

Взам. инв. №

Подпись и дата

Инв. № подл.

Ведомость основных комплектов рабочих чертежей (строение 1)

Обозначение	Наименование	Примечание
01-ВЕН/18-СК13-АС1-С1	Общие архитектурные решения	
01-ВЕН/18-СК13-АС2-С1	Стеновые и кровельные ограждающие конструкции	
01-ВЕН/18-СК13-КЖ1-С1	Конструкции железобетонные. Фундаменты	
01-ВЕН/18-СК13-КЖ1И-С1	Конструкции железобетонные. Фундаменты. Изделия	
01-ВЕН/18-СК13-КЖ2-С1	Конструкции железобетонные. Цокольные панели	
01-ВЕН/18-СК13-КЖ2И-С1	Конструкции железобетонные. Цокольные панели. Изделия	
01-ВЕН/18-СК13-КЖ3-С1	Конструкции железобетонные. Колонны	
01-ВЕН/18-СК13-КЖ3И-С1	Конструкции железобетонные. Колонны. Изделия	
01-ВЕН/18-СК13-КЖ4-С1	Конструкции железобетонные. Полы.	
01-ВЕН/18-СК13-КЖ5-С1	Конструкции железобетонные. Плиты перекрытий	
01-ВЕН/18-СК13-КМ1-С1	Конструкции металлические. Покрытие	
01-ВЕН/18-СК13-КМ2-С1	Конструкции металлические. Наружный фахверк, каркас пристраиваемых помещений, наружные лестницы.	
01-ВЕН/18-СК13-КМ3-С1	Конструкции металлические. Внутренний фахверк, внутренние лестницы.	
01-ВЕН/18-СК13-ЭОМ-С1	Электрическое освещение и электрооборудование	
01-ВЕН/18-СК13-ВК-С1	Внутренние системы водоснабжения и канализации	
01-ВЕН/18-СК13-ОВ-С1	Отопление, вентиляция и кондиционирование	
01-ВЕН/18-СК13-ПС-С1	Пожарная сигнализация	
01-ВЕН/18-СК13-АК-С1	Автоматизация комплексная	

Ведомость основных комплектов рабочих чертежей (внутриплощадочные решения)

Обозначение	Наименование	Примечание
01-ВЕН/18-СК13-ГП	Генеральный план	
01-ВЕН/18-СК13-ЭС	Электроснабжение	
01-ВЕН/18-СК13-НВК	Наружные сети водоснабжения и канализации	
01-ВЕН/18-СК13-ТС	Тепловые сети	
01-ВЕН/18-СК13-НСС	Наружные сети связи	
01-ВЕН/18-СК13-КПП	Контрольно-пропускной пункт	

Ведомость ссылочных документов

Обозначение	Наименование	Примечание
СП 57.13330.2011	Складские здания	
Федеральный закон от 22.07.2008 N 123-ФЗ	Технический регламент о требованиях пожарной безопасности (с изменениями на 2 июля 2013 года)	
СП 1.13130.2009	Системы противопожарной защиты. Эвакуационные пути и выходы (с изменениями №1)	
СП 2.13130.2012	Системы противопожарной защиты. Обеспечение огнестойкости объектов защиты (с изменением N 1)	
СП 4.13130.2013	Системы противопожарной защиты. Ограничение распространения пожара на объектах защиты. Требования к объемно-планировочным и конструктивным решениям	
СП 16.13330.2012	Стальные конструкции	
СП 20.13330.2011	Нагрузки и воздействия	
СП 28.13330.2012	Защита строительных конструкций от коррозии	
СП 70.13330.2012	Несущие и ограждающие конструкции	
СП 131.13330.2012	Строительная климатология	
СНиП 12-03-2001	Безопасность труда в строительстве. Часть 1. Общие требования	
СНиП 12-04-2002	Безопасность труда в строительстве. Часть 2. Строительное производство	

Технико-экономические показатели

№ п/п	Наименование	Ед. изм.	Кол-во
1	Общая площадь	м ²	4421.61
2	Строительный объем, в т.ч.	м ³	40440.90
3	Площадь застройки	м ²	4156.43

						01-ВЕН/18-СК13-АС1-С1				
						«Производственно-складской комплекс №13 «Industrial City», расположенный по адресу: Московская область, Городской округ Подольск, деревня Новоселки, территория Технопарка, 13»				
Изм.	Кол.уч.	Лист	№ док	Подпись	Дата	Строение 1		Стадия	Лист	Листов
Разраб.		Якунина			04.18			Р	1	33
Проверил		Черкасов			04.18					
ГИП		Авдулов			04.18	Общие данные (начало)		ООО "КУРСКРЕГИОНПРОЕКТ"		
Н. контр.		Авдулов			04.18					

Формат А3

Инв. № подл.

Подпись и дата

Взам. инв. №

Ведомость рабочих чертежей комплекта 01-ВЕН/18-СК 13-АС1-С1		
Лист	Наименование	Примечание
1	Общие данные (начало)	
2	Общие данные (продолжение)	
3	Общие данные (окончание)	
4	Фасады в осях Г-А и А-Г. Фасады в осях 1-7 и 7-1	
5	Цветовое решение фасадов в осях Г-А и А-Г, 1-7 и 7-1. Ведомость отделки фасадов	
6	Схема заполнения дверных проемов. План на отм. 0,000	
7	План полов на отм. 0,000. Экспликация полов	
8	Схема заполнения дверных проемов. План на отм. +3.600	
9	План полов на отм. +3.600. Экспликация полов	
10	План кровли	
11	Разрез 1-1. Рразрез 2-2. Узел 1, 2	
12	Ведомость отделки помещений. Блок 1	
13	Ведомость отделки помещений. Блок 2	
14	Ведомость отделки помещений. Блок 3	
15	Ведомость отделки помещений. Блок 4	
16	Ведомость отделки помещений. Блок 5	
17	Ведомость отделки помещений. Блок 6	
18	Ведомость отделки технических помещений	
19	Двери внутренние. Общие указания	
20	Спецификация внутренних дверей (начало)	
21	Спецификация внутренних дверей (продолжение)	
22	Спецификация внутренних дверей (продолжение)	
23	Спецификация внутренних дверей (окончание) Сводная спецификация внутренних дверей	
24	Дверной блок Тип 3-7, 3-7.1, 4-7, 4-7.1	
25	Дверной блок Тип 3-10, 3-10.1, 4-10, 4-10.1	

Рабочая документация разработана в соответствии с градостроительным планом земельного участка, заданием на проектирование, градостроительным регламентом, документами об использовании земельного участка для строительства, техническими регламентами, в том числе устанавливающими требования по обеспечению безопасной эксплуатации зданий, строений, сооружений и безопасного использования прилегающих к ним территорий, и с соблюдением технических условий.

Главный инженер проекта _____ Авдулов П.И.

Ведомость рабочих чертежей комплекта 01-ВЕН/18-СК 13-АС1-С1		
Лист	Наименование	Примечание
26	Раскладка стеновых панелей по оси 2,3,4,5,6. Спецификация внутренних сэндвич-панелей	
27	Вид в осях А-Г	
28	Узлы 1, 3	
29	Узлы 4, 5, 5а	
30	Узлы 7, 8	
31	Узел 10	
32	Узлы А-Г	
33	Ведомость фасонных элементов	

Изм.	Кол.уч.	Лист	№ док	Подпись	Дата
Разраб.		Якунина			04.18
Проверил		Черкасов			04.18
ГИП		Авдулов			04.18
Н. контр.		Авдулов			04.18

01-ВЕН/18-СК13-АС1-С1				
«Производственно-складской комплекс №13 «Industrial City», расположенный по адресу: Московская область, Городской округ Подольск, деревня Новоселки, территория Технопарка, 13»				
Строение 1		Стадия	Лист	Листов
		Р	2	
Общие данные (продолжение)		ООО"КУРСКРЕГИОНПРОЕКТ"		

Формат А3

Инв. № подл.	Подпись и дата	Взам. инв. №

- Общие данные:
- Комплект чертежей марки 01-ВЕН/18-СК 13-АС1-С1 разработан по заданию на проектирование, выданному Заказчиком. Объект строительства – “Производственно-складской комплекс №13 “Industrial City”, расположенный по адресу: Московская область, Городской округ Подольск, деревня Новоселки, территория Технопарка,13.
 - Чертежи разработаны для следующих условий строительства:
 - расчетный вес снегового покрова для района III – 180 кг/м²;
 - температура наиболее холодной пятидневки: обеспеченностью 0,92 –минус 25°С, обеспеченностью 0,98 –минус 29°С;
 - нормативное значение ветрового давления – 23 кг/м²;
 - уровень ответственности здания – II (нормальный);
 - степень огнестойкости здания – III;
 - класс конструктивной пожарной опасности – С0;
 - среда неагрессивная по отношению к металлоконструкциям.
 - За отметку 0,000 принята отметка чистого пола первого этажа, что соответствует абсолютной отметке 168,70 (Балтийская система высот).
 - Проектируемый производственно-складской комплекс представляет собой здание прямоугольное в плане размерами в осях 108,0 м x 33,0 м, состоящее из производственной зоны,административно-бытовой части и технических помещений. Высота здания от уровня чистого пола до верха парапета составляет 10,850 м. Производственно-складской комплекс запроектирован одноэтажным. Помещение производства (пом.№108) имеет макс. отм. от уровня чистого пола до низа выступающих строительных конструкций – +8.125. Высота потолка офисов и административных помещений – 2,7 м до подвесного потолка, высота потолка бытовых помещений (раздевалок, санузлов)-2,7 м. Высота потолка коридоров –2,7 м.

В Административно-бытовом блоке расположены: тамбур (пом.№101), коридор (пом. №102), кабинет (пом. №103), санузлы (пом. №104), умывальная (пом. №105), комната уборочного инвентаря (№пом.106), кабинет (пом.№107). Производственная зона (пом.№108).

Технические помещения: ИТП. Водомерный узел (пом.№109)

Помещения разных категорий В1,В2,В3 по взрывопожарной и пожарной опасности отделены одно от другого, а так же от помещений категории В4,Д и коридоров противопожарными стенами 2 –го типа и перегородками 1-го типа, перекрытиями 3–го типа.

Межкомнатные перегородки выполнены из ГКЛ-12,5мм, в два слоя гипсокартона, толщиной листа 12,5мм, в помещениях с влажным режимом из влагостойких гипсокартонных листов – 125мм, в два слоя гипсокартона, толщиной листа 12,5мм. Внутренняя сторона сэндвич-панелей обшивается листами ГКЛ-12,5мм, в два слоя гипсокартона, толщиной листа 12,5мм слоями без минераловатного утеплителя.

Двери выходов из здания металлические утепленные, внутренние – металлические, деревянные с ламинированием. В противопожарных стенах и перегородках установлены противопожарные двери с пределом огнестойкости- EI30. Наружные ворота – металлические утепленные, подъемно-секционные.

Оконные блоки выполнены из ПВХ профилей с двухкамерным стеклопакетом.

Кровля здания плоская с уклоном 3%, имеющая отметку верха парапета +10.600.

Водоотвод организованный, внутренний. Водоотводных воронок – 22 шт.

Конструктивная схема здания – железобетонный сборный каркас. Несущий каркас здания – ж/б колонны квадратного сечения 500х500мм, устанавливаемые с шагом 11,0 x 18,0 м. В здании применяются фундаменты мелкого заложения. Фундаменты под железобетонные колонны – сборно-монолитные отдельностоящие. Состоят из стакана заводского изготовления и плитной части, выполняемой на строительной площадке. Фундаменты под основные стойки фахверка – монолитные отдельностоящие. Покрытие здания выполняется из ферм. Подстропильные фермы пролетом 11 м устанавливаются вдоль цифровых осей здания. Стропильные фермы пролетом 18 м устанавливаются вдоль буквенных осей с шагом 5,5 м. Для обеспечения устойчивости ферм в здании предусмотрена система связей по покрытию. По периметру здания в уровне верхних поясов ферм устанавливаются крестовые горизонтальные связи из □ 100х60х3.

По фермам укладывается профилированный настил Н114–750–1.0. По стенам здания устраиваются фахверковые элементы – трубы квадратного и прямоугольного сечений – для фиксации стеновых сэндвич-панелей.






Кровля – Мембрана ECOLAST V–RP, Минераловатный утеплитель ТЕХНОРУФ ПРОФ – 40мм, Минераловатный утеплитель ТЕХНОРУФ Н ЭКСТРА – 100мм.

Полы и перекрытия выполнены:






 - монолитными железобетонными толщиной 160мм – в помещениях АБК.
 - Расчет конструкций выполнен на комбинации нагрузжений постоянными, длительными и временными нагрузками с учетом пространственной работы здания в линейной постановке с использованием программного комплекса Scad Office.
 - Материалы конструкций указаны в рабочих чертежах и технической спецификации металла.
 - Изготовление и монтаж строительных конструкций выполнить в соответствии с требованиями следующих нормативных документов:
 - СП 16.13330.2011 “Стальные конструкции”;
 - СП 70.13330.2012 “Несущие и ограждающие конструкции”;
 - СП 53-101-98 “Изготовление и контроль качества стальных строительных конструкций”;
 - ГОСТ 23118-2012 “Конструкции стальные строительные. Общие технические условия”;
 - Заводские сварные швы выполнять по ГОСТ 14771-76 и ГОСТ 23518-79 в среде углекислого газа по ГОСТ 8050-85 или в его смеси с аргоном по ГОСТ 10157-79 сварной проволокой Св-08Г2С. Монтажные сварные швы выполнить по ГОСТ 5264-80 и ГОСТ 11534-75 электродами Э42/аналог. Минимальные катеты сварных швов принимать по

- таблице 38 СП 16.13330.2011 “Стальные конструкции”, кроме тех случаев, когда катет шва указан на чертеже.
- Защиту металлоконструкций от коррозии выполнить в соответствии с требованиями СП 28.13330.2012. На предприятии-изготовителе нанести 2 слоя грунт-эмали ГФ-021/аналог (ГОСТ 25129-82) и 2 слоя эмали ПФ-115/аналог (ГОСТ 6465-76). Общая толщина лакокрасочного покрытия должна быть не менее 80мкм.
 - Все работы по строительству объекта и эксплуатации грузоподъемных механизмов необходимо вести в строгом соответствии с требованиями СП 45.13330.2012 “Земляные сооружения, основания и фундаменты. Актуализированная редакция СНиП 3.02.01-87”, СП 70.13330.2012 “Несущие и ограждающие конструкции. Актуализированная редакция СНиП 3.03.01-87”; СП 28.13330.2012 “Защита строительных конструкций от коррозии. Актуализированная редакция СНиП 2.03.11-85”; СНиП 12-03-2001 “Безопасность труда в строительстве. Часть 1. Общие требования”; СНиП 12-04-2002 “Безопасность труда в строительстве. Часть2. Строительное производство”. Организация строительной площадки, участков работ и рабочих мест должна обеспечивать безопасность труда работающих на всех этапах производства работ. Необходимо выполнить ограждение опасных зон, устроить проходы, проезды и переходы с соблюдением правил движения строительного автотранспорта по территории строительной площадки, разместить административные, санитарно-бытовые помещения, знаки безопасности и наглядную агитацию по безопасности труда.
 - Технические решения, принятые в рабочих чертежах, соответствуют требованиям экологических, санитарно-гигиенических, противопожарных и других норм, действующих на территории Российской Федерации и обеспечивают безопасную для жизни и здоровья эксплуатацию объекта при соблюдении предусмотренных рабочими чертежами мероприятий.

						01-ВЕН/18-СК13-АС1-С1				
						«Производственно-складской комплекс №13 «Industrial City», расположенный по адресу: Московская область, Городской округ Подольск, деревня Новоселки, территория Технопарка, 13»				
Изм.	Кол.уч.	Лист	№ док	Подпись	Дата					
Разраб.		Якунина			04.18	Строение 1		Стадия	Лист	Листов
Проверил		Черкасов			04.18			Р	3	
						Общие данные (окончание)		ООО "КУРСКРЕГИОНПРОЕКТ"		
ГИП		Авдулов			04.18					
Н. контр.		Авдулов			04.18					

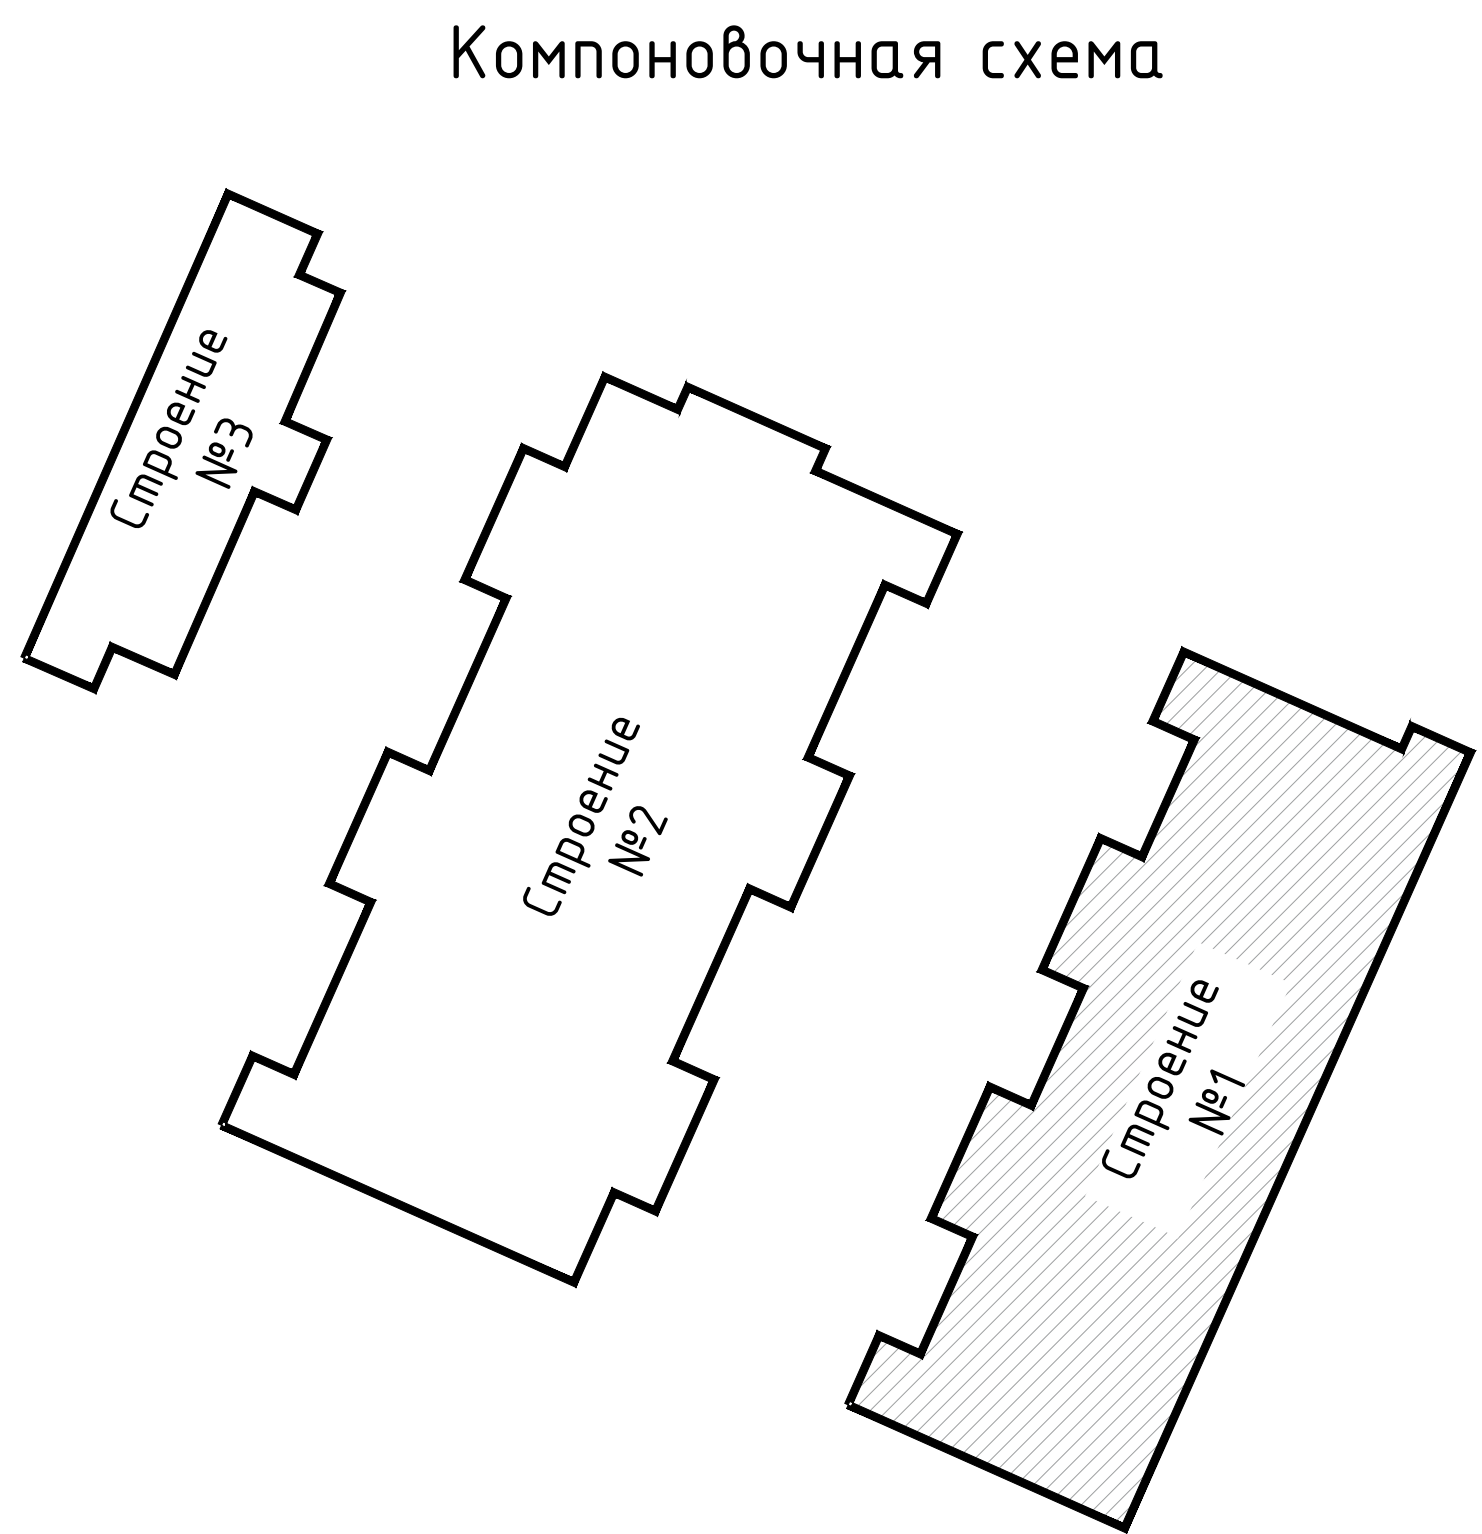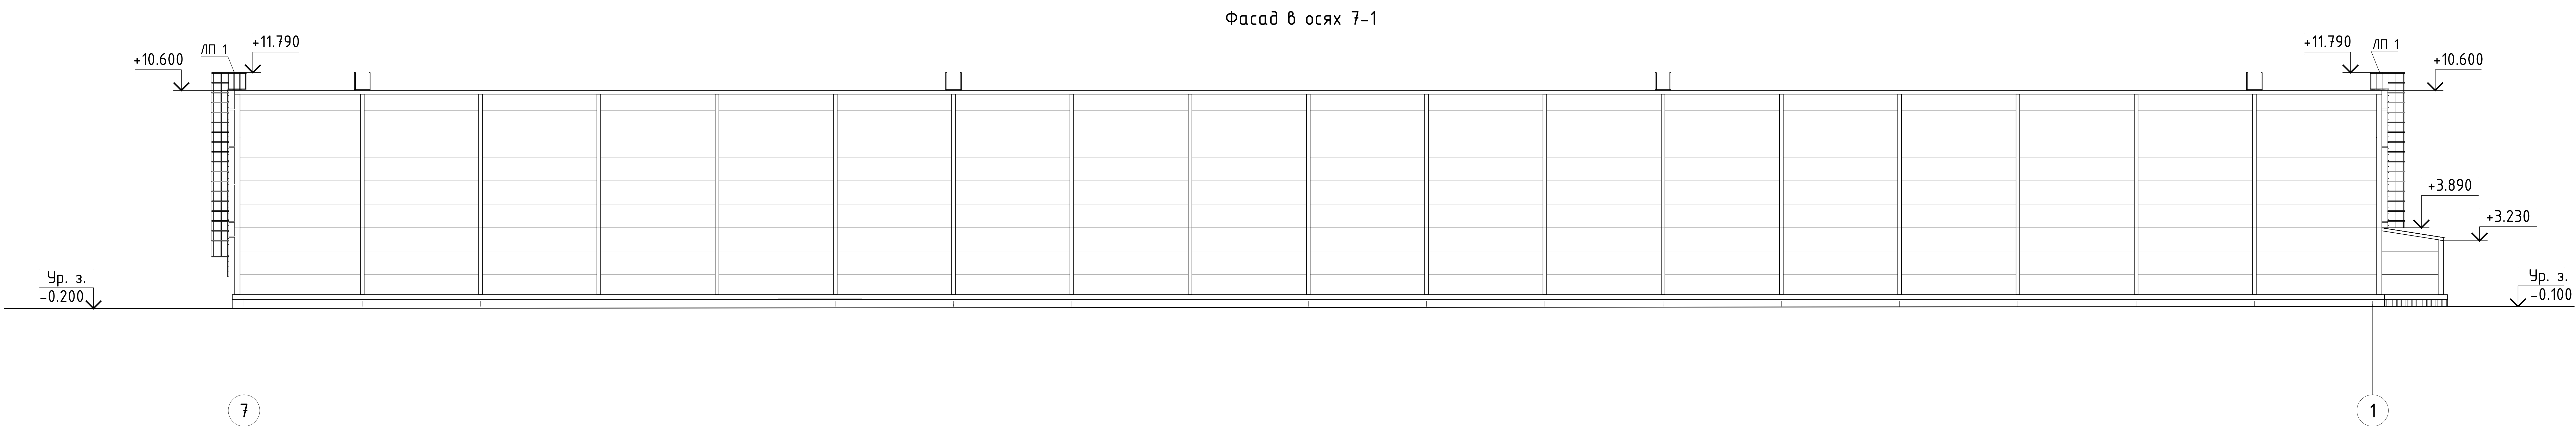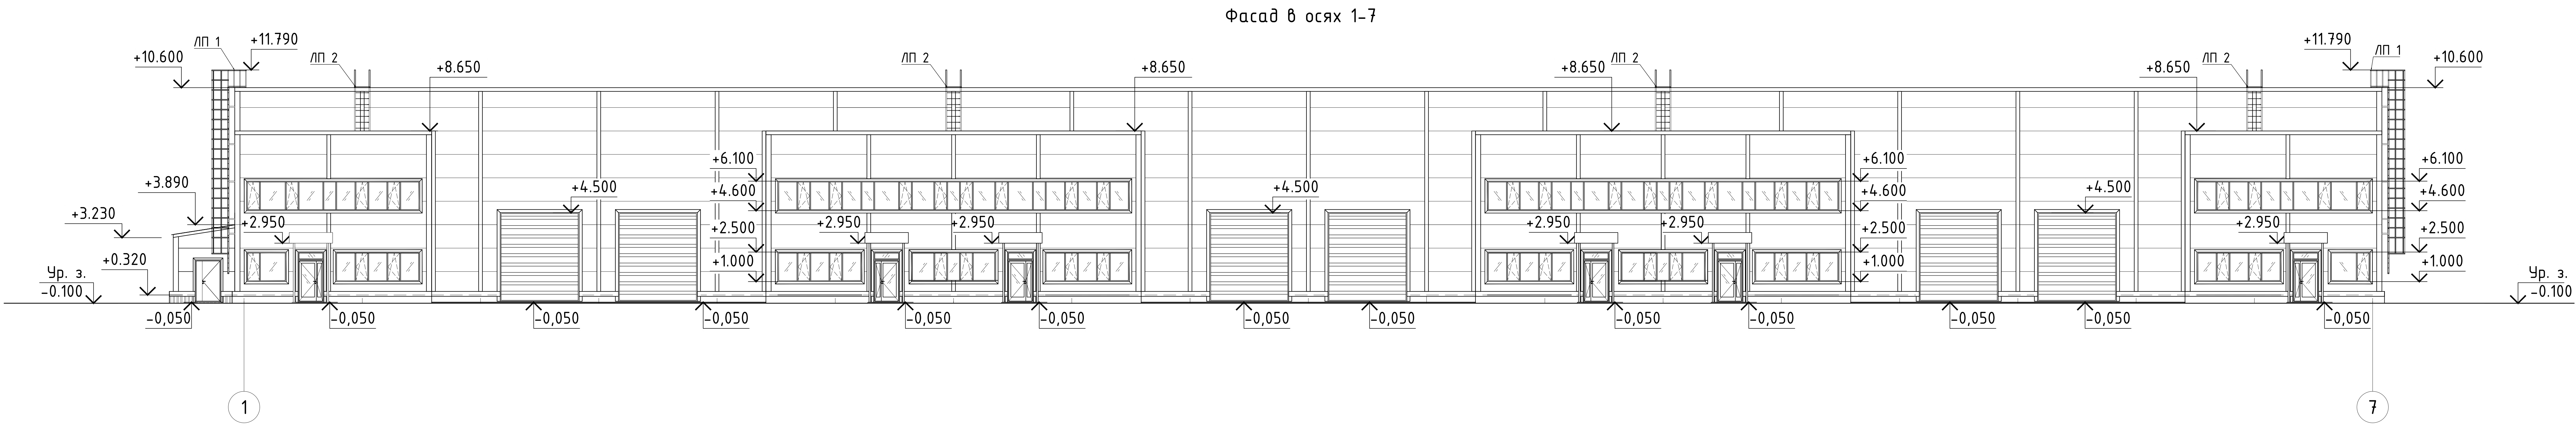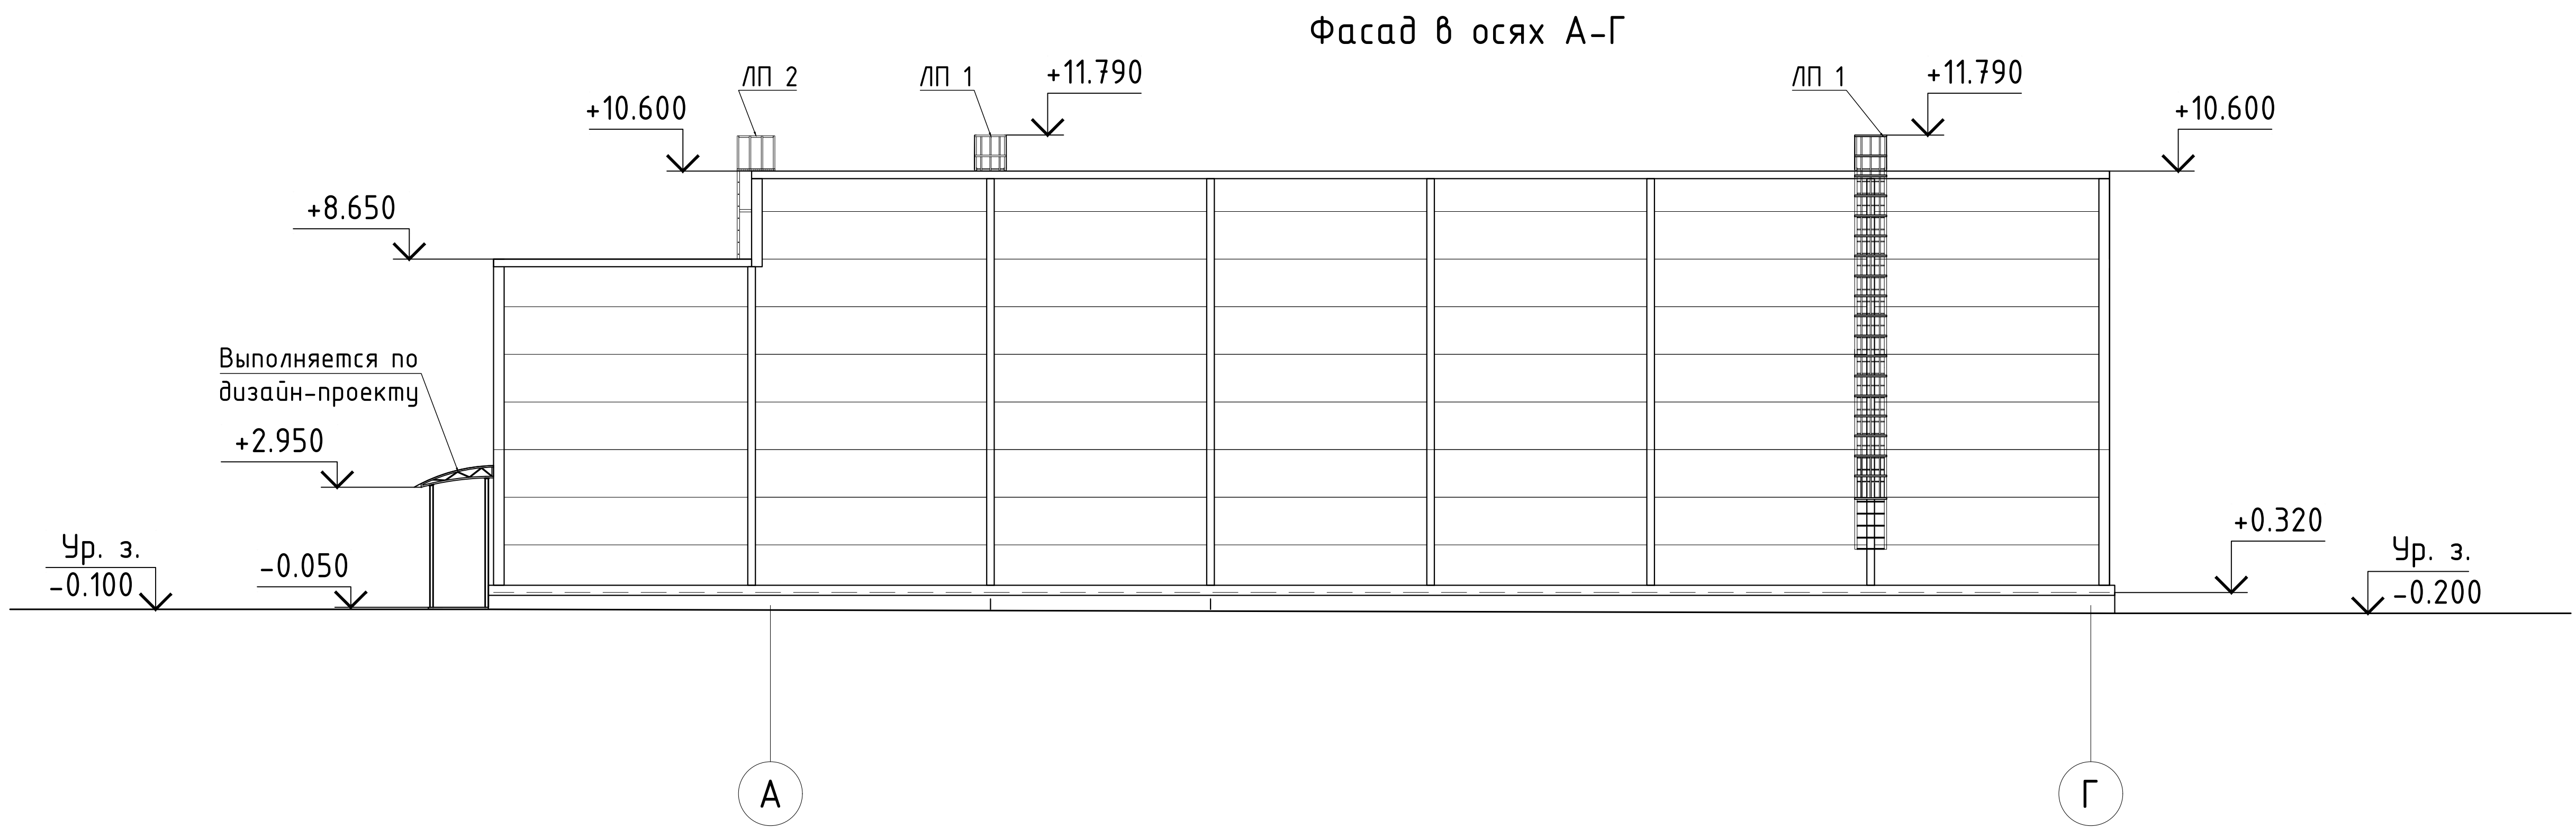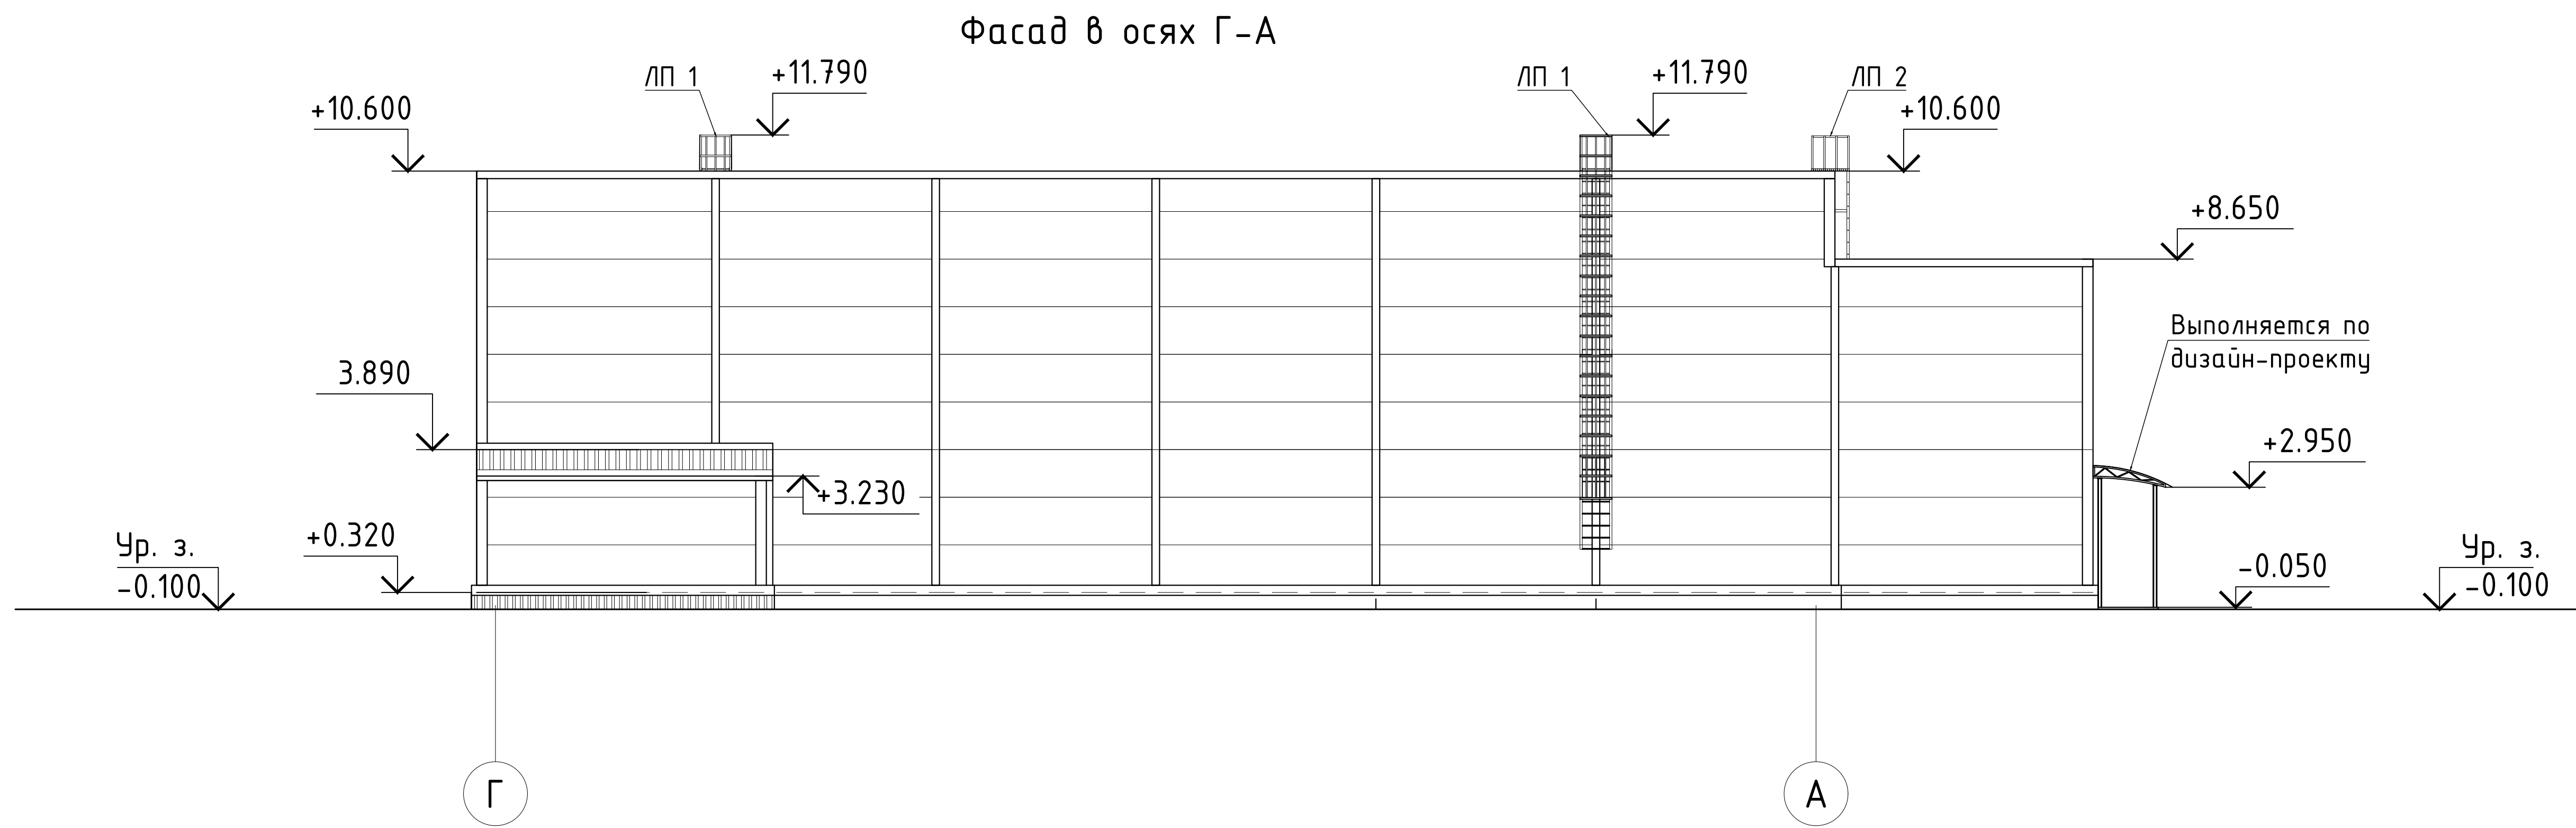


						01-ВЕН/18-СК13-АС1-С1			
						«Производственно-складской комплекс №13 «Industrial City», расположенный по адресу: Московская область, Городской округ Подольск, деревня Новоселки, территория Технопарка, 13»			
Изм.	Кол.уч.	Лист	№ док	Подпись	Дата	Строение 1	Стадия	Лист	Листов
Разраб.		Якунина			04.18		Р	4	
Проверил		Черкасов			04.18				
ГИП		Абдулов			04.18	Фасады в осях Г-А и А-Г. Фасады в осях 1-7 и 7-1	ООО"КУРСКРЕГИОНПРОЕКТ"		
Н. контр.		Абдулов			04.18				

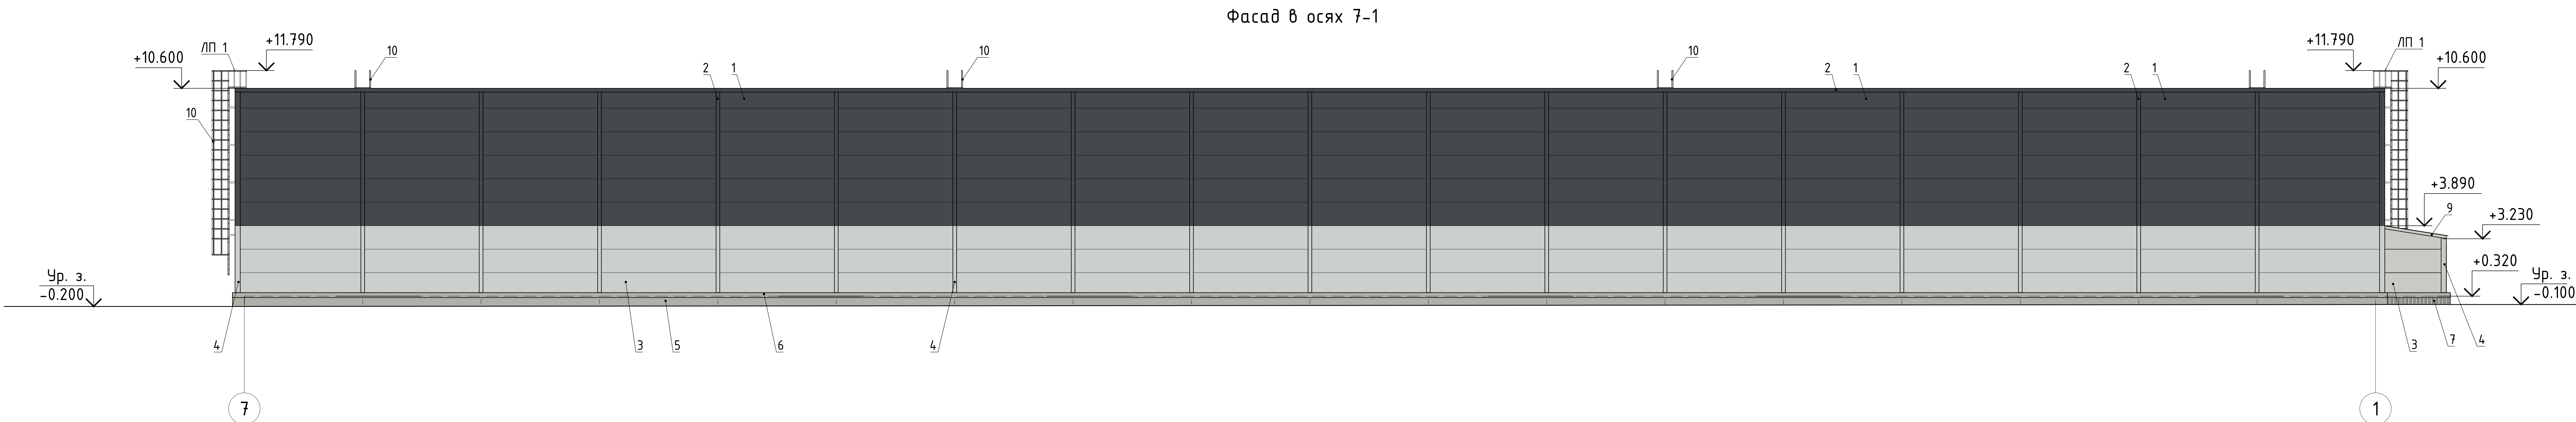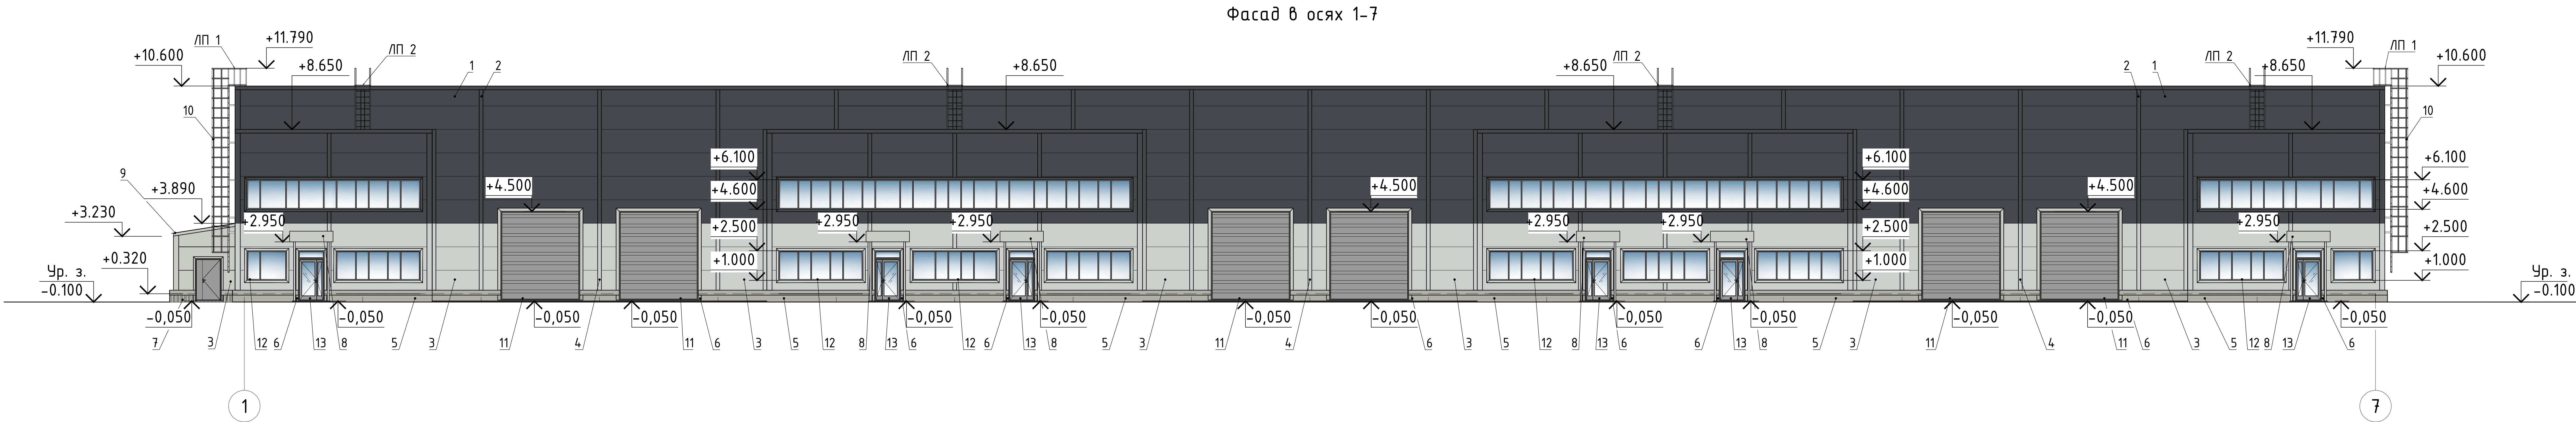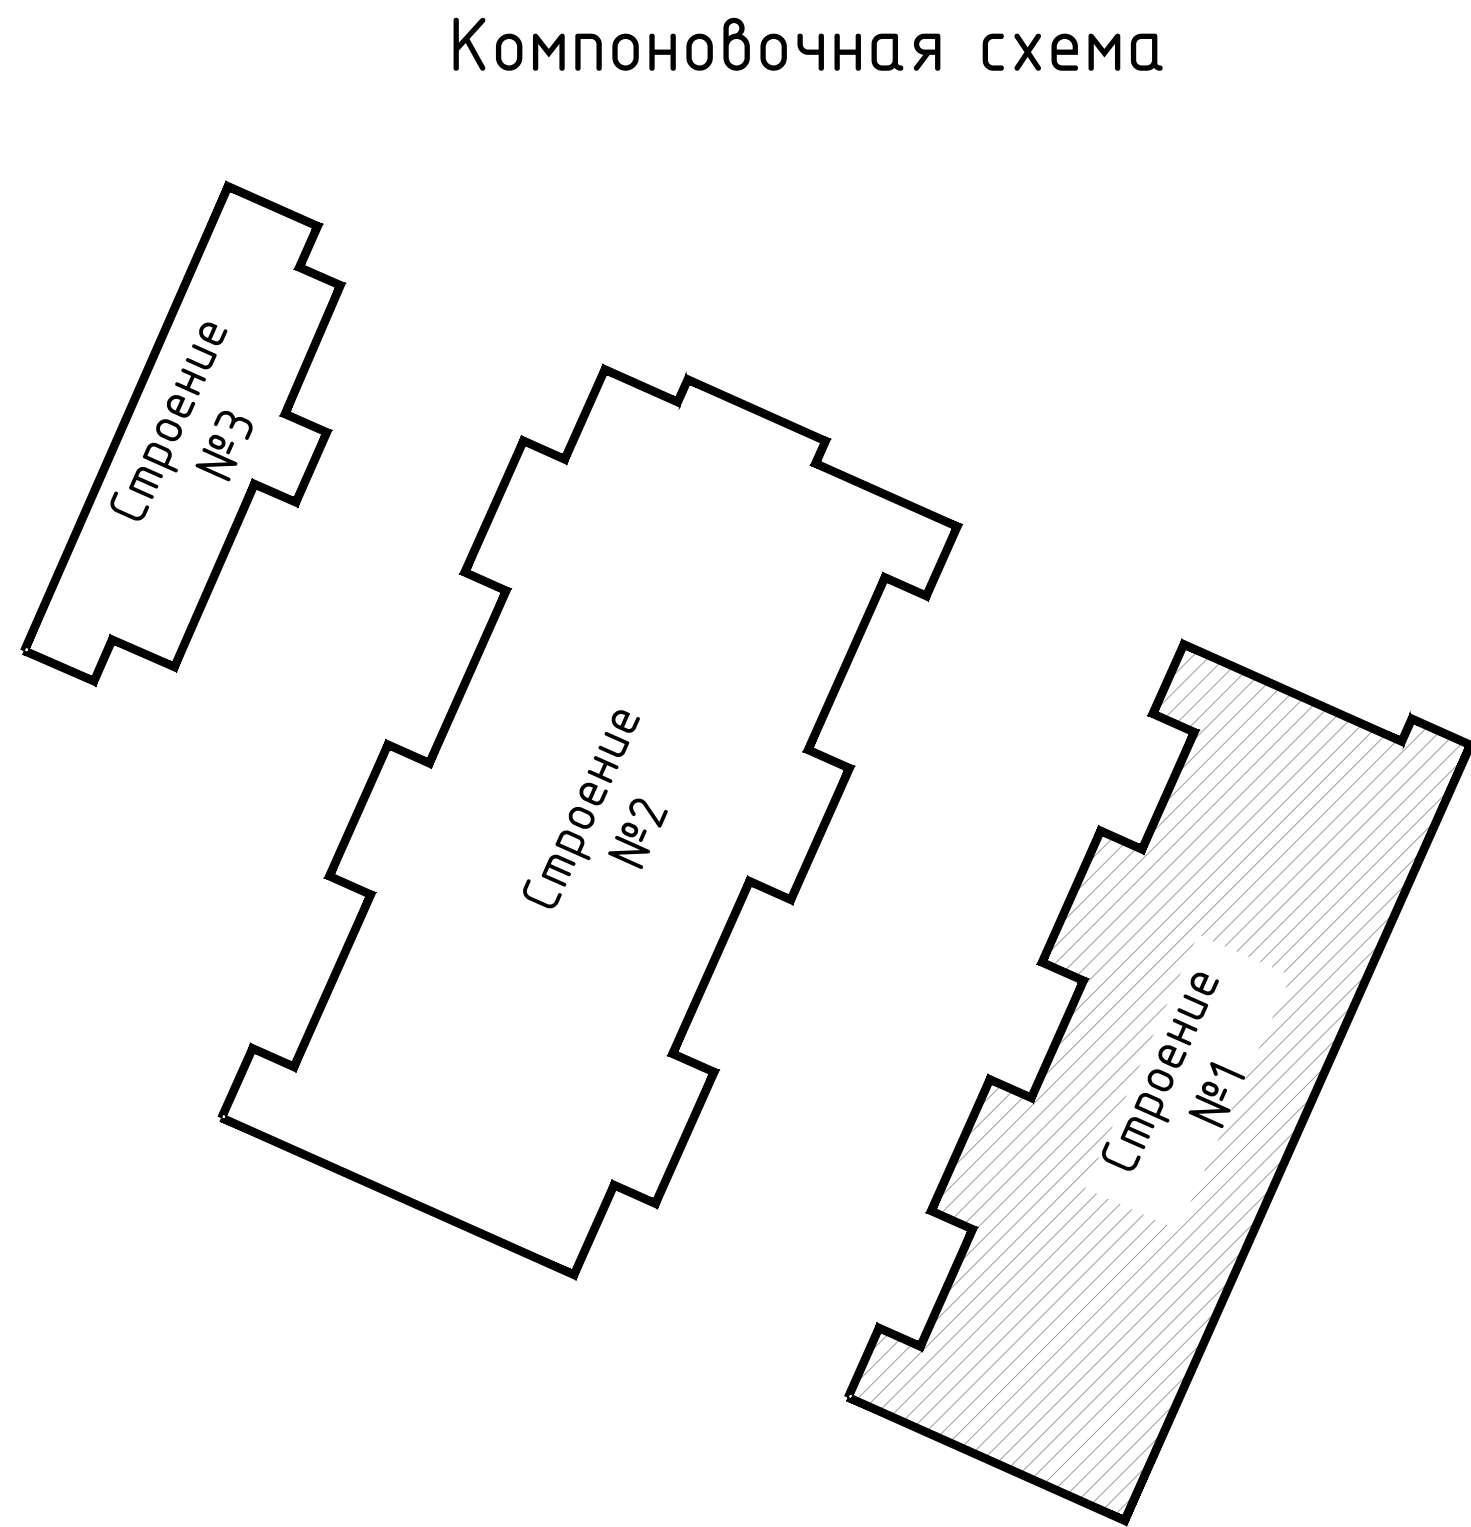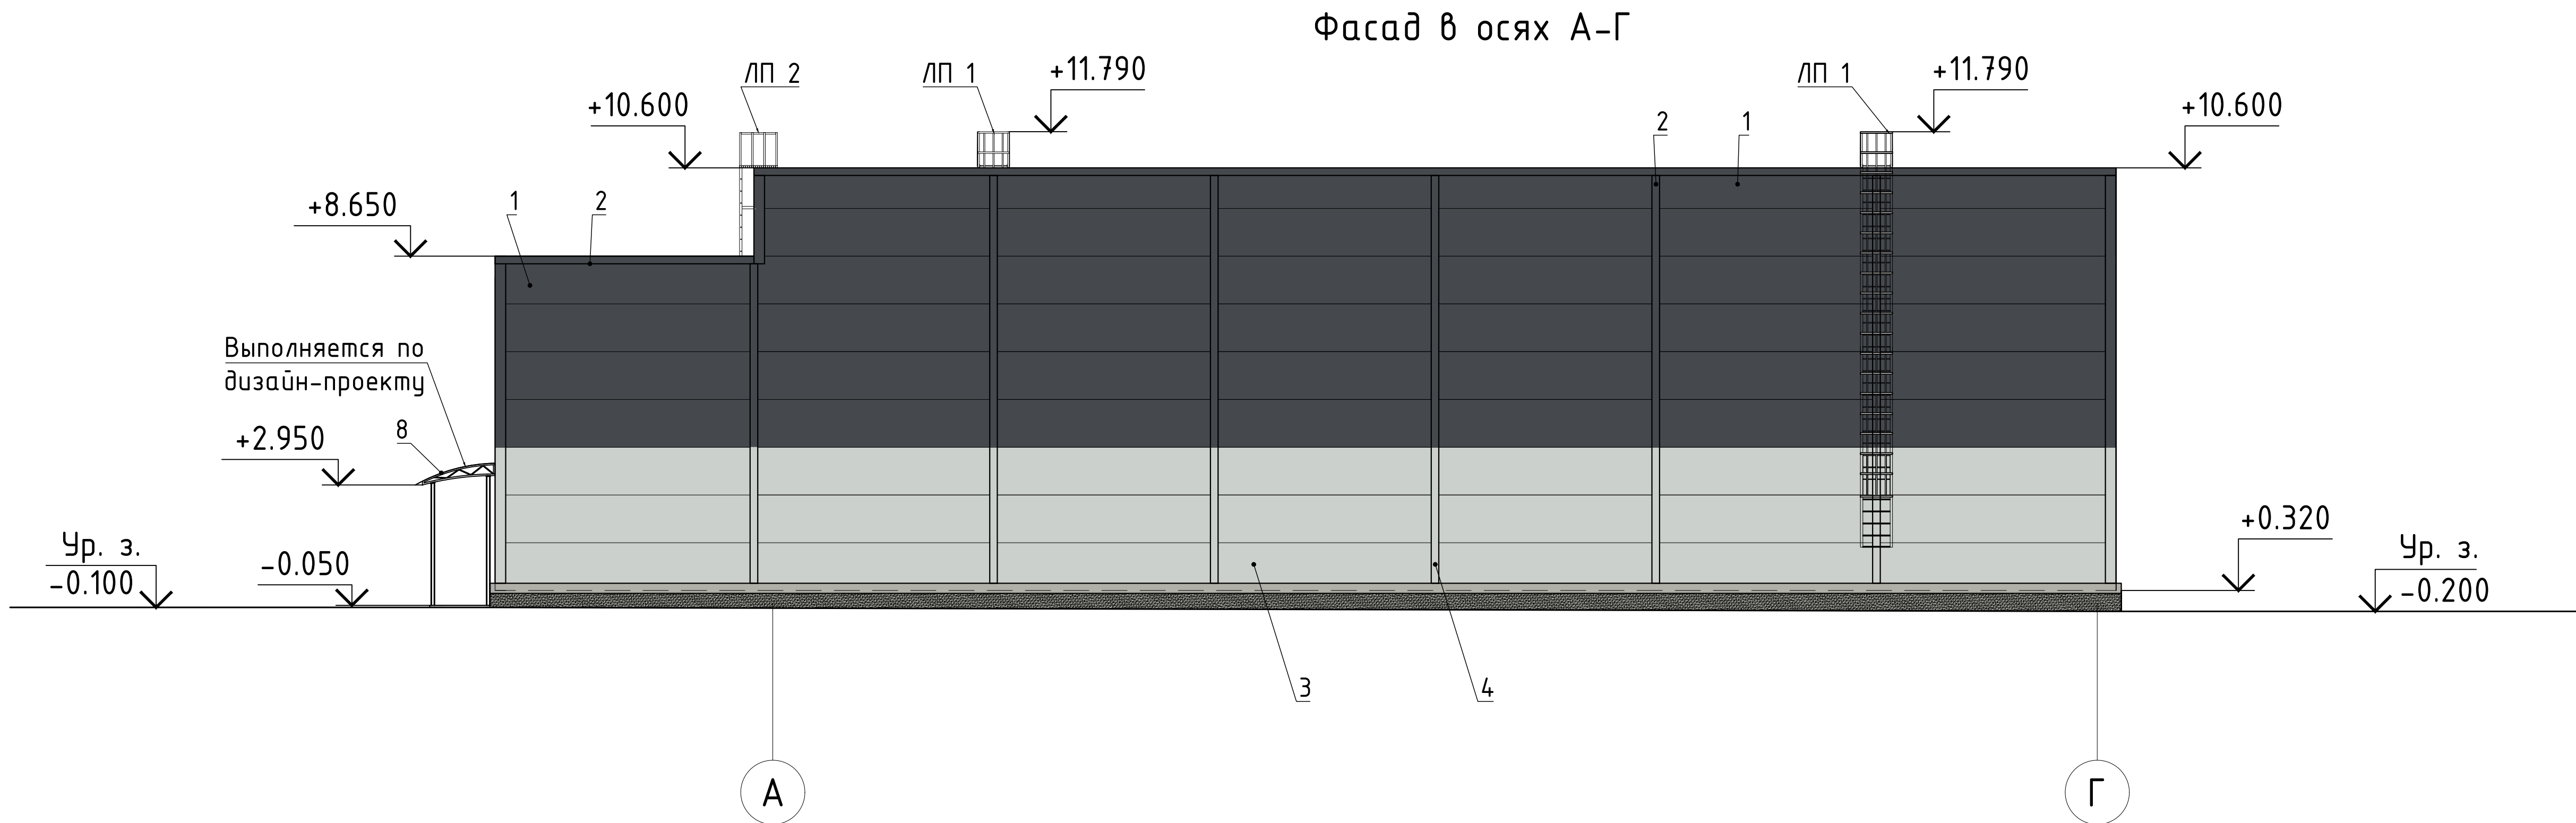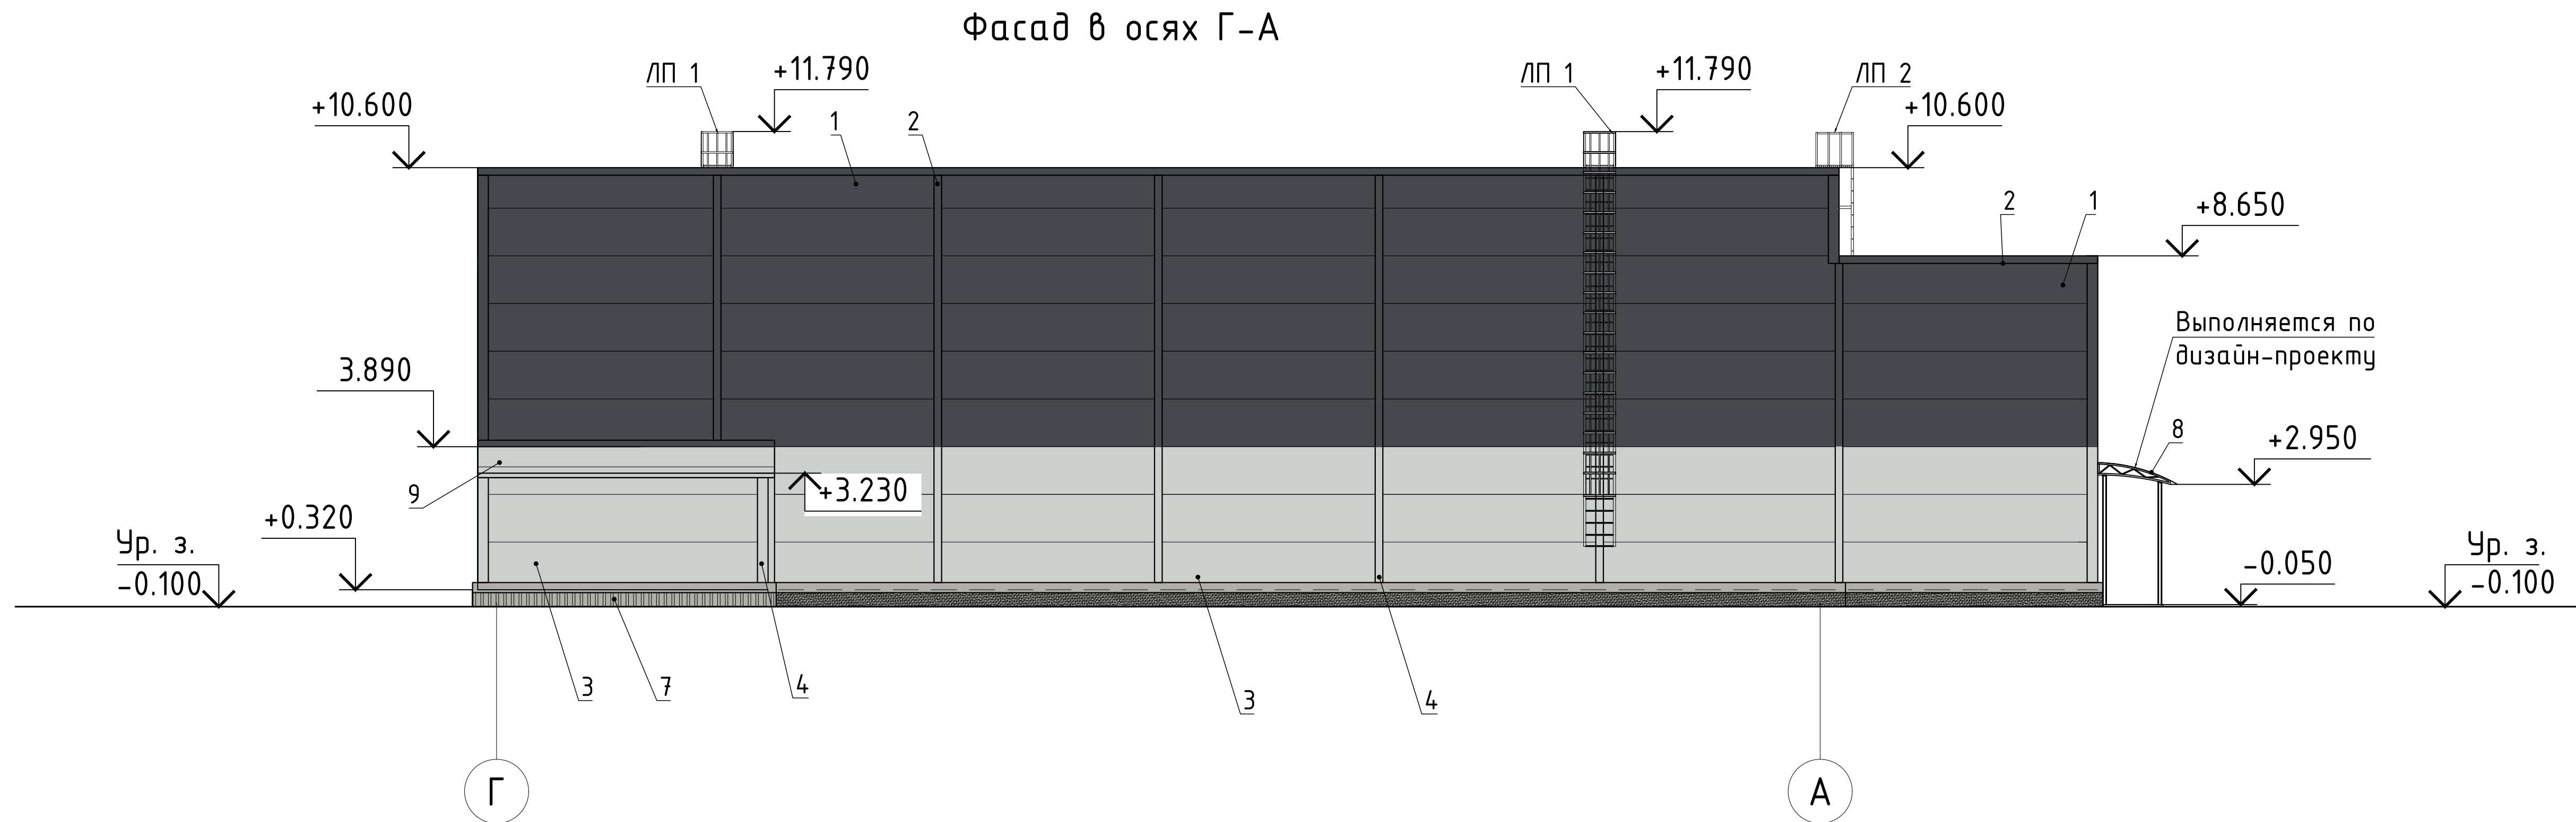


Ведомость отделки фасада

№ п/п	Наименование элемента фасада	Наименование и номер колера	Цвет	Примечание
1, 2	Стеновая сэндвич-панель, Фасонный элемент	RAL 7024		Альбом Classic RAL
3, 4, 8, 9, 10	Стеновая сэндвич-панель, Фасонный элемент, Навес, Кровельная сэндвич-панель, Металлическая лестница	RAL 7035		Альбом Classic RAL
5	Цокольная панель			Без окраски
6, 7	Фасонный элемент, Профлист	RAL 7038		Альбом Classic RAL
11	Ворота	RAL 9006		Альбом Classic RAL
12	Окна	RAL 7016		Альбом Classic RAL
13	Двери	RAL 7004		Альбом Classic RAL

						01-ВЕН/18-СК13-АС1-С1		
						«Производственно-складской комплекс №13 «Industrial City», расположенный по адресу: Московская область, Городской округ Подольск, деревня Новоселки, территория Технопарка, 13»		
Изм.	Колуч.	Лист	№ док	Подпись	Дата	Строение 1	Стадия	Лист
Разраб.	Якунина	04.18			04.18		Р	5
Проверил	Черкасов							
ГИП	Авдулов	04.18			04.18	Цветовое решение фасадов в осях Г-А и А-Г, 1-7 и 7-1. Ведомость отделки фасадов	ООО "КУРСКРЕГИОНПРОЕКТ"	
Н. контр.	Авдулов	04.18			04.18			

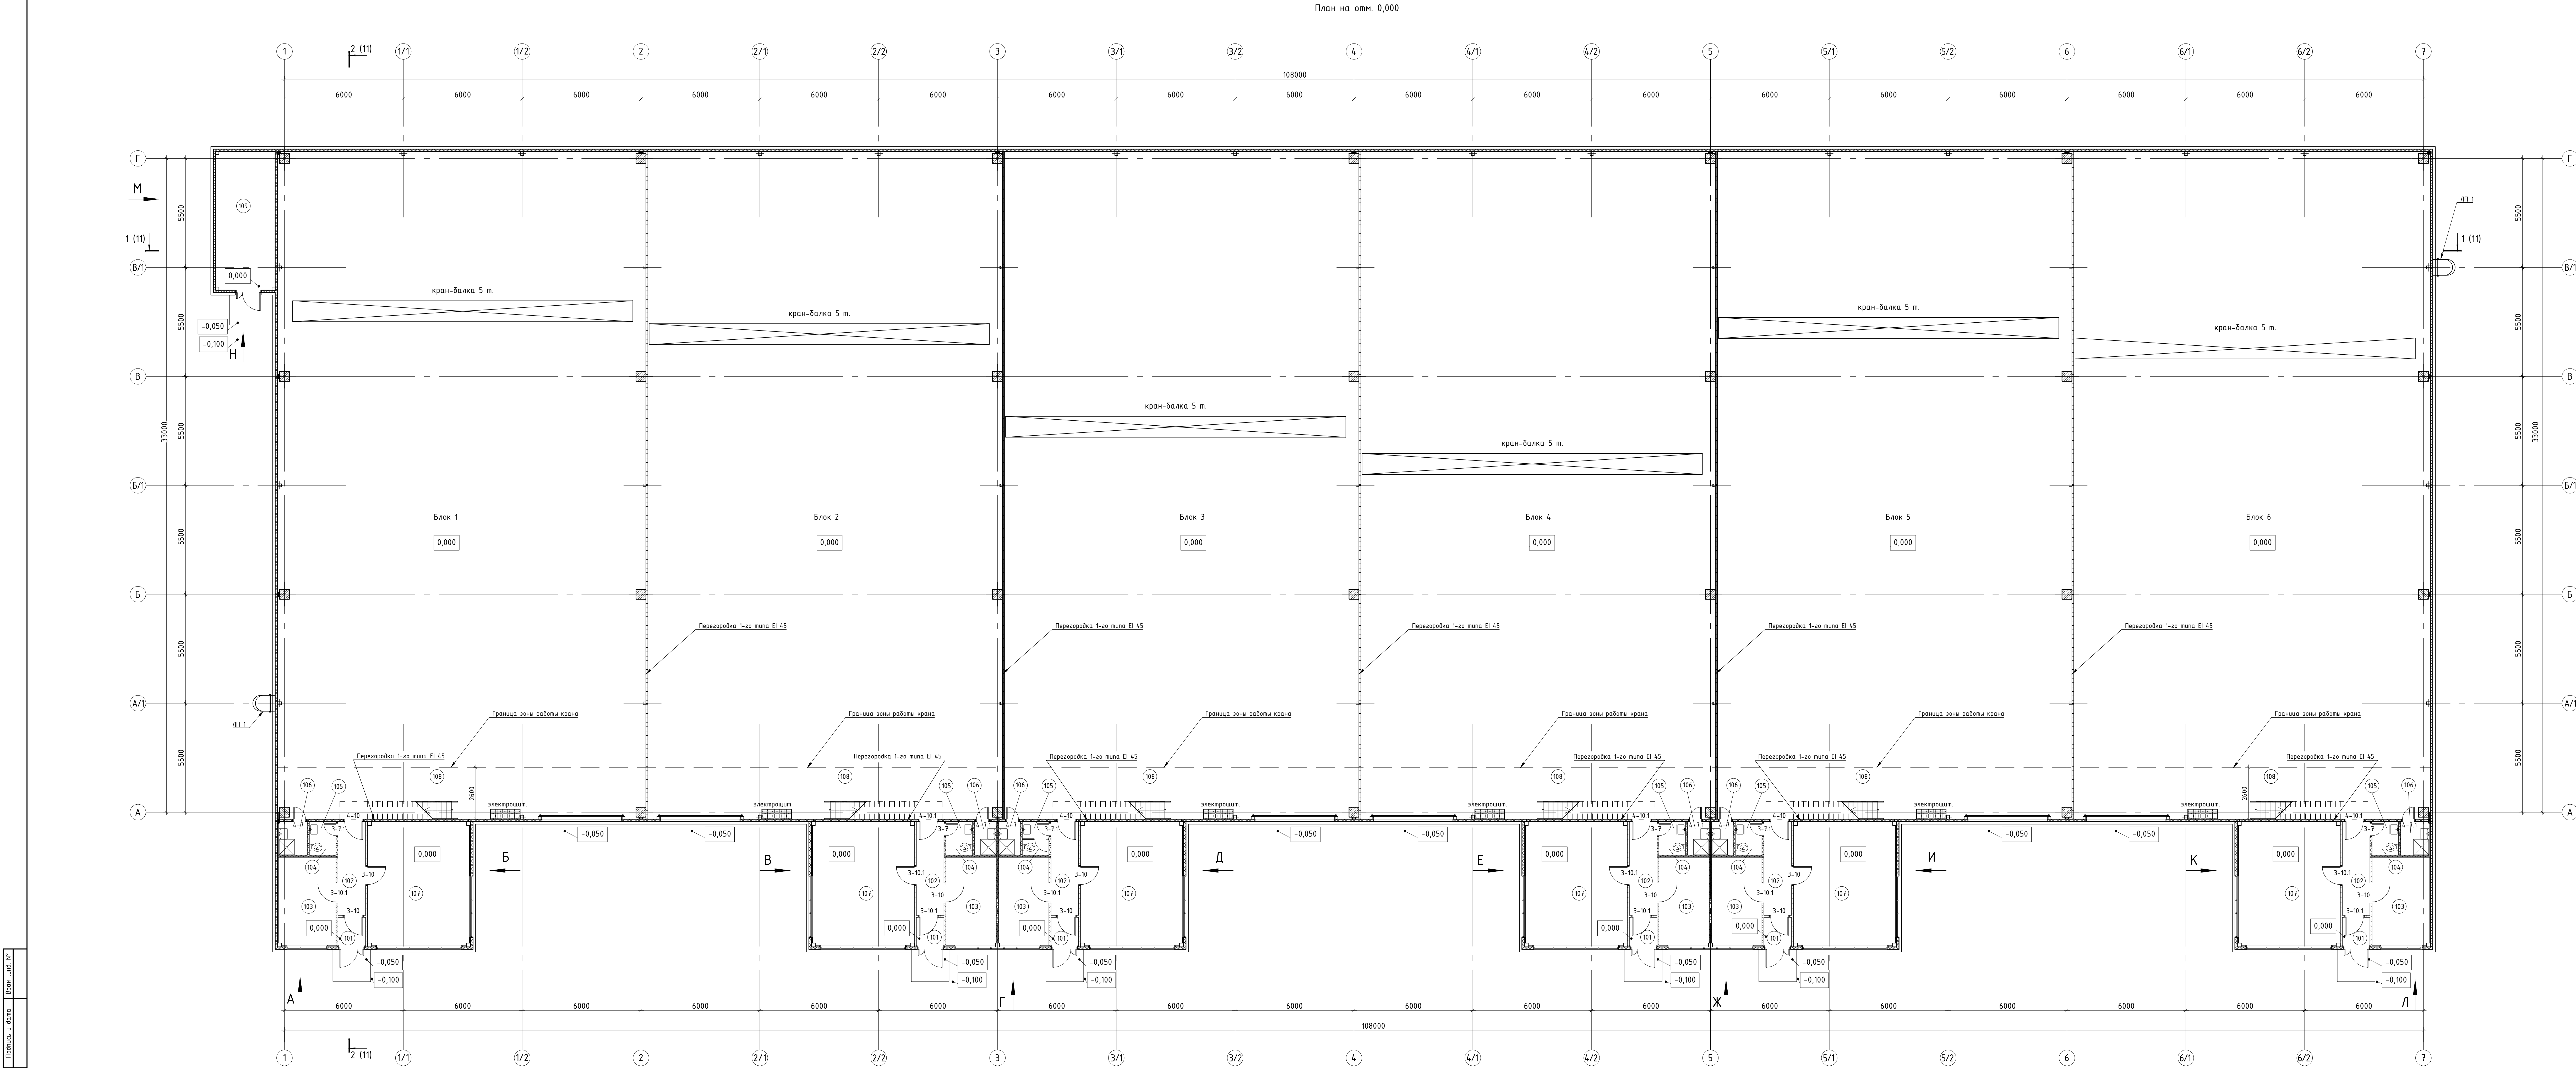

Экспликация помещений			
№ пом.	Наименование	Площадь, м²	Кат. пом.
Блок 1			
101	Танбур	2,82	
102	Коридор	6,62	
103	Кабинет	12,92	
104	Санузел	1,08	
105	Умывальная	1,17	
106	Пом. уборочного инвентаря	2,45	В4
107	Кабинет	32,23	
108	Производственное помещение	626,82	В4
Итого по блоку №1		685,31	
Блок 2			
101	Танбур	2,82	
102	Коридор	6,62	
103	Кабинет	11,35	
104	Санузел	1,08	
105	Умывальная	1,17	
106	Пом. уборочного инвентаря	1,85	В4
107	Кабинет	32,23	
108	Производственное помещение	603,23	В4
Итого по блоку №2		659,55	
Блок 3			
101	Танбур	2,82	
102	Коридор	6,62	
103	Кабинет	11,35	
104	Санузел	1,08	
105	Умывальная	1,17	
106	Пом. уборочного инвентаря	1,85	В4
107	Кабинет	32,23	
108	Производственное помещение	603,23	В4
Итого по блоку №3		659,55	
Блок 4			
101	Танбур	2,82	
102	Коридор	6,62	
103	Кабинет	11,35	
104	Санузел	1,08	
105	Умывальная	1,17	
106	Пом. уборочного инвентаря	1,85	В4
107	Кабинет	32,23	
108	Производственное помещение	603,23	В4
Итого по блоку №4		659,55	
Блок 5			
101	Танбур	2,82	
102	Коридор	6,62	
103	Кабинет	11,35	
104	Санузел	1,08	
105	Умывальная	1,17	
106	Пом. уборочного инвентаря	1,85	В4
107	Кабинет	32,23	
108	Производственное помещение	603,23	В4
Итого по блоку №5		659,55	
Блок 6			
101	Танбур	2,82	
102	Коридор	6,62	
103	Кабинет	12,92	
104	Санузел	1,08	
105	Умывальная	1,17	
106	Пом. уборочного инвентаря	2,45	В4
107	Кабинет	32,23	
108	Производственное помещение	606,60	В4
Итого по блоку №6		665,89	
Итого по этажу		3988,68	
Технические помещения			
109	ИТП, Водомерный узел	21,00	Д

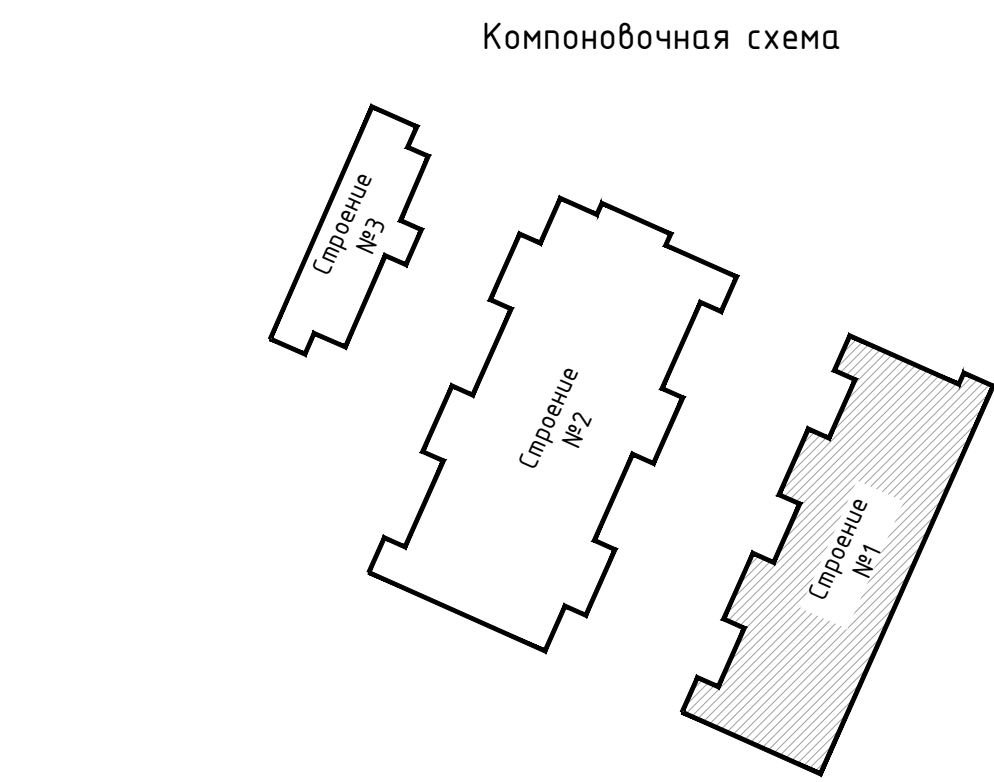

Условные обозначения

- Стена из сэндвич-панелей - 120 мм
- Перегородка из сэндвич-панелей - 100 мм
- Перегородки из гипсокартонных листов ГКЛ 2000x1200x12,5 ГОСТ 6266-97 - 125 мм
- Перегородки из гипсокартонных листов ГКЛ 2000x1200x12,5 ГОСТ 6266-97 - 125 мм
- Перегородки из гипсокартонных влагостойких листов ГКЛВ 2000x1200x12,5 ГОСТ 6266-97 - 125 мм

- Структура обозначения дверей:
- 3-10
 - ширина дверного проема в мм
 - 1 - наружная дверь/
 - 2 - наружная противопожарная дверь/
 - 3 - внутренняя дверь/
 - 4 - внутренняя противопожарная

Примечания:

- Чертежи и спецификации дверных проемов см. л. 19-25
- Тип 3 (маркировки 3-10, 3-7 и т.п.) - Внутренние двери.
- Тип 4 (марки 4-10) - Внутренние противопожарные двери.
- В пом. 101, 103, 107 (Блок 1-10) и 106 (Блок 5,6) наружные стены из сэндвич-панелей зашить гипсокартонными листами.
- Лестницы ЛП 1 см. альбом 01-БЕН/18-СК13-КМ3-С1
- Отверстия в перегородках выполнять по месту после монтажа перегородок.

Итого по блоку №6		Итого по блоку №5		Итого по блоку №4		Итого по блоку №3		Итого по блоку №2		Итого по блоку №1		Итого по этажу		--	-------------------	--	-------------------	--	-------------------	--	-------------------	--	-------------------	--	----------------	--	-------------------	--	-------------------	--	-------------------	--	-------------------	--	-------------------	--	-------------------	--	----------------	--	-------------------	--	-------------------	--	-------------------	--	-------------------	--	-------------------	--	-------------------	--	----------------	--	-------------------	--	-------------------	--	-------------------	--	-------------------	--	-------------------	--	-------------------	--	----------------	--	-------------------	--	-------------------	--	-------------------	--	-------------------	--	-------------------	--	-------------------	--	----------------	--	-------------------	--	-------------------	--	-------------------	--	-------------------	--	-------------------	--	-------------------	--	----------------	--	-------------------	--	-------------------	--	-------------------	--	-------------------	--	-------------------	--	-------------------	--	----------------	--	-------------------	--	-------------------	--	-------------------	--	-------------------	--	-------------------	--	-------------------	--	----------------	--	-------------------	--	-------------------	--	-------------------	--	-------------------	--	-------------------	--	-------------------	--	----------------	--	-------------------	--	-------------------	--	-------------------	--	-------------------	--	-------------------	--	-------------------	--	----------------	--	-------------------	--	-------------------	--	-------------------	--	-------------------	--	-------------------	--	-------------------	--	----------------	--	-------------------	--	-------------------	--	-------------------	--	-------------------	--	-------------------	--	-------------------	--	----------------	--	-------------------	--	-------------------	--	-------------------	--	-------------------	--	-------------------	--	-------------------	--	----------------	--	-------------------	--	-------------------	--	-------------------	--	-------------------	--	-------------------	--	-------------------	--	----------------	--	-------------------	--	-------------------	--	-------------------	--	-------------------	--	-------------------	--	-------------------	--	----------------	--	-------------------	--	-------------------	--	-------------------	--	-------------------	--	-------------------	--	-------------------	--	----------------	--	-------------------	--	-------------------	--	-------------------	--	-------------------	--	-------------------	--	-------------------	--	----------------	--	-------------------	--	-------------------	--	-------------------	--	-------------------	--	-------------------	--	-------------------	--	----------------	--	-------------------	--	-------------------	--	-------------------	--	-------------------	--	-------------------	--	-------------------	--	----------------	--	-------------------	--	-------------------	--	-------------------	--	-------------------	--	-------------------	--	-------------------	--	----------------	--	-------------------	--	-------------------	--	-------------------	--	-------------------	--	-------------------	--	-------------------	--	----------------	--	-------------------	--	-------------------	--	-------------------	--	-------------------	--	-------------------	--	-------------------	--	----------------	--	-------------------	--	-------------------	--	-------------------	--	-------------------	--	-------------------	--	-------------------	--	----------------	--	-------------------	--	-------------------	--	-------------------	--	-------------------	--	-------------------	--	-------------------	--	----------------	--	-------------------	--	-------------------	--	-------------------	--	-------------------	--	-------------------	--	-------------------	--	----------------	--	-------------------	--	-------------------	--	-------------------	--	-------------------	--	-------------------	--	-------------------	--	----------------	--	-------------------	--	-------------------	--	-------------------	--	-------------------	--	-------------------	--	-------------------	--	----------------	--	-------------------	--	-------------------	--	-------------------	--	-------------------	--	-------------------	--	-------------------	--	----------------	--	-------------------	--	-------------------	--	-------------------	--	-------------------	--	-------------------	--	-------------------	--	----------------	--	-------------------	--	-------------------	--	-------------------	--	-------------------	--	-------------------	--	-------------------	--	----------------	--	-------------------	--	-------------------	--	-------------------	--	-------------------	--	-------------------	--	-------------------	--	----------------	--	-------------------	--	-------------------	--	-------------------	--	-------------------	--	-------------------	--	-------------------	--	----------------	--	-------------------	--	-------------------	--	-------------------	--	-------------------	--	-------------------	--	-------------------	--	----------------	--	-------------------	--	-------------------	--	-------------------	--	-------------------	--	-------------------	--	-------------------	--	----------------	--	-------------------	--	-------------------	--	-------------------	--	-------------------	--	-------------------	--	-------------------	--	----------------	--	-------------------	--	-------------------	--	-------------------	--	-------------------	--	-------------------	--	-------------------	--	----------------	--	-------------------	--	-------------------	--	-------------------	--	-------------------	--	-------------------	--	-------------------	--	----------------	--	-------------------	--	-------------------	--	-------------------	--	-------------------	--	-------------------	--	-------------------	--	----------------	--	-------------------	--	-------------------	--	-------------------	--	-------------------	--	-------------------	--	-------------------	--	----------------	--	-------------------	--	-------------------	--	-------------------	--	-------------------	--	-------------------	--	-------------------	--	----------------	--	-------------------	--	-------------------	--	-------------------	--	-------------------	--	-------------------	--	-------------------	--	----------------	--	-------------------	--	-------------------	--	-------------------	--	-------------------	--	-------------------	--	-------------------	--	----------------	--	-------------------	--	-------------------	--	-------------------	--	-------------------	--	-------------------	--	-------------------	--	----------------	--	-------------------	--	-------------------	--	-------------------	--	-------------------	--	-------------------	--	-------------------	--	----------------	--	-------------------	--	-------------------	--	-------------------	--	-------------------	--	-------------------	--	-------------------	--	----------------	--	-------------------	--	-------------------	--	-------------------	--	-------------------	--	-------------------	--	-------------------	--	----------------	--	-------------------	--	-------------------	--	-------------------	--	-------------------	--	-------------------	--	-------------------	--	----------------	--	-------------------	--	-------------------	--	-------------------	--	-------------------	--	-------------------	--	-------------------	--	----------------	--	-------------------	--	-------------------	--	-------------------	--	-------------------	--	-------------------	--	-------------------	--	----------------	--	-------------------	--	-------------------	--	-------------------	--	-------------------	--	-------------------	--	-------------------	--	----------------	--	-------------------	--	-------------------	--	-------------------	--	-------------------	--	-------------------	--	-------------------	--	----------------	--	-------------------	--	-------------------	--	-------------------	--	-------------------	--	-------------------	--	-------------------	--	----------------	--	-------------------	--	-------------------	--	-------------------	--	-------------------	--	-------------------	--	-------------------	--	----------------	--	-------------------	--	-------------------	--	-------------------	--	-------------------	--	-------------------	--	-------------------	--	----------------	--	-------------------	--	-------------------	--	-------------------	--	-------------------	--	-------------------	--	-------------------	--	----------------	--	-------------------	--	-------------------	--	-------------------	--	-------------------	--	-------------------	--	-------------------	--	----------------	--	-------------------	--	-------------------	--	-------------------	--	-------------------	--	-------------------	--	-------------------	--	----------------	--	-------------------	--	-------------------	--	-------------------	--	-------------------	--	-------------------	--	-------------------	--	----------------	--	-------------------	--	-------------------	--	-------------------	--	-------------------	--	-------------------	--	-------------------	--	----------------	--	-------------------	--	-------------------	--	-------------------	--	-------------------	--	-------------------	--	-------------------	--	----------------	--	-------------------	--	-------------------	--	-------------------	--	-------------------	--	-------------------	--	-------------------	--	----------------	--	-------------------	--	-------------------	--	-------------------	--	-------------------	--	-------------------	--	-------------------	--	----------------	--	-------------------	--	-------------------	--	-------------------	--	-------------------	--	-------------------	--	-------------------	--	----------------	--	-------------------	--	-------------------	--	-------------------	--	-------------------	--	-------------------	--	-------------------	--	----------------	--	-------------------	--	-------------------	--	-------------------	--	-------------------	--	-------------------	--	-------------------	--	----------------	--	-------------------	--	-------------------	--	-------------------	--	-------------------	--	-------------------	--	-------------------	--	----------------	--	-------------------	--	-------------------	--	-------------------	--	-------------------	--	-------------------	--	-------------------	--	----------------	--	-------------------	--	-------------------	--	-------------------	--	-------------------	--	-------------------	--	-------------------	--	----------------	--	-------------------	--	-------------------	--	-------------------	--	-------------------	--	-------------------	--	-------------------	--	----------------	--	-------------------	--	-------------------	--	-------------------	--	-------------------	--	-------------------	--	-------------------	--	----------------	--	-------------------	--	-------------------	--	-------------------	--	-------------------	--	-------------------	--	-------------------	--	----------------	--	-------------------	--	-------------------	--	-------------------	--	-------------------	--	-------------------	--	-------------------	--	----------------	--	-------------------	--	-------------------	--	-------------------	--	-------------------	--	-------------------	--	-------------------	--	----------------	--	-------------------	--	-------------------	--	-------------------	--	-------------------	--	-------------------	--	-------------------	--	----------------	--	-------------------	--	-------------------	--	-------------------	--	-------------------	--	-------------------	--	-------------------	--	----------------	--	-------------------	--	-------------------	--	-------------------	--	-------------------	--	-------------------	--	-------------------	--	----------------	--	-------------------	--	-------------------	--	-------------------	--	-------------------	--	-------------------	--	-------------------	--	----------------	--	-------------------	--	-------------------	--	-------------------	--	-------------------	--	-------------------	--	-------------------	--	----------------	--	-------------------	--	-------------------	--	-------------------	--	-------------------	--	-------------------	--	-------------------	--	----------------	--	-------------------	--	-------------------	--	-------------------	--	-------------------	--	-------------------	--	-------------------	--	----------------	--	-------------------	--	-------------------	--	-------------------	--	-------------------	--	-------------------	--	-------------------	--	----------------	--	-------------------	--	-------------------	--	-------------------	--	-------------------	--	-------------------	--	-------------------	--	----------------	--	-------------------	--	-------------------	--	-------------------	--	-------------------	--	-------------------	--	-------------------	--	----------------	--	-------------------	--	-------------------	--	-------------------	--	-------------------	--	-------------------	--	-------------------	--	----------------	--	-------------------	--	-------------------	--	-------------------	--	-------------------	--	-------------------	--	-------------------	--	----------------	--	-------------------	--	-------------------	--	-------------------	--	-------------------	--	-------------------	--	-------------------	--	----------------	--	-------------------	--	-------------------	--	-------------------	--	-------------------	--	-------------------	--	-------------------	--	----------------	--	-------------------	--	-------------------	--	-------------------	--	-------------------	--	-------------------	--	-------------------	--	----------------	--	-------------------	--	-------------------	--	-------------------	--	-------------------	--	-------------------	--	-------------------	--	----------------	--	-------------------	--	-------------------	--	-------------------	--	-------------------	--	-------------------	--	-------------------	--	----------------	--	-------------------	--	-------------------	--	-------------------	--	-------------------	--	-------------------	--	-------------------	--	----------------	--	-------------------	--	-------------------	--	-------------------	--	-------------------	--	-------------------	--	-------------------	--	----------------	--	-------------------	--	-------------------	--	-------------------	--	-------------------	--	-------------------	--	-------------------	--	----------------	--	-------------------	--	-------------------	--	-------------------	--	-------------------	--	-------------------	--	-------------------	--	----------------	--	-------------------	--	-------------------	--	-------------------	--	-------------------	--	-------------------	--	-------------------	--	----------------	--	-------------------	--	-------------------	--	-------------------	--	-------------------	--	-------------------	--	-------------------	--	----------------	--	-------------------	--	-------------------	--	-------------------	--	-------------------	--	-------------------	--	-------------------	--	----------------	--	-------------------	--	-------------------	--	-------------------	--	-------------------	--	-------------------	--	-------------------	--	----------------	--	-------------------	--	-------------------	--	-------------------	--	-------------------	--	-------------------	--	-------------------	--	----------------	--	-------------------	--	-------------------	--	-------------------	--	-------------------	--	-------------------	--	-------------------	--	----------------	--	-------------------	--	-------------------	--	-------------------	--	-------------------	--	-------------------	--	-------------------	--	----------------	--	-------------------	--	-------------------	--	-------------------	--	-------------------	--	-------------------	--	-------------------	--	----------------	--	-------------------	--	-------------------	--	-------------------	--	-------------------	--	-------------------	--	-------------------	--	----------------	--	-------------------	--	-------------------	--	-------------------	--	-------------------	--	-------------------	--	-------------------	--	----------------	--	-------------------	--	-------------------	--	-------------------	--	-------------------	--	-------------------	--	-------------------	--	----------------	--	-------------------	--	-------------------	--	-------------------	--	-------------------	--	-------------------	--	-------------------	--	----------------	--	-------------------	--	-------------------	--	-------------------	--	-------------------	--	-------------------	--	-------------------	--	----------------	--	-------------------	--	-------------------	--	-------------------	--	-------------------	--	-------------------	--	-------------------	--	----------------	--	-------------------	--	-------------------	--	-------------------	--	-------------------	--	-------------------	--	-------------------	--	----------------	--	-------------------	--	-------------------	--	-------------------	--	-------------------	--	-------------------	--	-------------------	--	----------------	--	-------------------	--	-------------------	--	-------------------	--	-------------------	--	-------------------	--	-------------------	--	----------------	--	-------------------	--	-------------------	--	-------------------	--	-------------------	--	-------------------	--	-------------------	--	----------------	--	-------------------	--	-------------------	--	-------------------	--	-------------------	--	-------------------	--	-------------------	--	----------------	--	-------------------	--	-------------------	--	-------------------	--	-------------------	--	-------------------	--	-------------------	--	----------------	--	-------------------	--	-------------------	--	-------------------	--	-------------------	--	-------------------	--	-------------------	--	----------------	--	-------------------	--	-------------------	--	-------------------	--	-------------------	--	-------------------	--	-------------------	--	----------------	--	-------------------	--	-------------------	--	-------------------	--	-------------------	--	-------------------	--	-------------------	--	----------------	--	-------------------	--	-------------------	--	-------------------	--	-------------------	--	-------------------	--	-------------------	--	----------------	--	-------------------	--	--	--

Имя, №, дата, Подпись и дата


План полов на отм. 0,000



Экспликация помещений

№ пом.	Наименование	Площадь, м²	Кат. пом.
Блок 1			
101	Танбур	2.02	
102	Коридор	6.62	
103	Кабинет	12.92	
104	Санузел	1.08	
105	Умывальная	1.17	
106	Пан. уборочного инвентаря	2.45	Б4
107	Кабинет	32.23	
108	Производственное помещение	626.82	Б4
Итого по блоку №1		685.31	
Блок 2			
101	Танбур	2.02	
102	Коридор	6.62	
103	Кабинет	11.35	
104	Санузел	1.08	
105	Умывальная	1.17	
106	Пан. уборочного инвентаря	1.85	Б4
107	Кабинет	32.23	
108	Производственное помещение	603.23	Б4
Итого по блоку №2		659.55	
Блок 3			
101	Танбур	2.02	
102	Коридор	6.62	
103	Кабинет	11.35	
104	Санузел	1.08	
105	Умывальная	1.17	
106	Пан. уборочного инвентаря	1.85	Б4
107	Кабинет	32.23	
108	Производственное помещение	603.23	Б4
Итого по блоку №3		659.55	
Блок 4			
101	Танбур	2.02	
102	Коридор	6.62	
103	Кабинет	11.35	
104	Санузел	1.08	
105	Умывальная	1.17	
106	Пан. уборочного инвентаря	1.85	Б4
107	Кабинет	32.23	
108	Производственное помещение	603.23	Б4
Итого по блоку №4		659.55	
Блок 5			
101	Танбур	2.02	
102	Коридор	6.62	
103	Кабинет	11.35	
104	Санузел	1.08	
105	Умывальная	1.17	
106	Пан. уборочного инвентаря	1.85	Б4
107	Кабинет	32.23	
108	Производственное помещение	603.23	Б4
Итого по блоку №5		659.55	
Блок 6			
101	Танбур	2.02	
102	Коридор	6.62	
103	Кабинет	12.92	
104	Санузел	1.08	
105	Умывальная	1.17	
106	Пан. уборочного инвентаря	2.45	Б4
107	Кабинет	32.23	
108	Производственное помещение	606.60	Б4
Итого по блоку №6		665.09	
Итого по этажу		3988.68	
Технические помещения			
109	ИТП, Водомерный узел	21.00	Д

Компоновочная схема

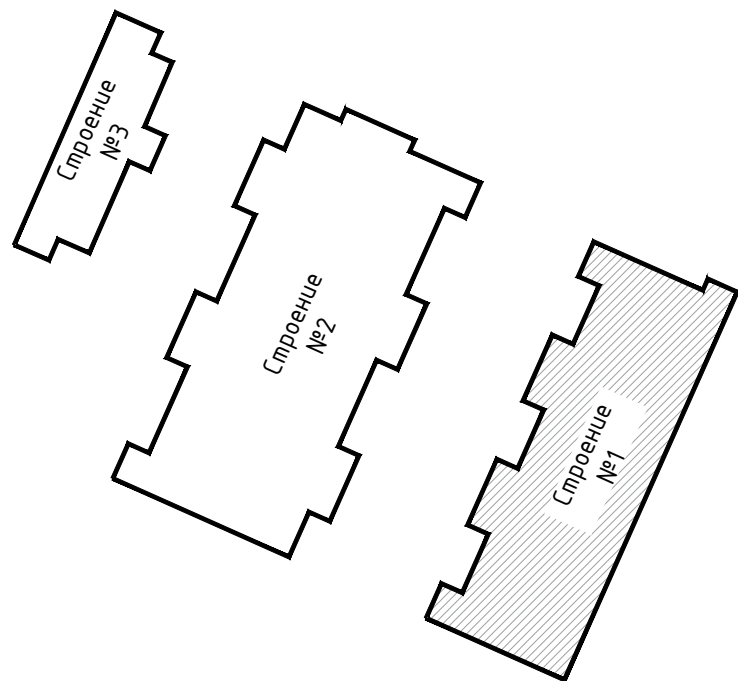

Условные обозначения

- Стекло из сэндвич-панелей - 120 мм
- Перегородка из сэндвич-панелей - 100 мм
- Перегородки из гипсокартонных листов ГКЛ 2000x1200x12.5 ГОСТ 6266-97 - 125 мм
- Перегородки из гипсокартонных листов ГКЛ 2000x1200x12.5 ГОСТ 6266-97 - 125 мм
- Перегородки из гипсокартонных влагостойких листов ГКЛВ 2000x1200x12.5 ГОСТ 6266-97 - 125 мм

Экспликация полов

Номер помещения	Тип пола	Схема пола или тип пола по сечению	Данные элементов пола, мм	Тип шпательной плиты
108	1		1 - Упрочняющее покрытие (эпоксидная смола) 2 - Ж.Б.плита (бетон B25, шпательный) - 180 мм 3 - Гипсокартон 602/12 4 - Цемент 20-40 5 - Гипсокартон СД-30 6 - Уплотненный грунт	3646.34
104, 105, 106	2		1 - Каркасная плита 2 - Плиточный клей 3 - Облицовочная гидроизоляция 2 сл. - 4 мм 4 - Ж.Б.плита (бетон B25, шпательный) - 180 мм 5 - Гипсокартон 602/12 6 - Цемент 20-40 7 - Гипсокартон СД-30 8 - Уплотненный грунт	25.80
101, 102	3		1 - Каркасная плита 2 - Плиточный клей 3 - Ж.Б.плита (бетон B25, шпательный) - 180 мм 4 - Гипсокартон 602/12 5 - Цемент 20-40 6 - Гипсокартон СД-30 7 - Уплотненный грунт	5184
103, 107	3 а		1 - Линолеум 2 - Подложка под ламинат - 8 мм 3 - Ж.Б.плита (бетон B25, шпательный) - 180 мм 4 - Гипсокартон 602/12 5 - Цемент 20-40 6 - Гипсокартон СД-30 7 - Уплотненный грунт	264.62
109	4		1 - Обесшумляющая краска 2 - Гидроизоляционный слой (ПЕНЕТРОН) 3 - Ж.Б.плита (бетон B25, шпательный) - 180 мм 4 - Гипсокартон 602/12 5 - Цемент 20-40 6 - Гипсокартон СД-30 7 - Уплотненный грунт	21.00


Имя	Колос	Лист	№	Дата
Разработчик	Чирков	04.18	04.18	
Проверщик	Чирков	04.18	04.18	
Ген. пр.	Абдулов	04.18	04.18	
Н. контр.	Абдулов	04.18	04.18	

01-ВЕН/18-СК13-АС1-С1
«Производственно-складской комплекс №13 «Industrial City», расположенный по адресу: Московская область, Городской округ Подольск, деревня Наболевки, территория Технопарк, 13а»

Сверение 1

План полов на отм. 0,000. Экспликация полов

0001-УС-КРЕДИТОПРОЕКТ

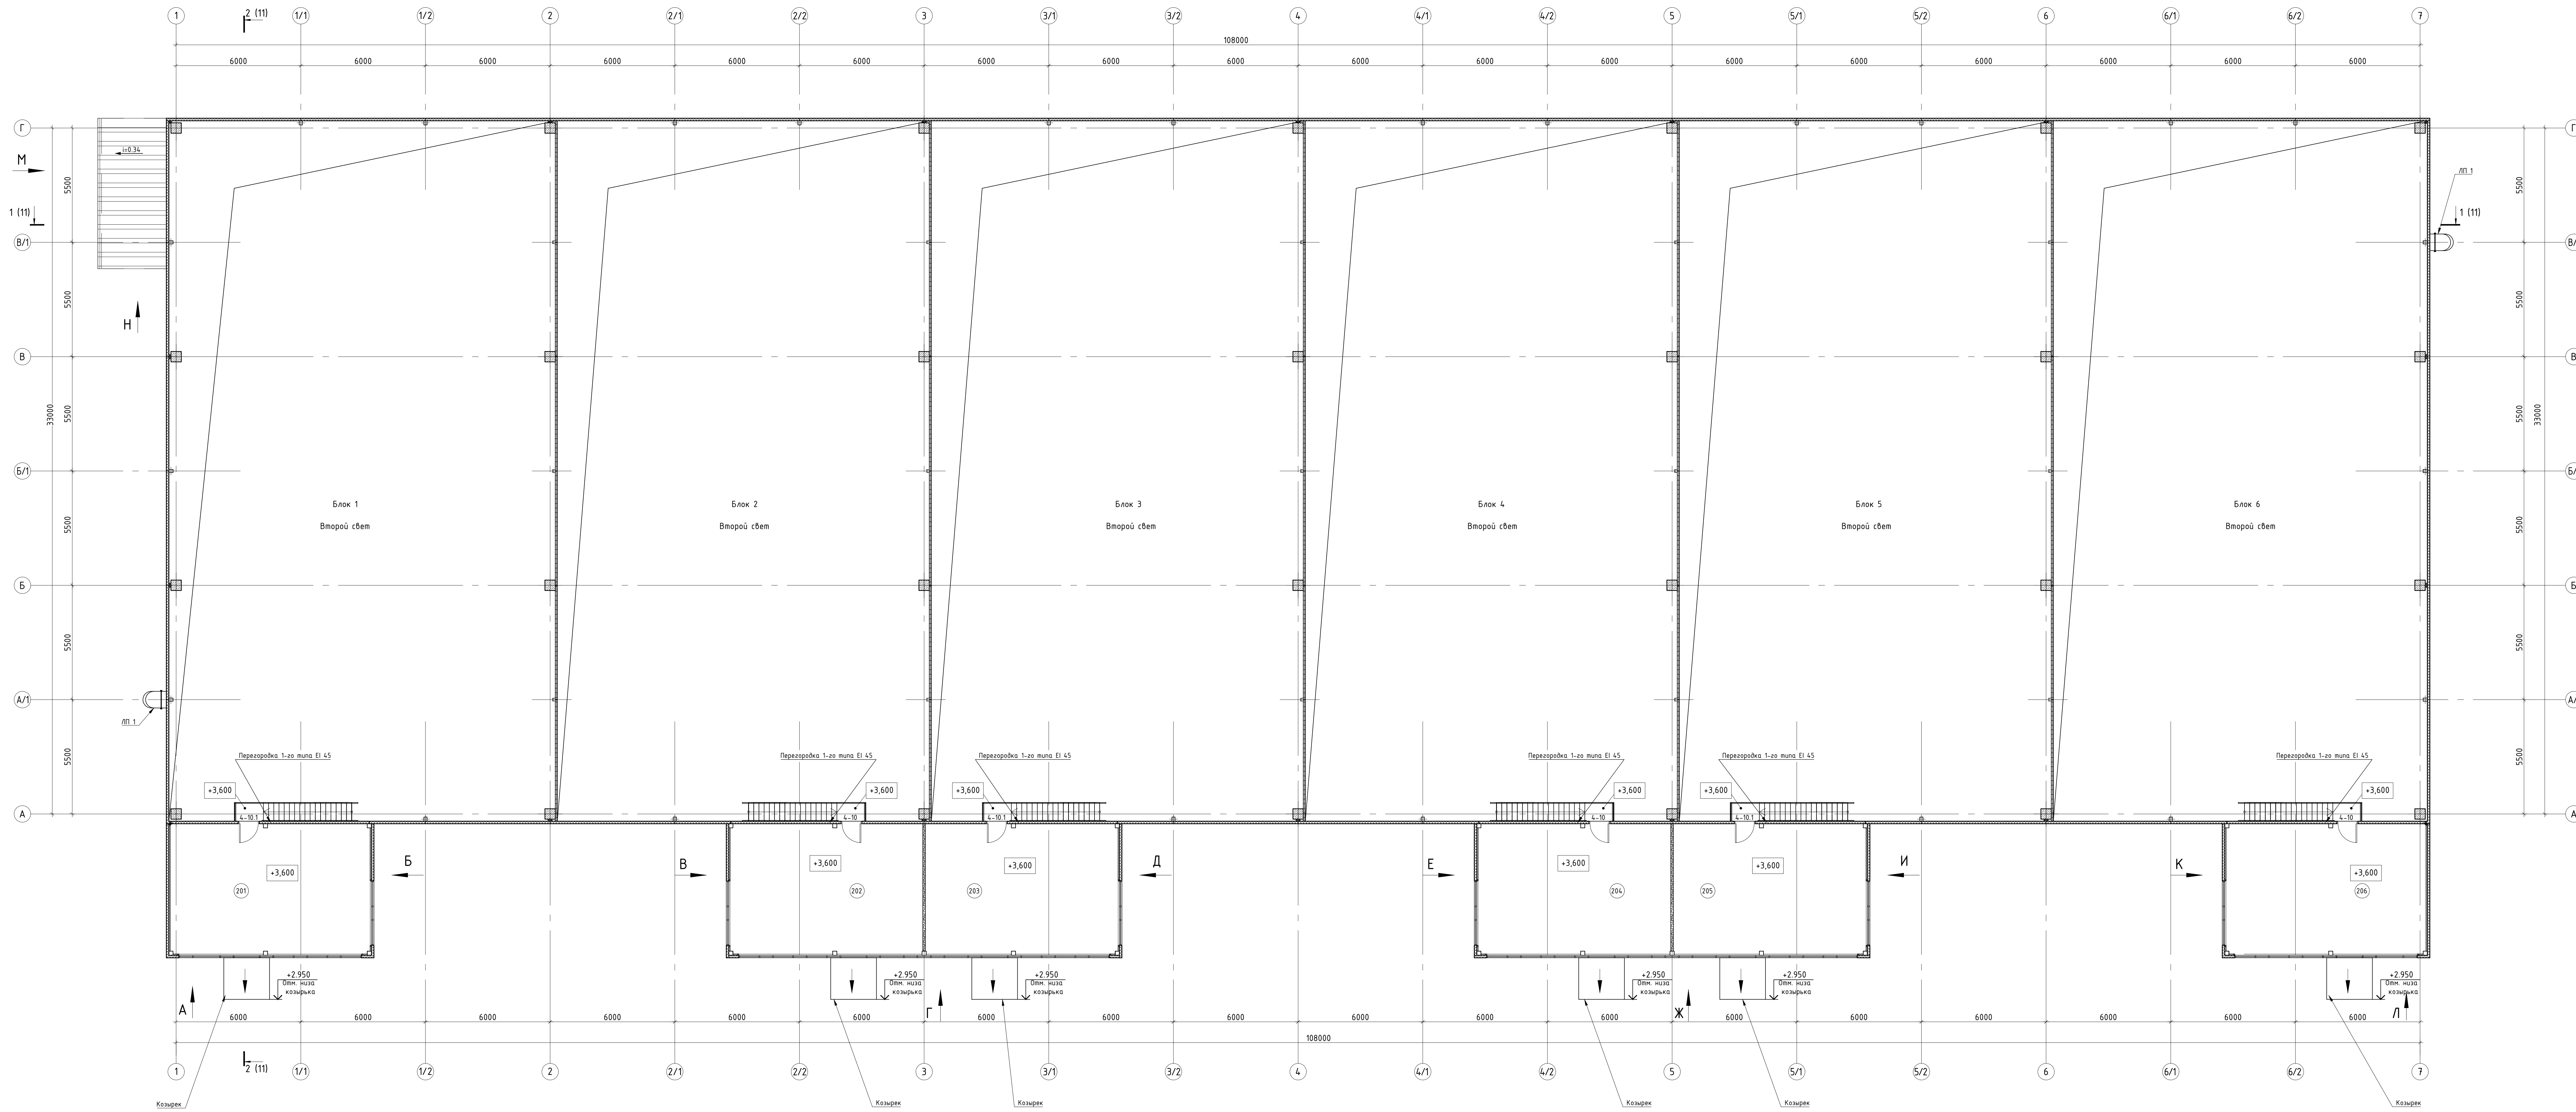

	Стено из сэндвич-панелей - 120 мм
	Перегородка из сэндвич-панелей - 100 мм
	Перегородки из гипсокартонных листов ГКЛ 2000х1200х12,5 ГОСТ 6266-97 - 125 мм
	Перегородки из гипсокартонных листов ГКЛ 2000х1200х12,5 ГОСТ 6266-97 - 125 мм
	Перегородки из гипсокартонных влагостойких листов ГКЛВ 2000х1200х12,5 ГОСТ 6266-97 - 125 мм

Структура обозначения Шерей:
3-10


 группа Шерейных изделий 3-й дм

1. Чертежи и спецификации дверных проемов см. в п. 19-25
2. Тип 3 (маркировки 3-10, 3-7 и п.п.) - внешние двери.
Тип 4 (марки 4-10) - внутренние противопожарные двери.
3. В пом. 101, 103, 107 (Блок 1-10) и 106 (Блок 5,5-6) наружные стены из сэндвич-панелей защитнокаркасные листами.
4. Отверстия в перекрытиях см. 01-ВЕН-18-СК13-КОС-С1
5. Отверстия в перегородках выполняются по месту после монтажа перегородок.

						01-ВЕН/18-СК13-АС1-С1					
						«Производственно-складской комплекс» №13 industrial (г.г.у), расположенный по адресу: Московская область, Горбовский округ Подольск, деревня Новоселки, территория «Технопарк, 13»					
ин.	Молж.	Лист	№'вок	Подпись	Дата	Страница 1			Страниц	Лист	Листов
разверн.		Акчина			04.18				P	8	
вернул		Черкашов			04.18						
ИП		Авдубов			04.18						
компр.		Авдубов			04.18	Схема заполнения данных приемов. План на отв. +3600			ООО"КУРСКОМПРОЕКТ"		

Имя, №, дата, Подпись и дата, Взам. инв. №


План полов на отм. +3.600

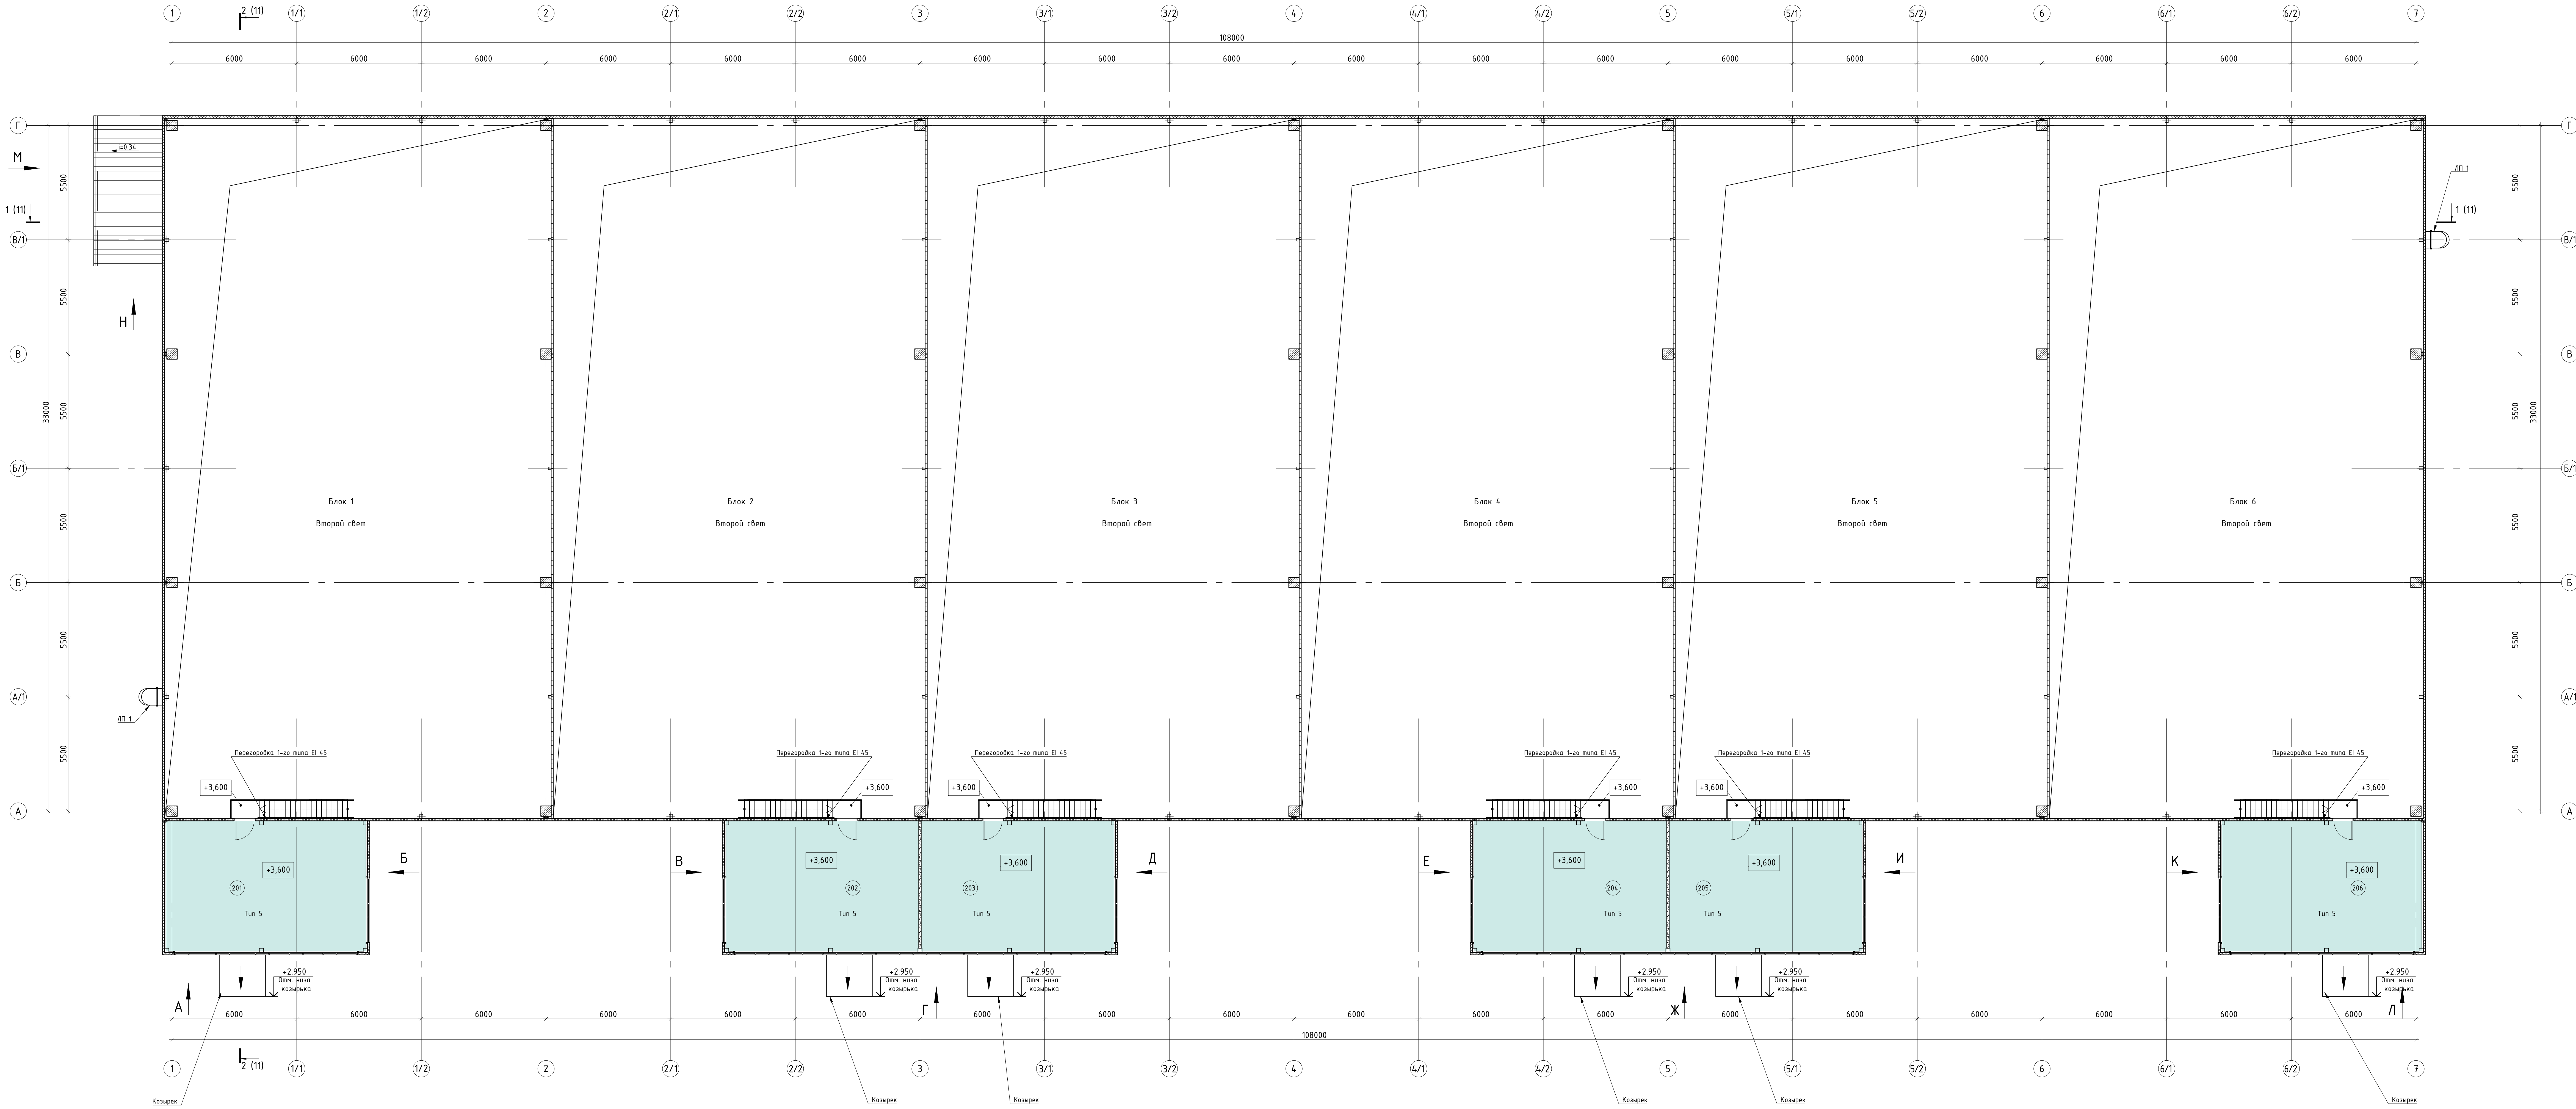

Экспликация помещений

№ пом.	Наименование	Площадь, м²	Кат. пом.
201	Подсобное помещение (сантрезервуар)	60,38	
202	Подсобное помещение (сантрезервуар)	58,19	
203	Подсобное помещение (сантрезервуар)	58,19	
204	Подсобное помещение (сантрезервуар)	58,19	
205	Подсобное помещение (сантрезервуар)	58,19	
206	Подсобное помещение (сантрезервуар)	60,38	
Итого по этажу		353,52	

Компоновочная схема

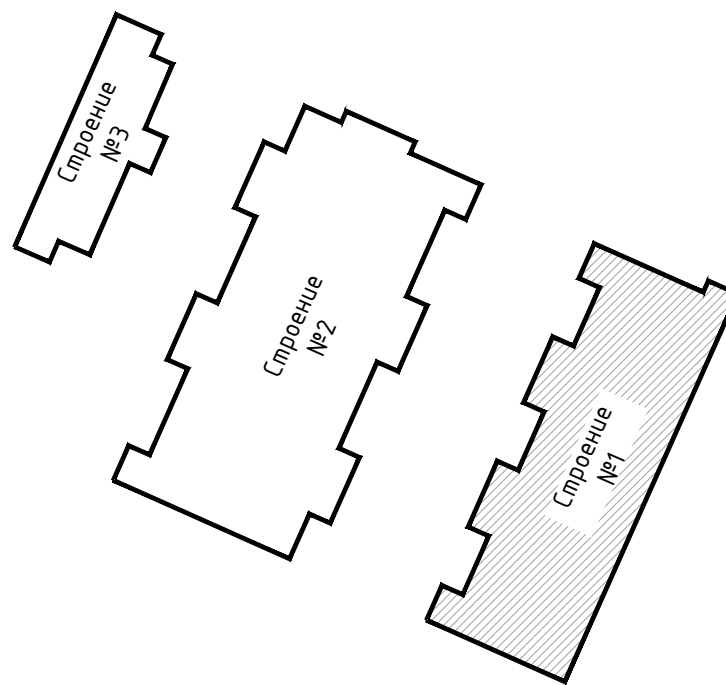

Условные обозначения

- Стена из сэндвич-панелей - 120 мм
- Перегорода из сэндвич-панелей - 100 мм
- Перегорода из гипсокартонных листов ГКЛ 2000x1200x12,5 ГОСТ 6266-97 - 125 мм
- Перегорода из гипсокартонных листов ГКЛ 2000x1200x12,5 ГОСТ 6266-97 - 125 мм
- Перегорода из гипсокартонных влагостойких листов ГКЛВ 2000x1200x12,5 ГОСТ 6266-97 - 125 мм

Экспликация полов


Номер помещения	Тип пола	Схема пола или тип пола по серии	Данные элементов пола, мм	Тип шпательной, мм
201-206	5		1 - Ламинат 2 - Подложка под ламинат 3 - Ж.Б.плита бетон В25, армированная по профилированному листу	-12 мм -8 мм -150мм

Примечания:


1. Отверстия в перегородках см. 01-ВЕН/18-СК13-КХ5-С1

				01-ВЕН/18-СК13-АС1-С1		
				«Производственно-складской комплекс №13 «Industrial City», расположенный по адресу: Московская область, городской округ Подольск, деревня Набокселки, территория Технопарк, 13а»		
Изм.	Кол.	Лист	№	Подпись	Дата	
Разработ.	Чертков	04.18	04.18			
Проверил	Черкасский	04.18	04.18			
ГИП	Абдуллин	04.18	04.18			
Н. контр.	Абдуллин	04.18	04.18			
				Спроектировано 1		
				Составил		
				Лист		
				Р		
				9		
				Листов		
				0001-УС-КРЕДИТ-ПРОЕКТ		

План кровли

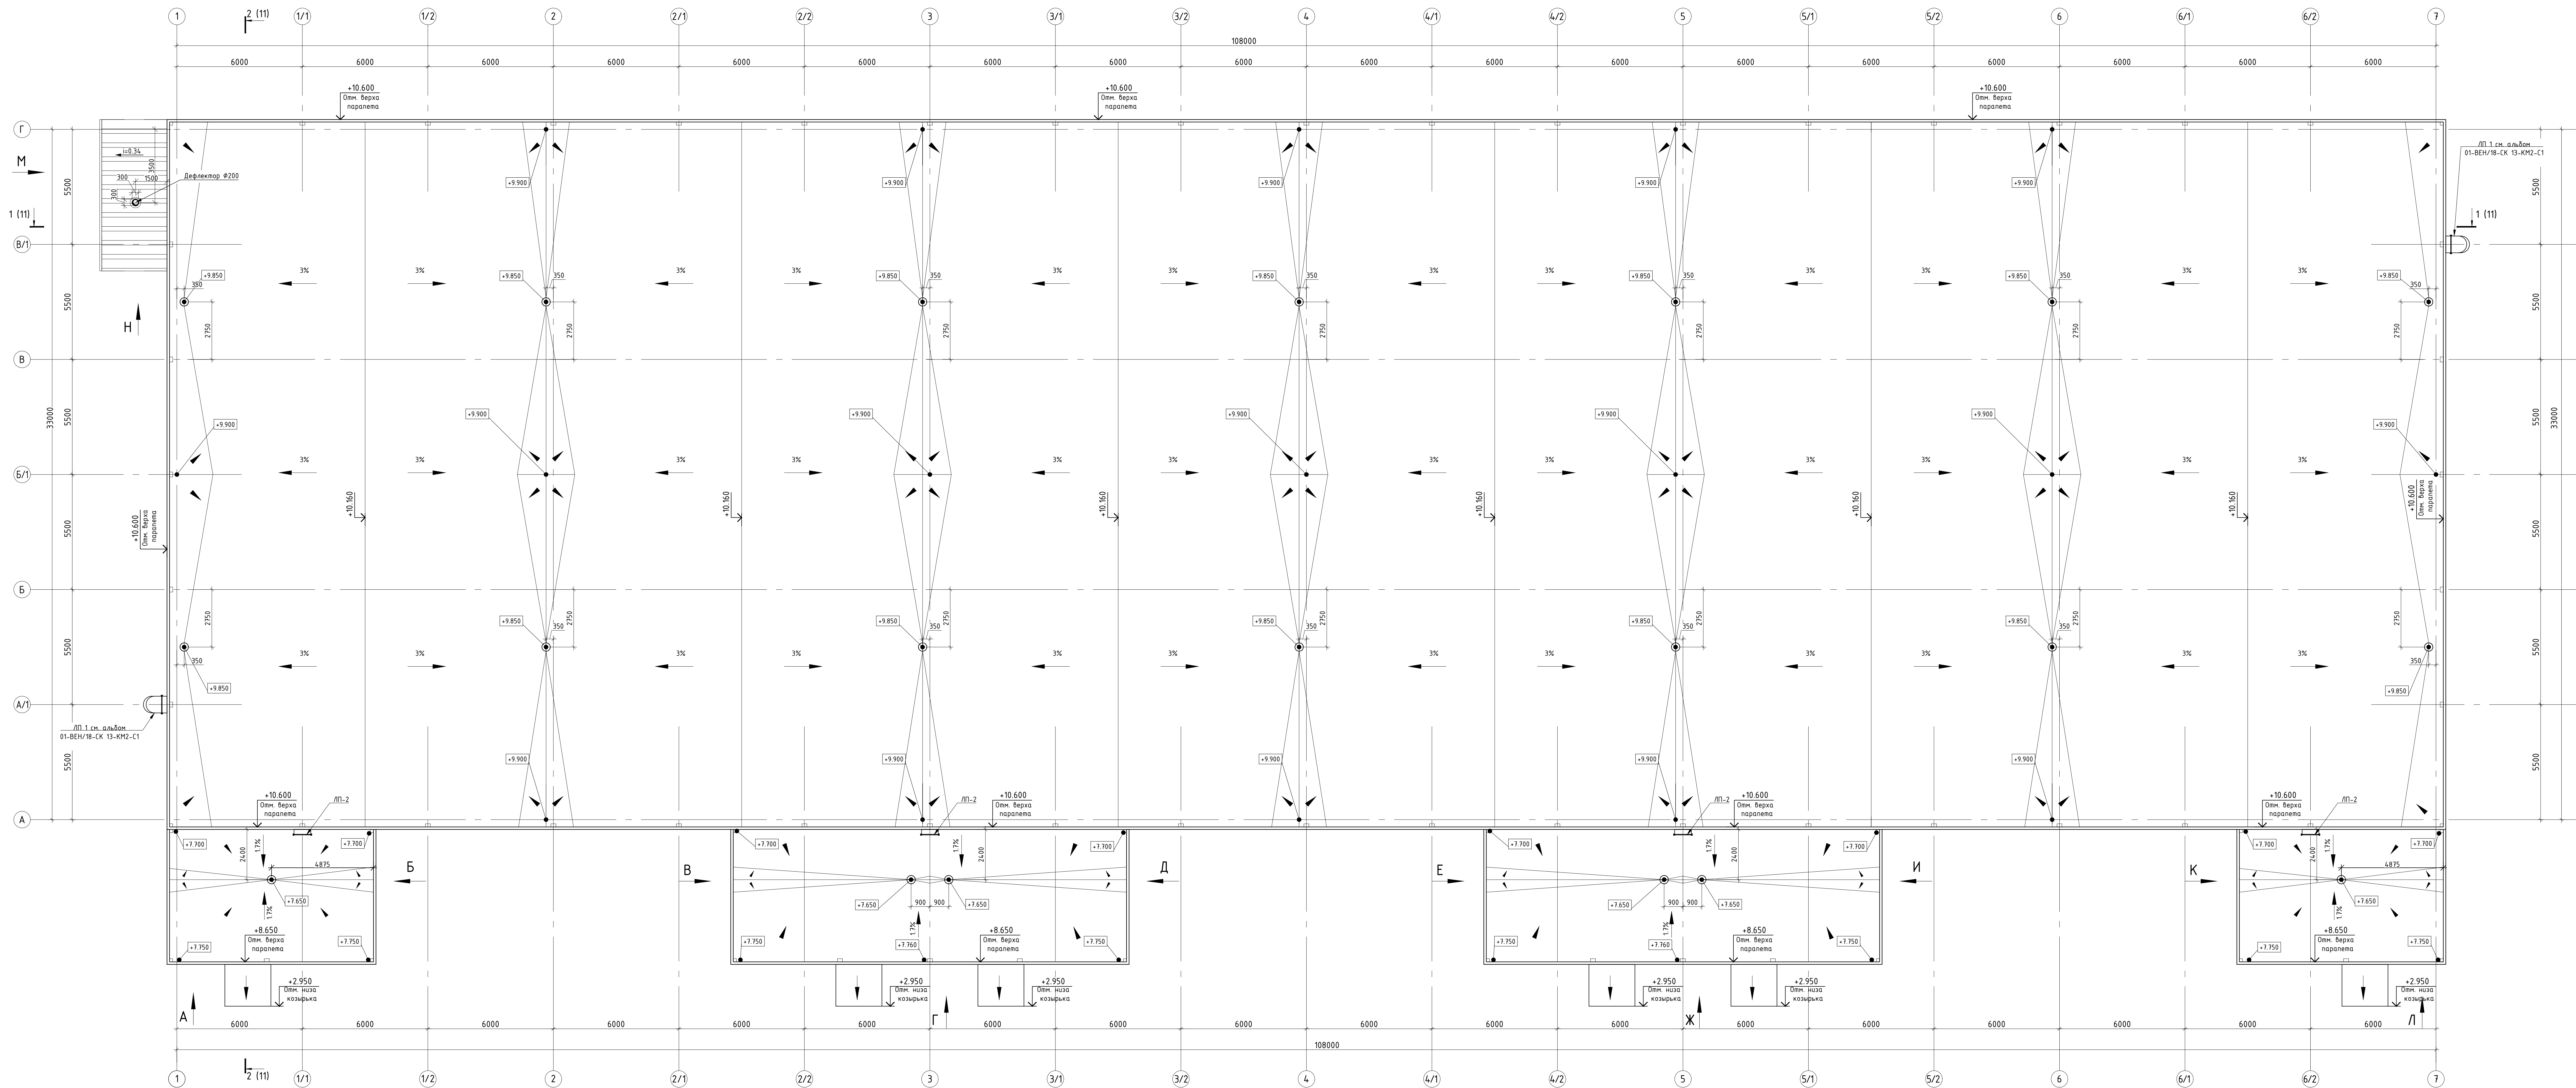

Компоновочная схема

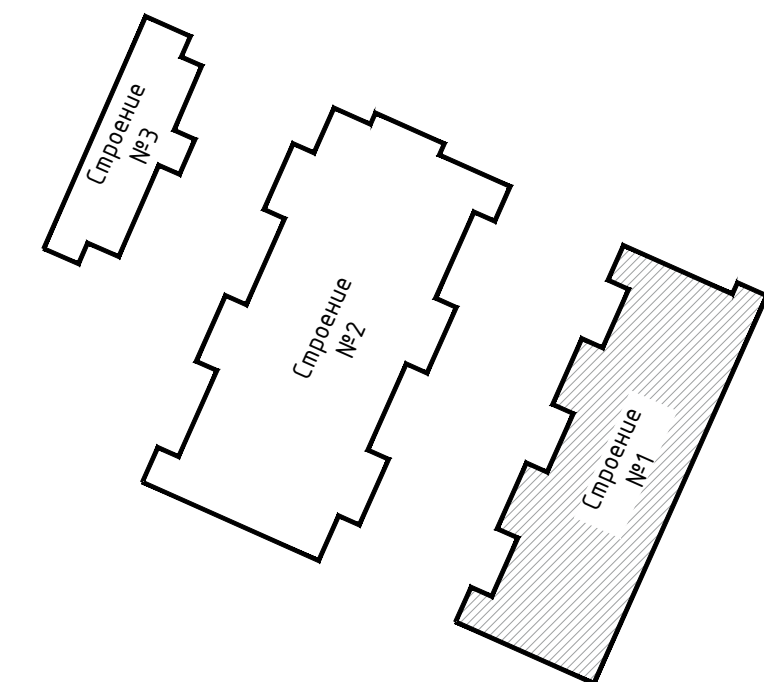[illegible]

Инф. № подл.

Подпись и дата

Взам. инф. №

Ведомость отделки помещений Блок 1

Наименование, № пом.	Вид отделки элементов интерьера								Примечание
	Пол	Площадь, м²	Потолок	Площадь, м²	Стены и перегородки	Площадь, м²	Цокольная панель	Площадь, м²	
Помещения на отм. 0.000									
Тамбур (пом.№101)	Керамограни тная плитка	2,02	Подвесной потолок – типа "Грильято"	2,02	Краска акриловая, обои под покраску, шпатлевка, грунтовка(стены из ГКЛ)	11.22	Краска акриловая, шпатлевка, грунтовка штукатурка, грунтовка	0.03	
					Краска акриловая, обои под покраску, шпатлевка, грунтовка (стены из сэндвич-панелей с внутренней стороны обшить листами ГКЛ по металлокаркасу)	0.71			
Коридор (№пом.102)	Керамограни тная плитка	6,62	Подвесной потолок – типа "Грильято"	6,62	Краска акриловая, обои под покраску, шпатлевка, грунтовка(стены из ГКЛ)	24.81	-	-	
					Краска акриловая, обои под покраску, шпатлевка, грунтовка (стены из сэндвич-панелей с внутренней стороны обшить листами ГКЛ по металлокаркасу)	1.98			
Кабинет (№пом.103)	Ламинат	12.92	Подвесной потолок – типа "Грильято"	12.92	Краска акриловая, обои под покраску, шпатлевка, грунтовка(стены из ГКЛ)	20.34	Краска акриловая, шпатлевка, грунтовка штукатурка, грунтовка	2.21	
					Краска акриловая, обои под покраску, шпатлевка, грунтовка (стены из сэндвич-панелей с внутренней стороны обшить листами ГКЛ по металлокаркасу)	19.35			

Ведомость отделки помещений Блок 1

Наименование, № пом.	Вид отделки элементов интерьера								Примечание
	Пол	Площадь, м²	Потолок	Площадь, м²	Стены и перегородки	Площадь, м²	Цокольная панель	Площадь, м²	
Помещения на отм. 0.000									
Санузел (№пом.104)	Керамическая плитка	1,08	Потолок реечного типа	1,08	Плитка керамическая на клею, грунтовка (стены из ГКЛВ)	9.09	-	-	
Умывальная (№пом.105)	Керамическая плитка	1,17	Потолок реечного типа	1,17	Плитка керамическая на клею, грунтовка (стены из ГКЛВ)	3.72	-	-	
					Плитка керамическая на клею, грунтовка (стены из сэндвич-панелей с внутренней стороны обшить листами ГКЛ по металлокаркасу)	4.16			
Пом. уборочного инвентаря (№пом.106)	Керамическая плитка	2.45	Потолок реечного типа	2.45	Плитка керамическая на клею, грунтовка (стены из ГКЛВ)	9.67	-	-	
					Плитка керамическая на клею, грунтовка (стены из сэндвич-панелей с внутренней стороны обшить листами ГКЛ по металлокаркасу)	8.03			
Кабинет (№пом.107)	Ламинат	32,23	Подвесной потолок – типа “Грильято”	32,23	Краска акриловая, обои под покраску, шпатлевка, грунтовка (стены из ГКЛ)	17.16	Краска акриловая, шпатлевка, грунтовка штукатурка, грунтовка	3.42	
					Краска акриловая, обои под покраску, шпатлевка, грунтовка (стены из сэндвич-панелей с внутренней стороны обшить листами ГКЛ по металлокаркасу)	38.81			
Производственное помещение (пом.№108)	Упрочняющее покрытие Dugosog	626.82							

Ведомость отделки помещений Блок 1

Наименование, № пом.	Вид отделки элементов интерьера								Примечание
	Пол	Площадь, м²	Потолок	Площадь, м²	Стены и перегородки	Площадь, м²	Цокольная панель	Площадь, м²	
Помещения на отм. +3.600									
Подсобное помещение (антресоль) (пом.№201)	Ламинат	60,38	Подвесной потолок – типа “Грильято”	14.74	Краска акриловая, обои под покраску, шпатлевка, грунтовка (стены из сэндвич-панелей с внутренней стороны обшить листами ГКЛ по металлокаркасу)	100.87	-	-	

							01-ВЕН/18-СК13-АС1-С1				
							«Производственно-складской комплекс №13 «Industrial City», расположенный по адресу: Московская область, Городской округ Подольск, деревня Новоселки, территория Технопарка, 13»				
Изм.	Кол.уч.	Лист	№док	Подпись	Дата	Строение 1			Стадия	Лист	Листов
Разраб.	Якунина				04.18				P	12	
Проверил	Черкасов				04.18	Ведомость отделки помещений Блок 1			ООО"КУРСКРЕГИОНПРОЕКТ"		
ГИП	Абдулов				04.18						
Н. контр.	Абдулов				04.18						

Инф. № подл.

Подпись и дата

Взам. инф. №

Ведомость отделки помещений Блок 2									
Наименование, № пом.	Вид отделки элементов интерьера								Примечание
	Пол	Площадь, м²	Потолок	Площадь, м²	Стены и перегородки	Площадь, м²	Цокольная панель	Площадь, м²	
Помещения на отм. 0.000									
Тамбур (пом.№101)	Керамограни тная плитка	2,02	Подвесной потолок – типа “Грильято”	2,02	Краска акриловая, обои под покраску, шпатлевка, грунтовка(стены из ГКЛ)	11.22	Краска акриловая, шпатлевка, грунтовка штукатурка, грунтовка	0.03	
					Краска акриловая, обои под покраску, шпатлевка, грунтовка (стены из сэндвич-панелей с внутренней стороны обшить листами ГКЛ по металлокаркасу)	0.71			
Коридор (№пом.102)	Керамограни тная плитка	6,62	Подвесной потолок – типа “Грильято”	6,62	Краска акриловая, обои под покраску, шпатлевка, грунтовка(стены из ГКЛ)	24.81	-	-	
					Краска акриловая, обои под покраску, шпатлевка, грунтовка (стены из сэндвич-панелей с внутренней стороны обшить листами ГКЛ по металлокаркасу)	1.98			
Кабинет (№пом.103)	Ламинат	11.35	Подвесной потолок – типа “Грильято”	11.35	Краска акриловая, обои под покраску, шпатлевка, грунтовка(стены из ГКЛ)	33.39	Краска акриловая, шпатлевка, грунтовка штукатурка, грунтовка	2.21	
					Краска акриловая, обои под покраску, шпатлевка, грунтовка (стены из сэндвич-панелей с внутренней стороны обшить листами ГКЛ по металлокаркасу)	4.48			

Ведомость отделки помещений Блок 2									
Наименование, № пом.	Вид отделки элементов интерьера								Примечание
	Пол	Площадь, м²	Потолок	Площадь, м²	Стены и перегородки	Площадь, м²	Цокольная панель	Площадь, м²	
Помещения на отм. +3.600									
Подсобное помещение (антресоль) (пом.№202)	Ламинат	58.19	Подвесной потолок – типа “Грильято”	14.74	Краска акриловая, обои под покраску, шпатлевка, грунтовка(стены из ГКЛ)	20.69	-	-	
					Краска акриловая, обои под покраску, шпатлевка, грунтовка (стены из сэндвич-панелей с внутренней стороны обшить листами ГКЛ по металлокаркасу)	62			

Ведомость отделки помещений Блок 2									
Наименование, № пом.	Вид отделки элементов интерьера								Примечание
	Пол	Площадь, м²	Потолок	Площадь, м²	Стены и перегородки	Площадь, м²	Цокольная панель	Площадь, м²	
Помещения на отм. 0.000									
Санузел (№пом.104)	Керамическая плитка	1,08	Потолок реечного типа	1,08	Плитка керамическая на клею, грунтовка (стены из ГКЛВ)	9.09	-	-	
Умывальная (№пом.105)	Керамическая плитка	1,17	Потолок реечного типа	1,17	Плитка керамическая на клею, грунтовка (стены из ГКЛВ)	3.72	-	-	
					Плитка керамическая на клею, грунтовка (стены из сэндвич-панелей с внутренней стороны обшить листами ГКЛ по металлокаркасу)	4.16			
Пом. уборочного инвентаря (№пом.106)	Керамическая плитка	1,85	Потолок реечного типа	1,85	Плитка керамическая на клею, грунтовка (стены из ГКЛВ)	14	-	-	
					Плитка керамическая на клею, грунтовка (стены из сэндвич-панелей с внутренней стороны обшить листами ГКЛ по металлокаркасу)	1.44			
Кабинет (№пом.107)	Ламинат	32,23	Подвесной потолок – типа "Грильято"	32,23	Краска акриловая, обои под покраску, шпатлевка, грунтовка (стены из ГКЛ)	17.16	Краска акриловая, шпатлевка, грунтовка штукатурка, грунтовка	3.42	
					Краска акриловая, обои под покраску, шпатлевка, грунтовка (стены из сэндвич-панелей с внутренней стороны обшить листами ГКЛ по металлокаркасу)	38.81			
Производственное помещение (пом.№108)	Упрочняющее покрытие Dugosog	603.23							

							01-ВЕН/18-СК13-АС1-С1			
							«Производственно-складской комплекс №13 «Industrial City», расположенный по адресу: Московская область, Городской округ Подольск, деревня Новоселки, территория Технопарка, 13»			
Изм.	Кол.уч.	Лист	№ док	Подпись	Дата	Строение 1		Стадия	Лист	Листов
Разраб.	Якунина				04.18			Р	13	
Проверил	Черкасов				04.18	Ведомость отделки помещений Блок 2		ООО "КУРСКРЕГИОНПРОЕКТ"		
ГИП	Абдулов				04.18					
Н. контр.	Абдулов				04.18					

Инф. № подл.

Подпись и дата

Взам. инф. №

Ведомость отделки помещений Блок 3									
Наименование, № пом.	Вид отделки элементов интерьера								Примечание
	Пол	Площадь, м²	Потолок	Площадь, м²	Стены и перегородки	Площадь, м²	Цокольная панель	Площадь, м²	
Помещения на отм. 0.000									
Тамбур (пом.№101)	Керамограни тная плитка	2,02	Подвесной потолок – типа “Грильято”	2,02	Краска акриловая, обои под покраску, шпатлевка, грунтовка(стены из ГКЛ)	11.22	Краска акриловая, шпатлевка, грунтовка штукатурка, грунтовка	0.03	
					Краска акриловая, обои под покраску, шпатлевка, грунтовка (стены из сэндвич-панелей с внутренней стороны обшить листами ГКЛ по металлокаркасу)	0.71			
Коридор (№пом.102)	Керамограни тная плитка	6,62	Подвесной потолок – типа “Грильято”	6,62	Краска акриловая, обои под покраску, шпатлевка, грунтовка(стены из ГКЛ)	24.81	-	-	
					Краска акриловая, обои под покраску, шпатлевка, грунтовка (стены из сэндвич-панелей с внутренней стороны обшить листами ГКЛ по металлокаркасу)	1.98			
Кабинет (№пом.103)	Ламинат	11.35	Подвесной потолок – типа “Грильято”	11.35	Краска акриловая, обои под покраску, шпатлевка, грунтовка(стены из ГКЛ)	33.39	Краска акриловая, шпатлевка, грунтовка штукатурка, грунтовка	2.21	
					Краска акриловая, обои под покраску, шпатлевка, грунтовка (стены из сэндвич-панелей с внутренней стороны обшить листами ГКЛ по металлокаркасу)	4.48			

Ведомость отделки помещений Блок 3									
Наименование, № пом.	Вид отделки элементов интерьера								Примечание
	Пол	Площадь, м²	Потолок	Площадь, м²	Стены и перегородки	Площадь, м²	Цокольная панель	Площадь, м²	
Помещения на отм. +3.600									
Подсобное помещение (антресоль) (пом.№203)	Ламинат	58.19	Подвесной потолок – типа “Грильято”	14.74	Краска акриловая, обои под покраску, шпатлевка, грунтовка(стены из ГКЛ)	20.69	-	-	
					Краска акриловая, обои под покраску, шпатлевка, грунтовка (стены из сэндвич-панелей с внутренней стороны обшить листами ГКЛ по металлокаркасу)	62			

Ведомость отделки помещений Блок 3									
Наименование, № пом.	Вид отделки элементов интерьера								Примечание
	Пол	Площадь, м²	Потолок	Площадь, м²	Стены и перегородки	Площадь, м²	Цокольная панель	Площадь, м²	
Помещения на отм. 0.000									
Санузел (№пом.104)	Керамическая плитка	1,08	Потолок реечного типа	1,08	Плитка керамическая на клею, грунтовка (стены из ГКЛВ)	9.09	-	-	
Умывальная (№пом.105)	Керамическая плитка	1,17	Потолок реечного типа	1,17	Плитка керамическая на клею, грунтовка (стены из ГКЛВ)	3.72	-	-	
					Плитка керамическая на клею, грунтовка (стены из сэндвич-панелей с внутренней стороны обшить листами ГКЛ по металлокаркасу)	4.16			
Пом. уборочного инвентаря (№пом.106)	Керамическая плитка	1,85	Потолок реечного типа	1,85	Плитка керамическая на клею, грунтовка (стены из ГКЛВ)	14	-	-	
					Плитка керамическая на клею, грунтовка (стены из сэндвич-панелей с внутренней стороны обшить листами ГКЛ по металлокаркасу)	1.44			
Кабинет (№пом.107)	Ламинат	32,23	Подвесной потолок – типа "Грильято"	32,23	Краска акриловая, обои под покраску, шпатлевка, грунтовка (стены из ГКЛ)	17.16	Краска акриловая, шпатлевка, грунтовка штукатурка, грунтовка	3.42	
					Краска акриловая, обои под покраску, шпатлевка, грунтовка (стены из сэндвич-панелей с внутренней стороны обшить листами ГКЛ по металлокаркасу)	38.81			
Производственное помещение (пом.№108)	Упрочняющее покрытие Dugosog	603.23							

							01-ВЕН/18-СК13-АС1-С1			
							«Производственно-складской комплекс №13 «Industrial City», расположенный по адресу: Московская область, Городской округ Подольск, деревня Новоселки, территория Технопарка, 13»			
Изм.	Кол.уч.	Лист	№ док	Подпись	Дата	Строение 1		Стадия	Лист	Листов
Разраб.	Якунина				04.18			Р	14	
Проверил	Черкасов				04.18	Ведомость отделки помещений Блок 3		ООО "КУРСКРЕГИОНПРОЕКТ"		
ГИП	Абдулов				04.18					
Н. контр.	Абдулов				04.18					

Инф. № подл.

Подпись и дата

Взам. инф. №

Ведомость отделки помещений Блок 4									
Наименование, № пом.	Вид отделки элементов интерьера								Примечание
	Пол	Площадь, м²	Потолок	Площадь, м²	Стены и перегородки	Площадь, м²	Цокольная панель	Площадь, м²	
Помещения на отм. 0.000									
Тамбур (пом.№101)	Керамограни тная плитка	2,02	Подвесной потолок – типа “Грильято”	2,02	Краска акриловая, обои под покраску, шпатлевка, грунтовка(стены из ГКЛ)	11.22	Краска акриловая, шпатлевка, грунтовка штукатурка, грунтовка	0.03	
					Краска акриловая, обои под покраску, шпатлевка, грунтовка (стены из сэндвич-панелей с внутренней стороны обшить листами ГКЛ по металлокаркасу)	0.71			
Коридор (№пом.102)	Керамограни тная плитка	6,62	Подвесной потолок – типа “Грильято”	6,62	Краска акриловая, обои под покраску, шпатлевка, грунтовка(стены из ГКЛ)	24.81	-	-	
					Краска акриловая, обои под покраску, шпатлевка, грунтовка (стены из сэндвич-панелей с внутренней стороны обшить листами ГКЛ по металлокаркасу)	1.98			
Кабинет (№пом.103)	Ламинат	11.35	Подвесной потолок – типа “Грильято”	11.35	Краска акриловая, обои под покраску, шпатлевка, грунтовка(стены из ГКЛ)	33.39	Краска акриловая, шпатлевка, грунтовка штукатурка, грунтовка	2.21	
					Краска акриловая, обои под покраску, шпатлевка, грунтовка (стены из сэндвич-панелей с внутренней стороны обшить листами ГКЛ по металлокаркасу)	4.48			

Ведомость отделки помещений Блок 4									
Наименование, № пом.	Вид отделки элементов интерьера								Примечание
	Пол	Площадь, м²	Потолок	Площадь, м²	Стены и перегородки	Площадь, м²	Цокольная панель	Площадь, м²	
Помещения на отм. +3.600									
Подсобное помещение (антресоль) (пом.№204)	Ламинат	58.19	Подвесной потолок – типа “Грильято”	14.74	Краска акриловая, обои под покраску, шпатлевка, грунтовка(стены из ГКЛ)	20.69	-	-	
					Краска акриловая, обои под покраску, шпатлевка, грунтовка (стены из сэндвич-панелей с внутренней стороны обшить листами ГКЛ по металлокаркасу)	62			

Ведомость отделки помещений Блок 4									
Наименование, № пом.	Вид отделки элементов интерьера								Примечание
	Пол	Площадь, м²	Потолок	Площадь, м²	Стены и перегородки	Площадь, м²	Цокольная панель	Площадь, м²	
Помещения на отм. 0.000									
Санузел (№пом.104)	Керамическая плитка	1,08	Потолок реечного типа	1,08	Плитка керамическая на клею, грунтовка (стены из ГКЛ/В)	9.09	-	-	
Умывальная (№пом.105)	Керамическая плитка	1,17	Потолок реечного типа	1,17	Плитка керамическая на клею, грунтовка (стены из ГКЛ/В)	3.72	-	-	
					Плитка керамическая на клею, грунтовка (стены из сэндвич-панелей с внутренней стороны обшить листами ГКЛ по металлокаркасу)	4.16			
Пом. уборочного инвентаря (№пом.106)	Керамическая плитка	1,85	Потолок реечного типа	1,85	Плитка керамическая на клею, грунтовка (стены из ГКЛ/В)	14	-	-	
					Плитка керамическая на клею, грунтовка (стены из сэндвич-панелей с внутренней стороны обшить листами ГКЛ по металлокаркасу)	1.44			
Кабинет (№пом.107)	Ламинат	32,23	Подвесной потолок – типа "Грильято"	32,23	Краска акриловая, обои под покраску, шпатлевка, грунтовка (стены из ГКЛ)	17.16	Краска акриловая, шпатлевка, грунтовка штукатурка, грунтовка	3.42	
					Краска акриловая, обои под покраску, шпатлевка, грунтовка (стены из сэндвич-панелей с внутренней стороны обшить листами ГКЛ по металлокаркасу)	38.81			
Производственное помещение (пом.№108)	Упрочняющее покрытие Dugosog	603.23							

							01-ВЕН/18-СК13-АС1-С1			
							«Производственно-складской комплекс №13 «Industrial City», расположенный по адресу: Московская область, Городской округ Подольск, деревня Новоселки, территория Технопарка, 13»			
Изм.	Кол.уч.	Лист	№ док	Подпись	Дата	Строение 1		Стадия	Лист	Листов
Разраб.	Якунина				04.18			Р	15	
Проверил	Черкасов				04.18	Ведомость отделки помещений Блок 4		ООО "КУРСКРЕГИОНПРОЕКТ"		
ГИП	Абдулов				04.18					
Н. контр.	Абдулов				04.18					

Инф. № подл.

Подпись и дата

Взам. инф. №

Ведомость отделки помещений Блок 5									
Наименование, № пом.	Вид отделки элементов интерьера								Примечание
	Пол	Площадь, м²	Потолок	Площадь, м²	Стены и перегородки	Площадь, м²	Цокольная панель	Площадь, м²	
Помещения на отм. 0.000									
Тамбур (пом.№101)	Керамограни тная плитка	2,02	Подвесной потолок – типа “Грильято”	2,02	Краска акриловая, обои под покраску, шпатлевка, грунтовка(стены из ГКЛ)	11.22	Краска акриловая, шпатлевка, грунтовка штукатурка, грунтовка	0.03	
					Краска акриловая, обои под покраску, шпатлевка, грунтовка (стены из сэндвич–панелей с внутренней стороны обшить листами ГКЛ по металлокаркасу)	0.71			
Коридор (№пом.102)	Керамограни тная плитка	6,62	Подвесной потолок – типа “Грильято”	6,62	Краска акриловая, обои под покраску, шпатлевка, грунтовка(стены из ГКЛ)	24.81	-	-	
					Краска акриловая, обои под покраску, шпатлевка, грунтовка (стены из сэндвич–панелей с внутренней стороны обшить листами ГКЛ по металлокаркасу)	1.98			
Кабинет (№пом.103)	Ламинат	11.35	Подвесной потолок – типа “Грильято”	11.35	Краска акриловая, обои под покраску, шпатлевка, грунтовка(стены из ГКЛ)	33.39	Краска акриловая, шпатлевка, грунтовка штукатурка, грунтовка	2.21	
					Краска акриловая, обои под покраску, шпатлевка, грунтовка (стены из сэндвич–панелей с внутренней стороны обшить листами ГКЛ по металлокаркасу)	4.48			

Ведомость отделки помещений Блок 5									
Наименование, № пом.	Вид отделки элементов интерьера								Примечание
	Пол	Площадь, м²	Потолок	Площадь, м²	Стены и перегородки	Площадь, м²	Цокольная панель	Площадь, м²	
Помещения на отм. +3.600									
Подсобное помещение (антресоль) (пом.№205)	Ламинат	58.19	Подвесной потолок – типа “Грильято”	14.74	Краска акриловая, обои под покраску, шпатлевка, грунтовка(стены из ГКЛ)	20.69	-	-	
					Краска акриловая, обои под покраску, шпатлевка, грунтовка (стены из сэндвич-панелей с внутренней стороны обшить листами ГКЛ по металлокаркасу)	62			

Ведомость отделки помещений Блок 5									
Наименование, № пом.	Вид отделки элементов интерьера								Примечание
	Пол	Площадь, м²	Потолок	Площадь, м²	Стены и перегородки	Площадь, м²	Цокольная панель	Площадь, м²	
Помещения на отм. 0.000									
Санузел (№пом.104)	Керамическая плитка	1,08	Потолок реечного типа	1,08	Плитка керамическая на клею, грунтовка (стены из ГКЛВ)	9.09	-	-	
Умывальная (№пом.105)	Керамическая плитка	1,17	Потолок реечного типа	1,17	Плитка керамическая на клею, грунтовка (стены из ГКЛВ)	3.72	-	-	
					Плитка керамическая на клею, грунтовка (стены из сэндвич-панелей с внутренней стороны обшить листами ГКЛ по металлокаркасу)	4.16			
Пом. уборочного инвентаря (№пом.106)	Керамическая плитка	1,85	Потолок реечного типа	1,85	Плитка керамическая на клею, грунтовка (стены из ГКЛВ)	14	-	-	
					Плитка керамическая на клею, грунтовка (стены из сэндвич-панелей с внутренней стороны обшить листами ГКЛ по металлокаркасу)	1.44			
Кабинет (№пом.107)	Ламинат	32,23	Подвесной потолок – типа “Грильято”	32,23	Краска акриловая, обои под покраску, шпатлевка, грунтовка (стены из ГКЛ)	17.16	Краска акриловая, шпатлевка, грунтовка штукатурка, грунтовка	3.42	
					Краска акриловая, обои под покраску, шпатлевка, грунтовка (стены из сэндвич-панелей с внутренней стороны обшить листами ГКЛ по металлокаркасу)	38.81			
Производственное помещение (пом.№108)	Упрочняющее покрытие Dugosog	603.23							

							01-ВЕН/18-СК13-АС1-С1			
							«Производственно-складской комплекс №13 «Industrial City», расположенный по адресу: Московская область, Городской округ Подольск, деревня Новоселки, территория Технопарка, 13»			
Изм.	Кол.уч.	Лист	№ док	Подпись	Дата	Строение 1		Стадия	Лист	Листов
Разраб.	Якунина				04.18			Р	16	
Проверил	Черкасов				04.18	Ведомость отделки помещений Блок 5		ООО "КУРСКРЕГИОНПРОЕКТ"		
ГИП	Абдулов				04.18					
Н. контр.	Абдулов				04.18					

Инф. № подл.

Подпись и дата

Взам. инф. №

Ведомость отделки помещений Блок 6									
Наименование, № пом.	Вид отделки элементов интерьера								Примечание
	Пол	Площадь, м²	Потолок	Площадь, м²	Стены и перегородки	Площадь, м²	Цокольная панель	Площадь, м²	
Помещения на отм. 0.000									
Тамбур (пом.№101)	Керамограни тная плитка	2,02	Подвесной потолок – типа “Грильято”	2,02	Краска акриловая, обои под покраску, шпатлевка, грунтовка(стены из ГКЛ)	11.22	Краска акриловая, шпатлевка, грунтовка штукатурка, грунтовка	0.03	
					Краска акриловая, обои под покраску, шпатлевка, грунтовка (стены из сэндвич-панелей с внутренней стороны обшить листами ГКЛ по металлокаркасу)	0.71			
Коридор (№пом.102)	Керамограни тная плитка	6,62	Подвесной потолок – типа “Грильято”	6,62	Краска акриловая, обои под покраску, шпатлевка, грунтовка(стены из ГКЛ)	24.81	-	-	
					Краска акриловая, обои под покраску, шпатлевка, грунтовка (стены из сэндвич-панелей с внутренней стороны обшить листами ГКЛ по металлокаркасу)	1.98			
Кабинет (№пом.103)	Ламинат	12.92	Подвесной потолок – типа “Грильято”	12.92	Краска акриловая, обои под покраску, шпатлевка, грунтовка(стены из ГКЛ)	20.34	Краска акриловая, шпатлевка, грунтовка штукатурка, грунтовка	2.21	
					Краска акриловая, обои под покраску, шпатлевка, грунтовка (стены из сэндвич-панелей с внутренней стороны обшить листами ГКЛ по металлокаркасу)	19.35			

Ведомость отделки помещений Блок 6									
Наименование, № пом.	Вид отделки элементов интерьера								Примечание
	Пол	Площадь, м²	Потолок	Площадь, м²	Стены и перегородки	Площадь, м²	Цокольная панель	Площадь, м²	
Помещения на отм. +3.600									
Подсобное помещение (антресоль) (пом.№206)	Ламинат	60,38	Подвесной потолок – типа “Грильято”	14.74	Краска акриловая, обои под покраску, шпатлевка, грунтовка (стены из сэндвич-панелей с внутренней стороны обшить листами ГКЛ по металлокаркасу)	100.87	-	-	

Ведомость отделки помещений Блок 6									
Наименование, № пом.	Вид отделки элементов интерьера								Примечание
	Пол	Площадь, м²	Потолок	Площадь, м²	Стены и перегородки	Площадь, м²	Цокольная панель	Площадь, м²	
Помещения на отм. 0.000									
Санузел (№пом.104)	Керамическая плитка	1,08	Потолок реечного типа	1,08	Плитка керамическая на клею, грунтовка (стены из ГКЛ/В)	9.09	-	-	
Умывальная (№пом.105)	Керамическая плитка	1,17	Потолок реечного типа	1,17	Плитка керамическая на клею, грунтовка (стены из ГКЛ/В)	3.72	-	-	
					Плитка керамическая на клею, грунтовка (стены из сэндвич-панелей с внутренней стороны обшить листами ГКЛ по металлокаркасу)	4.16			
Пом. уборочного инвентаря (№пом.106)	Керамическая плитка	2.45	Потолок реечного типа	2.45	Плитка керамическая на клею, грунтовка (стены из ГКЛ/В)	9.67	-	-	
					Плитка керамическая на клею, грунтовка (стены из сэндвич-панелей с внутренней стороны обшить листами ГКЛ по металлокаркасу)	8.03			
Кабинет (№пом.107)	Ламинат	32,23	Подвесной потолок – типа “Грильято”	32,23	Краска акриловая, обои под покраску, шпатлевка, грунтовка (стены из ГКЛ)	17.16	Краска акриловая, шпатлевка, грунтовка штукатурка, грунтовка	3.42	
					Краска акриловая, обои под покраску, шпатлевка, грунтовка (стены из сэндвич-панелей с внутренней стороны обшить листами ГКЛ по металлокаркасу)	38.81			
Производственное помещение (пом.№108)	Упрочняющее покрытие Dugosog	606.6							

							01-ВЕН/18-СК13-АС1-С1				
							«Производственно-складской комплекс №13 «Industrial City», расположенный по адресу: Московская область, Городской округ Подольск, деревня Новоселки, территория Технопарка, 13»				
Изм.	Кол.уч.	Лист	№ док	Подпись	Дата	Строение 1			Стадия	Лист	Листов
Разраб.	Якунина				04.18				P	17	
Проверил	Черкасов				04.18	Ведомость отделки помещений Блок 6			ООО "КУРСКРЕГИОНПРОЕКТ"		
ГИП	Авдулов				04.18						
Н. контр.	Авдулов				04.18						

Инв. № подл.	Подпись и дата	Взам. инв. №

Ведомость отделки технические помещения

Наименование, № пом.	Вид отделки элементов интерьера								Примечание
	Пол	Площадь, м ²	Потолок	Площадь, м ²	Стены и перегородки	Площадь, м ²	Цоколь	Площадь, м ²	
Помещения на отм. 0.000									
ИТП, Водомерный узел (№пом.109)	Покраска пола обеспы- ливающей фасадной краской	21.00	Заводской готовности	-	Заводской готовности	-			

						01-ВЕН/18-СК13-АС1-С1		
						«Производственно-складской комплекс №13 «Industrial City», расположенный по адресу: Московская область, Городской округ Подольск, деревня Новоселки, территория Технопарка, 13»		
Изм.	Кол.уч.	Лист	№ док	Подпись	Дата			
Разраб.		Якунина			04.18	Строение 1	Стадия	Лист
Проверил		Черкасов			04.18		Р	18
ГИП		Авдулов			04.18	Ведомость отделки технических помещений	ООО "КУРСКРЕГИОНПРОЕКТ"	
Н. контр.		Авдулов			04.18			

Двери, ворота внутренние. Общие указания

В чертежах указаны общие требования и характеристики дверных блоков, а также спецификации и сводная ведомость. Производитель дверей не определен.

Все двери оснащены замками. Часть дверей запроектирована с ручками нажимного действия типа "антипаника". Наличие замков типа "антипаника" указано в спецификациях.

Противопожарные двери запроектированы по ГОСТ Р 57327-2016 "Двери металлические противопожарные".

Производителю дверей необходимо обязательно выполнить осмотр дверных проемов перед запуском изделий в производство. Типы дверных коробок могут уточняться производителем по месту.

Цвет внутренних дверей – RAL 9003 (белый) у металлических, деревянные – на усмотрение Заказчика.

В проекте использованы следующие типы дверных блоков:

- Тип 3 (маркировки 3-10, 3-13 и т.п.) – внутренние двери.
- Тип 4 (марки 4-10, 4-12 и т.п.) – внутренние противопожарные двери.

Материал дверей


МЕТ. – Металлическая коробка, плотно коробчатого типа, сварное из металлического листа толщ. до 0,8 м, с заполнением. Окраска порошковая, устойчивая к коррозии.

ДЕР - Двери деревянные с ламинированием.

Структура маркировки дверного блока:

Внутренние двери деревянные с ламинированием по ГОСТ 475-2016

ДМ 1 Рп Г Пр (21-9) — Высота полотна x Ширина полотна (в дм)

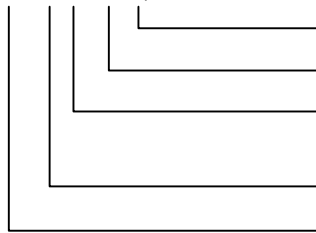

Пр - с порогом/ ПрБ - без порога/ По - с опускающимся порогом

- Г - глцхой/ 0 - остекленный

Рп - распашной правый/ Рл - распашной левый/ К - качающийся/

Р - раздвижной/ Р2- раздвижной двупольный/ С- складной

1 – распашной однополюсный/ 2- распашной двухполюсный

ДМ – дверной блок межкомнатный/


ДН – наружный входной в здание/

ДВ – внутренний входной в квартиры и в помещения общественных, производственных и вспомогательных зданий и сооружений/

ДС – дверной блок санузлов

Внутренние двери противопожарные по ГОСТ Р 57327-2016

ДПС 01 ПР 2100-1110 Е115

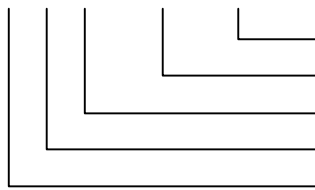

Огнестойкость

Высота коробки x Ширина коробки (в мм)

Пр- правое открывание/ Л- левое открывание

01-Однопальная /02- Двупольная

ДПС - дверь противопожарная стальная глухая/

ДПСО – дверь противопожарная стальная остекленная

Инв. № подл.	Изм.	Кол.уч.	Лист	№ док	Подпись	Дата	01-БЕН/18-СК13-АС1-С1		
							«Производственно-складской комплекс №13 «Industrial City», расположенный по адресу: Московская область, Городской округ Подольск, деревня Новоселки, территория Технопарка, 13»		
Взам. инв. №	Подпись и дата	Высота коробки х ширина коробки (в мм) Пр- правое открывание/ Л- левое открывание 01-Однопальная /02- Двупольная ДПС - дверь противопожарная стальная глухая/ ДПСО - дверь противопожарная стальная остекленная							

Инв. № подл.	Изм.	Кол.уч.	Лист	№ док	Подпись	Дата	01-БЕН/18-СК13-АС1-С1		
							«Производственно-складской комплекс №13 «Industrial City», расположенный по адресу: Московская область, Городской округ Подольск, деревня Новоселки, территория Технопарка, 13»		
Инв. № подл.	Изм.	Кол.уч.	Лист	№ док	Подпись	Дата	Строение 1		
							Стадия		
							Р		
							Лист		
							19		
							Листов		
Инв. № подл.	Изм.	Кол.уч.	Лист	№ док	Подпись	Дата	Двери внутренние. Общие указания		
							ООО "КУРСКИЙ РЕГИОН ПРОЕКТ"		

Спецификация внутренних дверей (начало)

Мака двери по проекту	Наименование помещения	Маркировка по ГОСТ	ТИП	Ширина проема	Высота проема	Уплотнение	Огнестойкость	Доводчик	Порог	Тип дверной коробки	Материал	Тип замка
-----------------------	------------------------	--------------------	-----	---------------	---------------	------------	---------------	----------	-------	---------------------	----------	-----------

На отм. 0.000

Блок 1

101	Тамбур	ДВ 1 Рн Г ПрБ (21-9) ГОСТ 475-2016	З-10	1010	2100	ДА	-	ДА	-	-	МЕТ	Анти-паника
102	Коридор	ДПС 01 Пр 2100-1010 ЕІЗО ГОСТ Р 57327-2016	4-10	1010	2100	ДА	ЕІЗО	ДА	-	-	МЕТ	Анти-паника
103	Кабинет	ДМ 1 Рн Г ПрБ (21-9) ГОСТ 475-2016	З-10.1	1010	2100	-	-	-	-	-	ДЕР	-
104	Санузел	-	-	-	-	-	-	-	-	-	-	-
105	Умывальная	ДС 1 Рн Г Пр (21-6) ГОСТ 475-2016	З-7.1	710	2100	-	-	-	ДА	-	ДЕР	-
106	Пом. уборочного инвентаря	ДПС 01 Пр 2100-710 ЕІЗО ГОСТ Р 57327-2016	4-7	710	2100	ДА	ЕІЗО	ДА	ДА	-	МЕТ	-
107	Кабинет	ДМ 1 Рн Г ПрБ (21-9) ГОСТ 475-2016	З-10	1010	2100	-	-	-	-	-	ДЕР	-
108	Производственное помещение	-	-	-	-	-	-	-	-	-	-	-

Блок 2

101	Тамбур	ДВ 1 Рн Г ПрБ (21-9) ГОСТ 475-2016	З-10.1	1010	2100	ДА	-	ДА	-	-	МЕТ	Анти-паника
102	Коридор	ДПС 01 Л 2100-1010 ЕІЗО ГОСТ Р 57327-2016	4-10.1	1010	2100	ДА	ЕІЗО	ДА	-	-	МЕТ	Анти-паника
103	Кабинет	ДМ 1 Рн Г ПрБ (21-9) ГОСТ 475-2016	З-10	1010	2100	-	-	-	-	-	ДЕР	-
104	Санузел	-	-	-	-	-	-	-	-	-	-	-
105	Умывальная	ДС 1 Рн Г Пр (21-6) ГОСТ 475-2016	З-7	710	2100	-	-	-	ДА	-	ДЕР	-
106	Пом. уборочного инвентаря	ДПС 01 Л 2100-710 ЕІЗО ГОСТ Р 57327-2016	4-7.1	710	2100	ДА	ЕІЗО	ДА	ДА	-	МЕТ	-
107	Кабинет	ДМ 1 Рн Г ПрБ (21-9) ГОСТ 475-2016	З-10.1	1010	2100	-	-	-	-	-	ДЕР	-
108	Производственное помещение	-	-	-	-	-	-	-	-	-	-	-

Взам. инв. №		106	Пом. уборочно-инвентаря		ДПС 01/1 2100-710 Е130 ГОСТ Р 57327-2016		4-7.1	710	2100	ДА	Е130	ДА	ДА	-	МЕТ	-
		107	Кабинет		ДМ 1 Рл Г ПрБ (21-9) ГОСТ 475-2016		3-10.1	1010	2100	-	-	-	-	-	ДЕР	-
		108	Производственное помещение		-		-	-	-	-	-	-	-	-	-	-
Подпись и дата							01-ВЕН/18-СК13-АС1-С1									
							«Производственно-складской комплекс №13 «Industrial City», расположенный по адресу: Московская область, Городской округ Подольск, деревня Новоселки, территория Технопарка, 13»									
		Изм.	Кол.уч.	Лист	№ док	Подпись	Дата	Строение 1					Стадия	Лист	Листов	
		Разраб.	Якунина			04.18	Р						20			
Проверил	Черкасов			04.18												
Инв. № подл.			ГИП		Авдулов		04.18	Спецификация внутренних дверей (начало)					ООО "КУРСКРЕГИОНПРОЕКТ"			
			Н. контр.		Авдулов		04.18									

Спецификация внутренних дверей (продолжение)

Мака двери по проекту	Наименование помещения	Маркировка по ГОСТ	ТИП	Ширина проема	Высота проема	Уплотнение	Огнестойкость	Доводчик	Порог	Тип дверной коробки	Материал	Тип замка
-----------------------	------------------------	--------------------	-----	---------------	---------------	------------	---------------	----------	-------	---------------------	----------	-----------

На отм. 0.000

Блок 3

101	Тамбур	ДВ 1 Рн Г ПрБ (21-9) ГОСТ 475-2016	3-10	1010	2100	ДА	-	ДА	-	-	МЕТ	Анти-паника
102	Коридор	ДПС 01 Пр 2100-1010 ЕІЗО ГОСТ Р 57327-2016	4-10	1010	2100	ДА	ЕІЗО	ДА	-	-	МЕТ	Анти-паника
103	Кабинет	ДМ 1 Рн Г ПрБ (21-9) ГОСТ 475-2016	3-10.1	1010	2100	-	-	-	-	-	ДЕР	-
104	Санузел	-	-	-	-	-	-	-	-	-	-	-
105	Умывальная	ДС 1 Рн Г Пр (21-6) ГОСТ 475-2016	3-7.1	710	2100	-	-	-	ДА	-	ДЕР	-
106	Пом. уборочного инвентаря	ДПС 01 Пр 2100-710 ЕІЗО ГОСТ Р 57327-2016	4-7	710	2100	ДА	ЕІЗО	ДА	ДА	-	МЕТ	-
107	Кабинет	ДМ 1 Рн Г ПрБ (21-9) ГОСТ 475-2016	3-10	1010	2100	-	-	-	-	-	ДЕР	-
108	Производственное помещение	-	-	-	-	-	-	-	-	-	-	-

Блок 4

101	Тамбур	ДВ 1 Рн Г ПрБ (21-9) ГОСТ 475-2016	3-10.1	1010	2100	ДА	-	ДА	-	-	МЕТ	Анти-паника
102	Коридор	ДПС 01 Л 2100-1010 ЕІЗО ГОСТ Р 57327-2016	4-10.1	1010	2100	ДА	ЕІЗО	ДА	-	-	МЕТ	Анти-паника
103	Кабинет	ДМ 1 Рн Г ПрБ (21-9) ГОСТ 475-2016	3-10	1010	2100	-	-	-	-	-	ДЕР	-
104	Санузел	-	-	-	-	-	-	-	-	-	-	-
105	Умывальная	ДС 1 Рн Г Пр (21-6) ГОСТ 475-2016	3-7	710	2100	-	-	-	ДА	-	ДЕР	-
106	Пом. уборочного инвентаря	ДПС 01 Л 2100-710 ЕІЗО ГОСТ Р 57327-2016	4-7.1	710	2100	ДА	ЕІЗО	ДА	ДА	-	МЕТ	-
107	Кабинет	ДМ 1 Рн Г ПрБ (21-9) ГОСТ 475-2016	3-10.1	1010	2100	-	-	-	-	-	ДЕР	-
108	Производственное помещение	-	-	-	-	-	-	-	-	-	-	-

Взам инв. №	
Подпись и дата	
Инв. № подл.	

						01-ВЕН/18-СК13-АС1-С1				
						«Производственно-складской комплекс №13 «Industrial City», расположенный по адресу: Московская область, Городской округ Подольск, деревня Новоселки, территория Технопарка, 13»				
Изм.	Кол.уч.	Лист	№ док	Подпись	Дата	Строение 1		Стадия	Лист	Листов
Разраб.		Якунина			04.18			Р	21	
Проверил		Черкасов			04.18	Спецификация внутренних дверей (продолжение)		ООО "КУРСКИЙ РЕГИОН ПРОЕКТ"		
ГИП		Авдулов			04.18					
Н. контр.		Авдулов			04.18					

Спецификация внутренних дверей (продолжение)

Мака двери по проекту	Наименование помещения	Маркировка по ГОСТ	ТИП	Ширина проема	Высота проема	Уплотнение	Огнестойкость	Доводчик	Порог	Тип дверной коробки	Материал	Тип замка
-----------------------	------------------------	--------------------	-----	---------------	---------------	------------	---------------	----------	-------	---------------------	----------	-----------

На отм. 0.000

Блок 5

101	Тамбур	ДВ 1 Рн Г ПрБ (21-9) ГОСТ 475-2016	З-10	1010	2100	ДА	-	ДА	-	-	МЕТ	Анти-паника
102	Коридор	ДПС 01 Пр 2100-1010 Е130 ГОСТ Р 57327-2016	4-10	1010	2100	ДА	Е130	ДА	-	-	МЕТ	Анти-паника
103	Кабинет	ДМ 1 Рл Г ПрБ (21-9) ГОСТ 475-2016	З-10.1	1010	2100	-	-	-	-	-	ДЕР	-
104	Санузел	-	-	-	-	-	-	-	-	-	-	-
105	Умывальная	ДС 1 Рл Г Пр (21-6) ГОСТ 475-2016	З-7.1	710	2100	-	-	-	ДА	-	ДЕР	-
106	Пом. уборочного инвентаря	ДПС 01 Пр 2100-710 Е130 ГОСТ Р 57327-2016	4-7	710	2100	ДА	Е130	ДА	ДА	-	МЕТ	-
107	Кабинет	ДМ 1 Рл Г ПрБ (21-9) ГОСТ 475-2016	З-10	1010	2100	-	-	-	-	-	ДЕР	-
108	Производственное помещение	-	-	-	-	-	-	-	-	-	-	-

Блок 6

101	Тамбур	ДВ 1 Рл Г ПрБ (21-9) ГОСТ 475-2016	З-10.1	1010	2100	ДА	-	ДА	-	-	МЕТ	Анти-паника
102	Коридор	ДПС 01 Л 2100-1010 Е130 ГОСТ Р 57327-2016	4-10.1	1010	2100	ДА	Е130	ДА	-	-	МЕТ	Анти-паника
103	Кабинет	ДМ 1 Рл Г ПрБ (21-9) ГОСТ 475-2016	З-10	1010	2100	-	-	-	-	-	ДЕР	-
104	Санузел	-	-	-	-	-	-	-	-	-	-	-
105	Умывальная	ДС 1 Рл Г Пр (21-6) ГОСТ 475-2016	З-7	710	2100	-	-	-	ДА	-	ДЕР	-
106	Пом. уборочного инвентаря	ДПС 01 Л 2100-710 Е130 ГОСТ Р 57327-2016	4-7.1	710	2100	ДА	Е130	ДА	ДА	-	МЕТ	-
107	Кабинет	ДМ 1 Рл Г ПрБ (21-9) ГОСТ 475-2016	З-10.1	1010	2100	-	-	-	-	-	ДЕР	-
108	Производственное помещение	-	-	-	-	-	-	-	-	-	-	-

Инв. № подл.	Изм.	Кол.уч.	Лист	№ док	Подпись	Дата	01-ВЕН/18-СК13-АС1-С1					
							«Производственно-складской комплекс №13 «Industrial City», расположенный по адресу: Московская область, Городской округ Подольск, деревня Новоселки, территория Технопарка, 13»					
Инв. № подл.	Изм.	Кол.уч.	Лист	№ док	Подпись	Дата	Строение 1			Стадия	Лист	Листов
										Р	22	
							Спецификация внутренних дверей (продолжение)			ООО "КУРСКИЙ РЕГИОН ПРОЕКТ"		

Спецификация внутренних дверей (окончание)

Мака дверь по проекту	Наименование помещения	Маркировка по ГОСТ	ТИП	Ширина проема	Высота проема	Уплотнение	Огнестойкость	Доводчик	Порог	Тип дверной коробки	Материал	Тип замка
На отм. +3.600												
201	Подсобное помещение (антресоль)	ДПС 01 Л 2100-1010 EI30 ГОСТ Р 57327-2016	4-10.1	1010	2100	ДА	EI30	ДА	-	-	МЕТ	-
202	Подсобное помещение (антресоль)	ДПС 01 Пр 2100-1010 EI30 ГОСТ Р 57327-2016	4-10	1010	2100	ДА	EI30	ДА	-	-	МЕТ	-
203	Подсобное помещение (антресоль)	ДПС 01 Л 2100-1010 EI30 ГОСТ Р 57327-2016	4-10.1	1010	2100	ДА	EI30	ДА	-	-	МЕТ	-
204	Подсобное помещение (антресоль)	ДПС 01 Пр 2100-1010 EI30 ГОСТ Р 57327-2016	4-10	1010	2100	ДА	EI30	ДА	-	-	МЕТ	-
205	Подсобное помещение (антресоль)	ДПС 01 Л 2100-1010 EI30 ГОСТ Р 57327-2016	4-10.1	1010	2100	ДА	EI30	ДА	-	-	МЕТ	-
206	Подсобное помещение (антресоль)	ДПС 01 Пр 2100-1010 EI30 ГОСТ Р 57327-2016	4-10	1010	2100	ДА	EI30	ДА	-	-	МЕТ	-


Сводная спецификация внутренних дверей

Обозначение	Наименование (согласно спецификации внутренних дверей)	Тип	Кол.
ГОСТ 475-2016	ДС 1 Рп Г Пр (21-6)	3-7	3
ГОСТ 475-2016	ДС 1 Рл Г Пр (21-6)	3-7.1	3
ГОСТ 475-2016	ДМ 1 Рп Г ПрБ (21-9)	3-10	6
ГОСТ 475-2016	ДМ 1 Рл Г ПрБ (21-9)	3-10.1	6
ГОСТ 475-2016	ДВ 1 Рп Г ПрБ (21-9)	3-10	3
ГОСТ 475-2016	ДВ 1 Рл Г ПрБ (21-9)	3-10.1	3
ГОСТ Р 57327-2016	ДПС 01 Пр 2100-710 EI30	4-7	3
ГОСТ Р 57327-2016	ДПС 01 Л 2100-710 EI30	4-7.1	3
ГОСТ Р 57327-2016	ДПС 01 Пр 2100-1010 EI30	4-10	6
ГОСТ Р 57327-2016	ДПС 01 Л 2100-1010 EI30	4-10.1	6
Итого:			42

Инв. № подл.	Инв. №	Взам. инв. №	Подпись и дата	01-ВЕН/18-СК13-АС1-С1							
				«Производственно-складской комплекс №13 «Industrial City», расположенный по адресу: Московская область, Городской округ Подольск, деревня Новоселки, территория Технопарка, 13»							
Инв. № подл.	Инв. №	Взам. инв. №	Подпись и дата	Изм.	Кол.уч.	Лист	№ док	Подпись	Дата		
				Разраб.	Якунина		04.18	Строение 1	Стадия	Лист	Листов
				Проверил	Черкасов		04.18		Р	23	
				ГИП	Авдулов		04.18	Спецификация внутренних дверей (окончание) Сводная спецификация внутренних дверей			
Н. контр.	Авдулов		04.18								

ООО "КУРСКИЙ РЕГИОН ПРОЕКТ"

Дверной блок Тип 3-7, 3-7.1, 4-7, 4-7.1

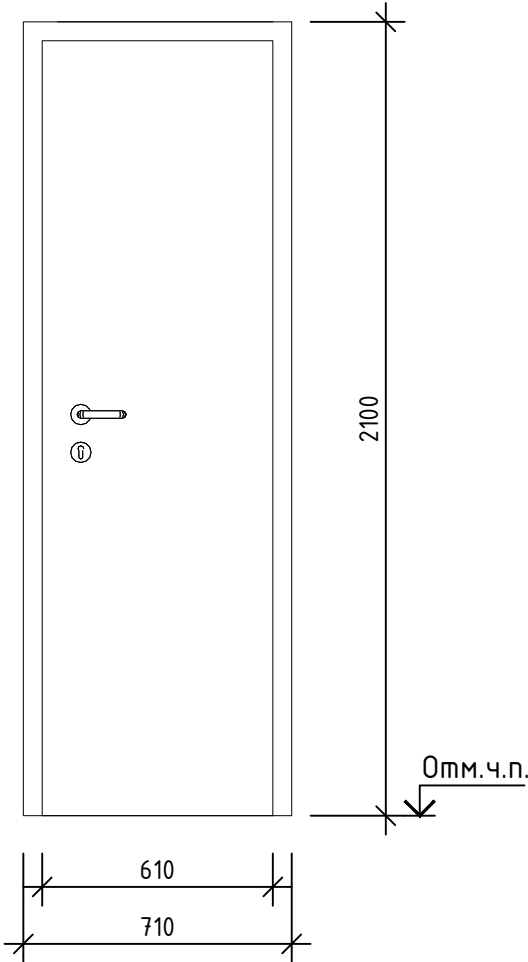

- - Цвет отделки
металлического дверного блока
белый RAL 9003
- - Цвет ламинирования деревянного
дверного блока
на усмотрение Заказчика.

Тип 3-7 - 710x2100h
Площадь (дана по строительному проему) 1шт. - 1,49 м²
Кол-во по проекту -3 шт.

Тип 3-7.1 - 710x2100h
Площадь (дана по строительному проему) 1шт. - 1,49 м²
Кол-во по проекту -3 шт.


Тип 4-7- 710x2100h
Площадь (дана по строительному проему) 1шт. - 1,49 м²
Кол-во по проекту -3 шт.

Тип 4-7.1 - 710x2100h
Площадь (дана по строительному проему) 1шт. - 1,49 м²
Кол-во по проекту -3 шт.

- Примечание
1. Дверной блок 3-7, 3-7.1 деревянный с ламинированием;
 2. Дверной блок 4-7, 4-7.1 противопожарный (предел огнестойкости см. спецификацию дверей);
 3. Направление открывания, см. спецификацию дверей;
 4. Габаритные размеры изделий указаны по проему;
 5. Изделия заказывают после предварительных обмеров существующих проемов;
 6. Двери замаркированы на схеме дверных проемов см. л. 6,8

Инв. № подл.	Взам. инв. №	1. Дверной блок 3-7, 3-7.1 бесстворчатый с напавлением; 2. Дверной блок 4-7, 4-7.1 противопожарный (предел огнестойкости см. спецификацию дверей); 3. Направление открывания, см. спецификацию дверей; 4. Габаритные размеры изделий указаны по проему; 5. Изделия заказывают после предварительных замеров существующих проемов; 6. Двери замаркированы на схеме дверных проемов см. л. 6,8								
		01-ВЕН/18-СК13-АС1-С1 «Производственно-складской комплекс №13 «Industrial City», расположенный по адресу: Московская область, Городской округ Подольск, деревня Новоселки, территория Технопарка, 13»								
Подпись и дата							Строение 1	Стадия	Лист	Листов
	Изм.	Кол.уч.	Лист	№ док	Подпись	Дата		Р	24	
	Разраб.	Якунина			04.18					
	Проверил	Черкасов			04.18					
	ГИП	Авдулов			04.18					
							Дверной блок Тип 3-7, 3-7.1, 4-7, 4-7.1	ООО "КУРСКИЙ РЕГИОН ПРОЕКТ"		

Дверной блок Тип 3-10, 3-10.1, 4-10, 4-10.1

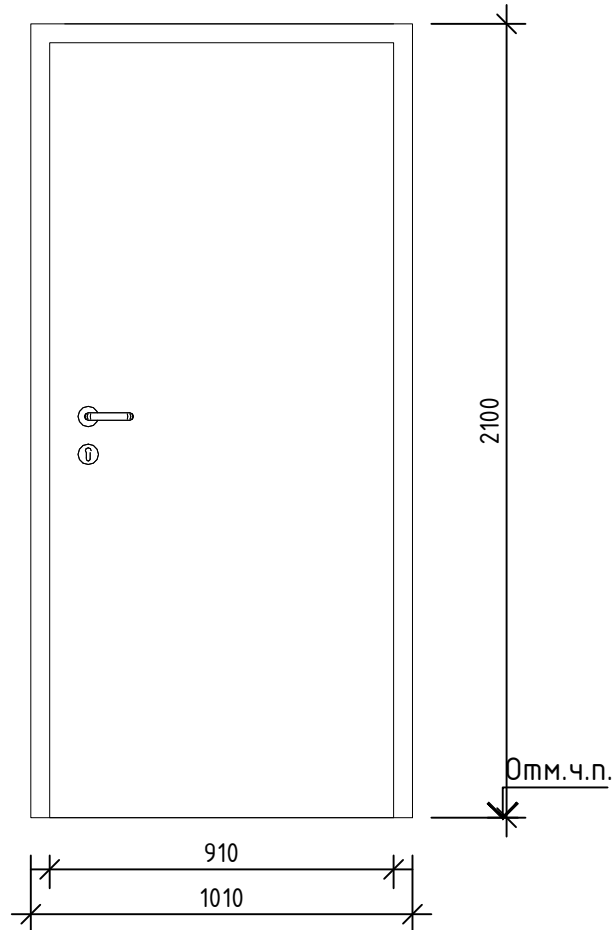

- Цвет отделки металлического дверного блока белый RAL 9003
- Цвет ламинирования деревянного, металлического дверного блока на усмотрение Заказчика.

Тип 3-10 - 1010x2100h
Площадь (дана по строительному проему) 1шт. - 2,12 м²
Кол-во по проекту -9 шт.

Тип 3-10.1 - 1010x2100h
Площадь (дана по строительному проему) 1шт. - 2,12 м²
Кол-во по проекту -9 шт.

Тип 4-10 - 1010x2100h
Площадь (дана по строительному проему) 1шт. - 2,12 м²
Кол-во по проекту -6 шт.


Тип 4-10.1 - 1010x2100h
Площадь (дана по строительному проему) 1шт. - 2,12 м²
Кол-во по проекту -6 шт.

Примечание

1. Дверной блок 3-10, 3-10.1 деревянный, с ламинированием, металлический;
2. Дверной блок 4-10, 4-10.1 противопожарный (предел огнестойкости см. спецификацию дверей);
3. Направление открывания, см. спецификацию дверей;
4. Габаритные размеры изделий указаны по проему;
5. Изделия заказывают после предварительных обмеров существующих проемов;
6. Двери замаркированы на схеме дверных проемов см. л. 6,8

Инв. № подл.	Подпись и дата	Взам. инв. №	1. Дверной блок 3-10, 3-10.1 деревянный, с ламинированием, металлический; 2. Дверной блок 4-10, 4-10.1 противопожарный (предел огнестойкости см. спецификацию дверей); 3. Направление открывания, см. спецификацию дверей; 4. Габаритные размеры изделий указаны по проему; 5. Изделия заказывают после предварительных обмеров существующих проемов; 6. Двери замаркированы на схеме дверных проемов см. л. 6,8						
							01-ВЕН/18-СК13-АС1-С1		
							«Производственно-складской комплекс №13 «Industrial City», расположенный по адресу: Московская область, Городской округ Подольск, деревня Новоселки, территория Технопарка, 13»		
	Изм.	Кол.уч.	Лист	№ док	Подпись	Дата			
	Разраб.		Якунина			04.18			
	Проверил		Черкасов			04.18	Строение 1		
									
	ГИП		Авдулов			04.18			
	Н. контр.		Авдулов			04.18	Дверной блок Тип 3-10, 3-10.1, 4-10, 4-10.1		
							ООО "КУРСКРЕГИОНПРОЕКТ"		

Раскладка стеновых панелей по оси 2, 3, 4, 5, 6

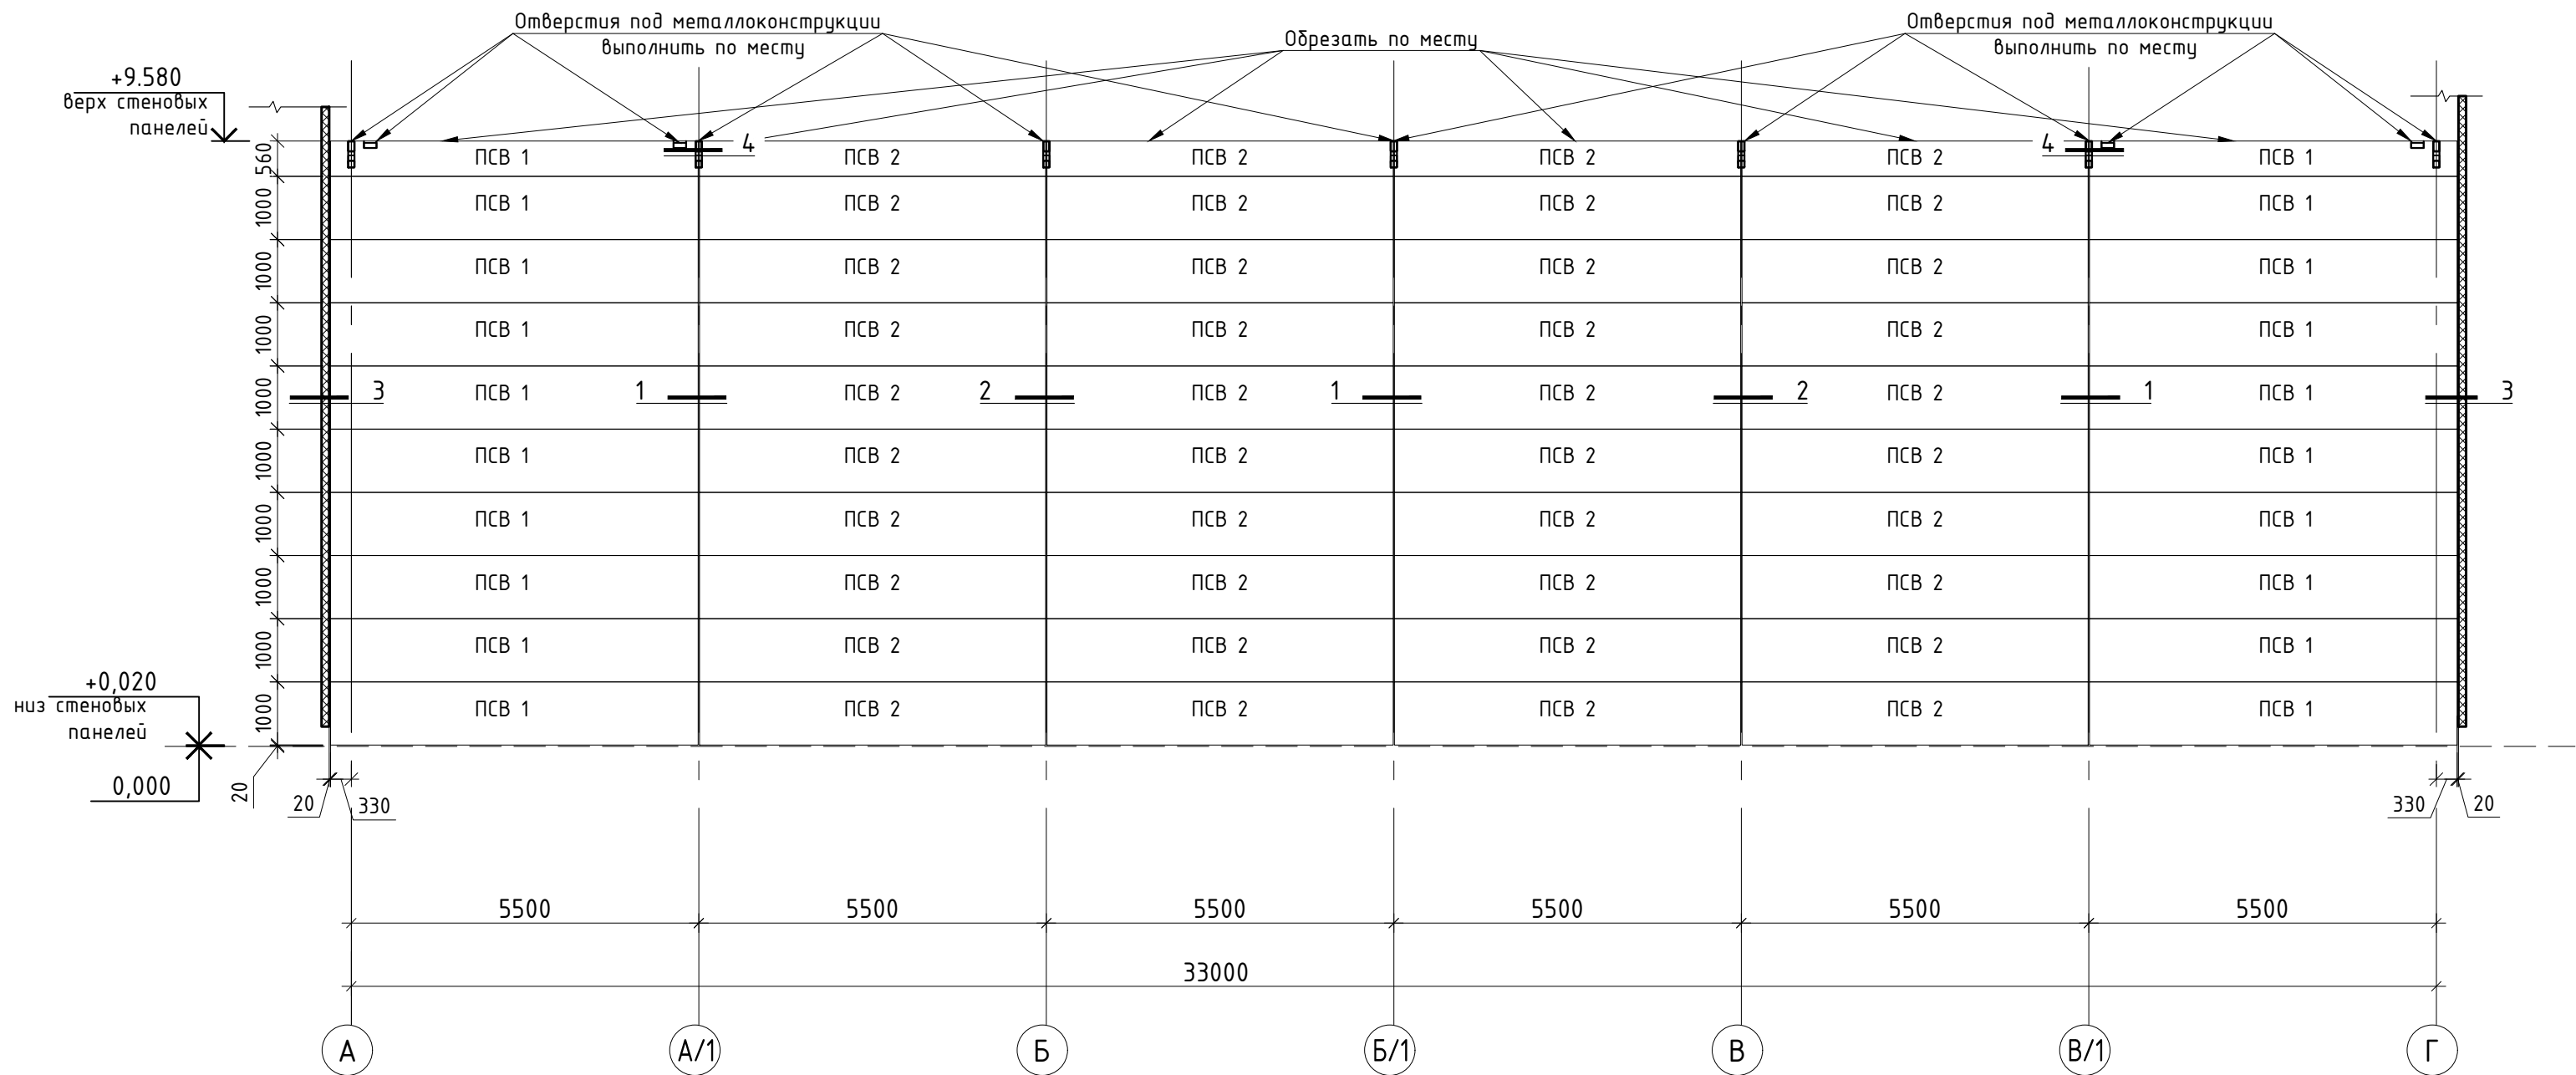



Условные обозначения:

- ПСВ 1 - Панель стеновая внутренняя
— геометрическое исполнение внутренней панели


Спецификация внутренних сэндвич-панелей

Марка поз.	ОБОЗНАЧЕНИЕ	НАИМЕНОВАНИЕ	Количество внутренних сэндвич-панелей по фасадам, шт.						Масса ед. шт.	Примечание
			по осц 2	по осц 3	по осц 4	по осц 5	по осц 6	Всего		
ПСВ 1	ТУ 5284-003-54655944-2004	“Белпанель” С4-100.1000.5820-0.5мп-0.5см	20	20	20	20	20	100		RAL 9003
ПСВ 2		“Белпанель” С4-100.1000.5480-0.5мп-0.5см	40	40	40	40	40	200		RAL 9003
Итого внутренних стеновых панелей			60	60	60	60	60	300		


Узел стыковки стеновых панелей по длине (см. прим. п.1)

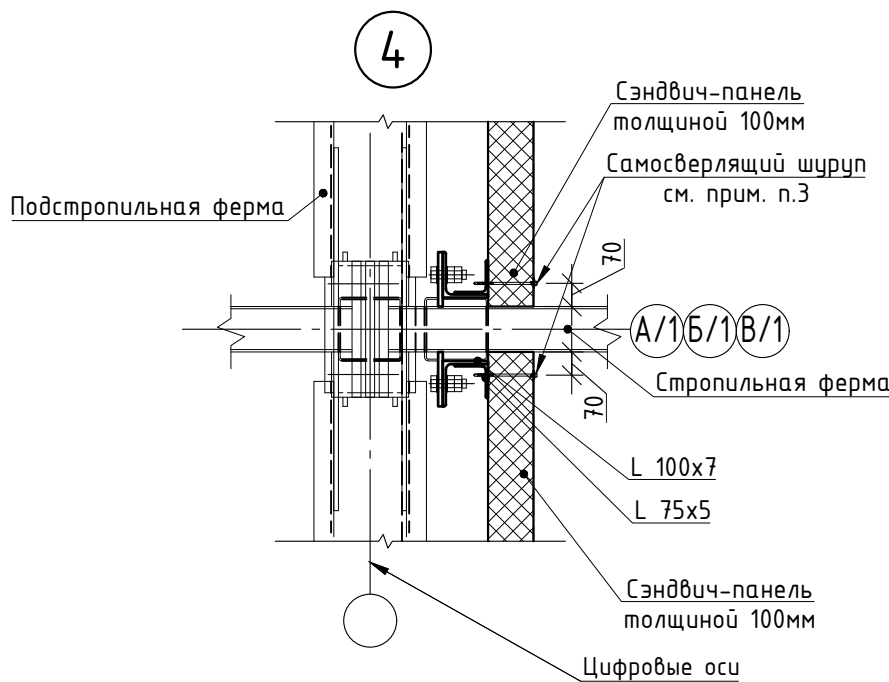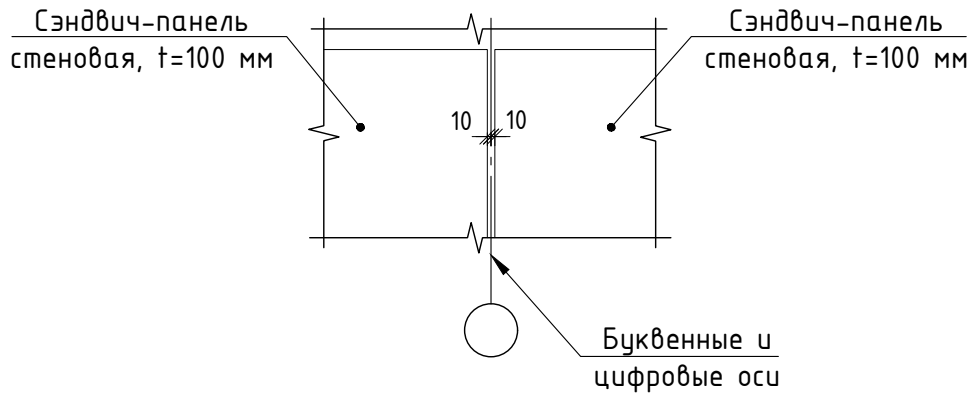


1

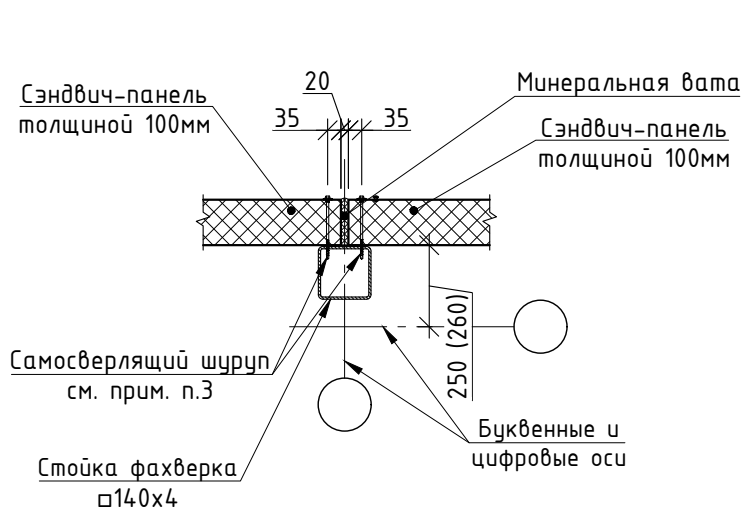

2

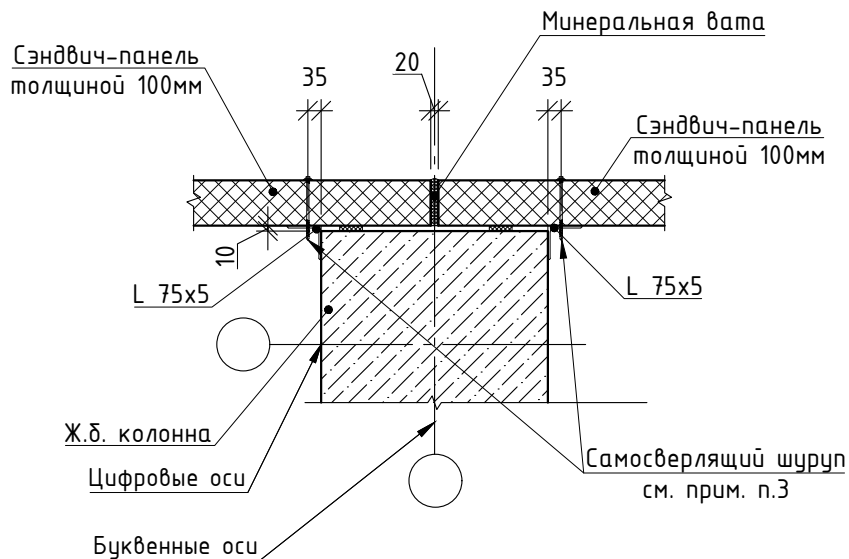

3

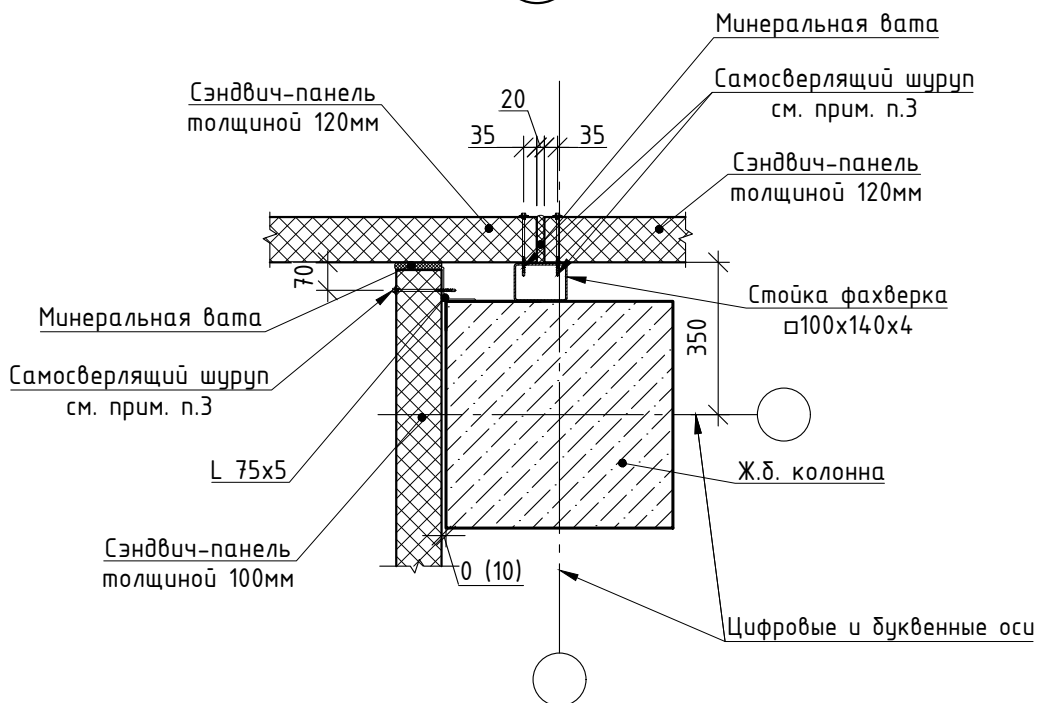


Примечания:

- Стеновые панели по длине монтировать с зазором 20 мм. Узел стыковки панелей смотри данный лист.
- Узлы 1-11 смотри данный лист
- Для крепления сэндвич-панелей использовать самосверлящий шуруп SFS intek SDT 14-A19-5.5x160:
 - по 3 в ряд шурупа на панель и прогон для сэндвич-панелей средних пролетов;
 - по 4 в ряд шурупа на панель и прогон для сэндвич-панелей крайних пролетов.
- Спецификацию наружных сэндвич-панелей смотри л.9 01-БЕН/18-СК 13-АС2-С1
- Проемы в сэндвич-панелях выполнить после их монтажа к стойкам фахверка.
- Монтаж внутренних сэндвич-панелей вдоль ось В произвести первоначально.

						01-БЕН/18-СК13-АС1-С1			
						«Производственно-складской комплекс №13 «Industrial City», расположенный по адресу: Московская область, Городской округ Подольск, деревня Новоселки, территория Технопарка, 13»			
Изм.	Кол.уч.	Лист	№ док	Подпись	Дата	Строение 1	Стадия	Лист	Листов
Разраб.	Якунина				04.18		Р	26	
Проверил	Черкасов				04.18				
ГИП	Авдулов				04.18	Раскладка стеновых панелей по оси 2,3,4,5,6. Спецификация внутренних сэндвич-панелей	ООО "КУРСКРЕГИОНПРОЕКТ"		
Н. контр.	Авдулов				04.18				


Вид в осях А-Г

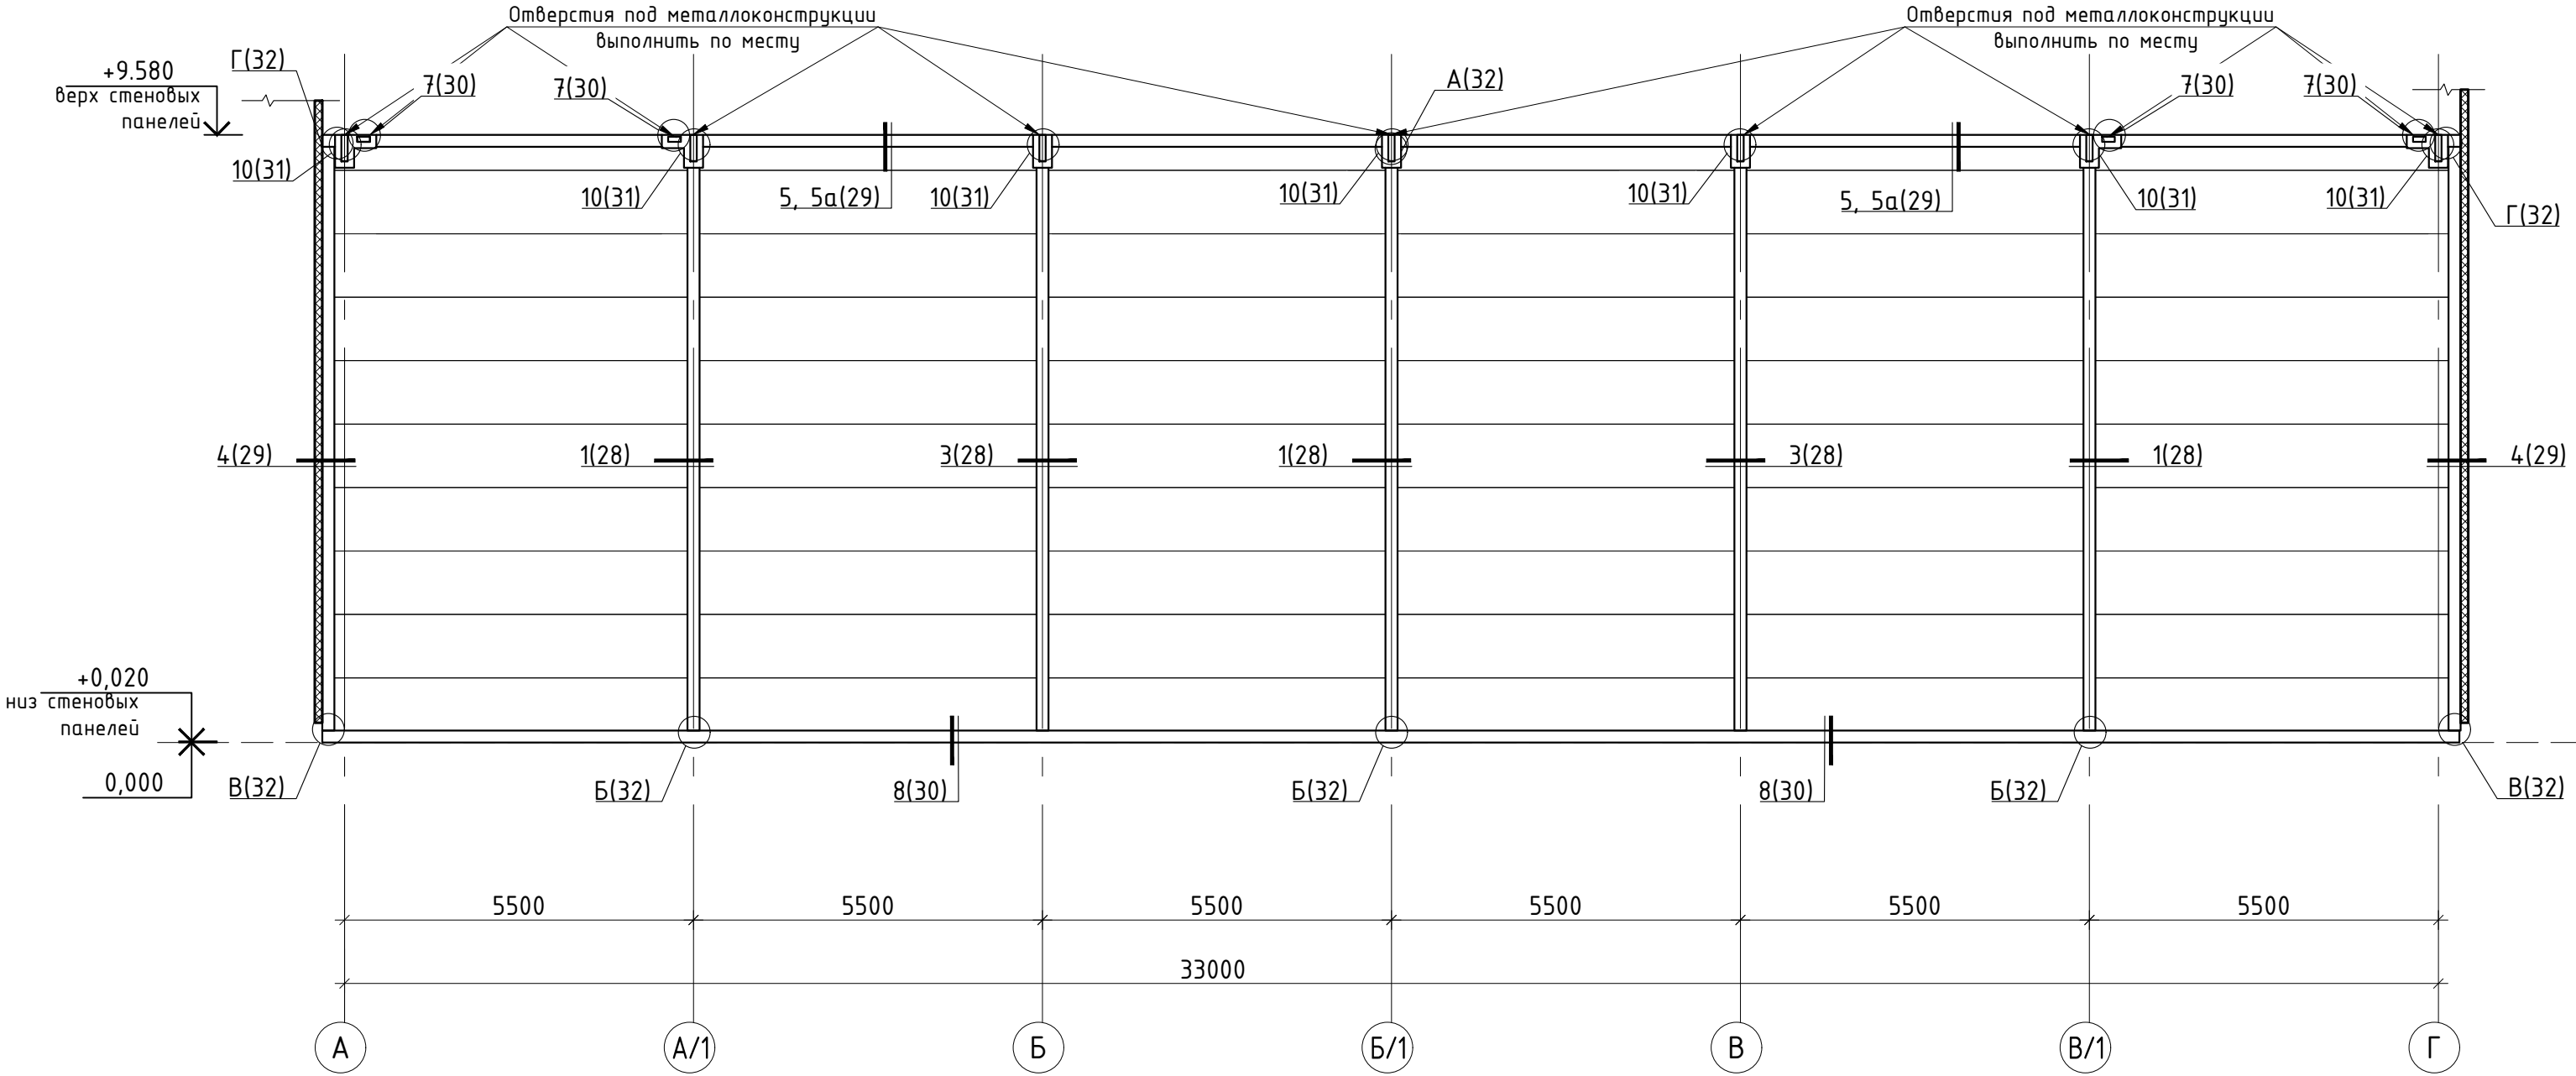

Инв. № подл.	Подпись и дата	Взам. инв. №

01-ВЕН/18-СК13-АС1-С1					
«Производственно-складской комплекс №13 «Industrial City», расположенный по адресу: Московская область, Городской округ Подольск, деревня Новоселки, территория Технопарка, 13»					
Изм.	Кол.уч.	Лист	№ док.	Подпись	Дата
Разраб.	Якунина	04.18			
Проверил	Черкасов	04.18			
ГИП	Абдулов	04.18			
Н. контр.	Абдулов	04.18			
Строение 1				Р	27
Вид в осях А-Г				ООО «КУРСКРЕГИОНПРОЕКТ»	



Инв. №	Взам. инв. №
№ подл.	Дата
Подпись	Инф. №

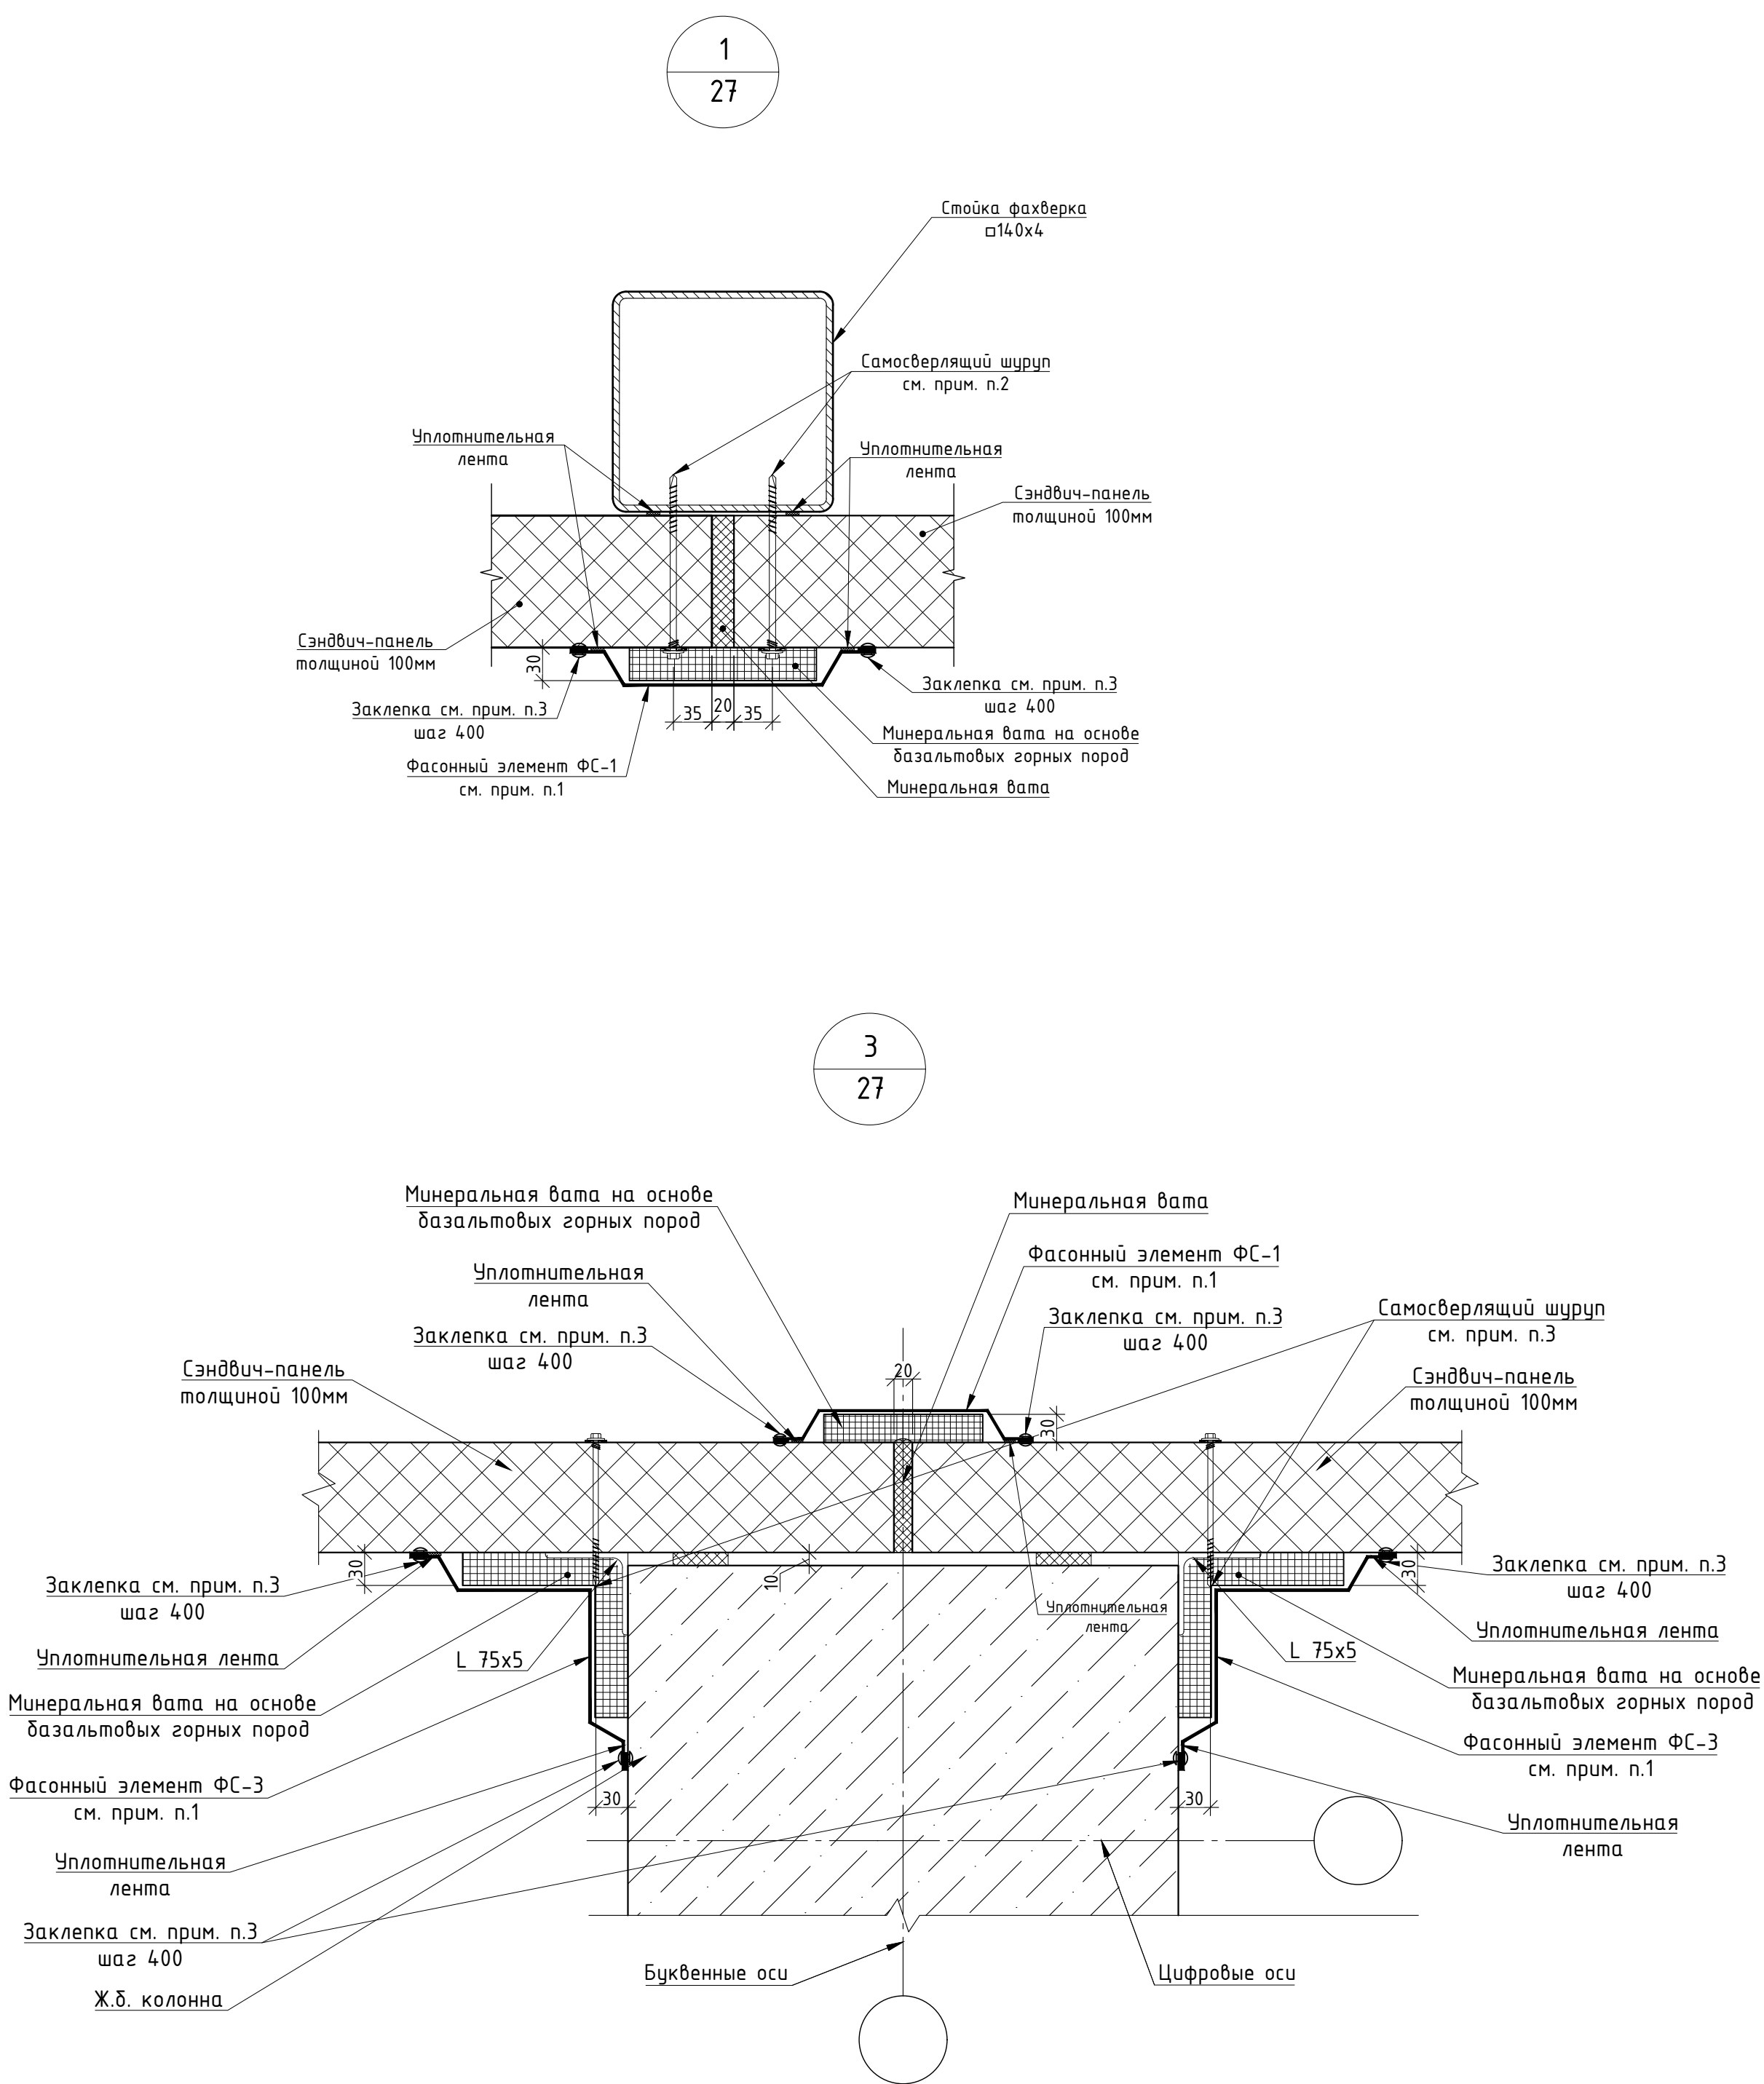

- Примечания:
- Ведомость фасонных элементов см. лист 33.
 - Для крепления сэндвич-панелей использовать самосверлящий шуруп SFS intek SDT 14-A19-5.5х160:
 - по 3 шурупа на панель и прогон для сэндвич-панелей средних пролетов;
 - по 4 шурупа на панель и прогон для сэндвич-панелей крайних пролетов.
 - Для крепления фасонных элементов использовать:
 - заклепку SFS intek ATC-D-3,2х8,0 к панелям;
 - самосверлящий шуруп SFS intek SD14-T15-5.5х32 к стальным конструкциям;
 - Фасонные элементы внутри помещения не предусматриваются, отделку откосов выполнить при общей отделке помещений.
 - После монтажа панелей, перед заказом фасонных элементов, необходимо уточнить габариты всех фасонных элементов

						01-ВЕН/18-СК13-АС1-С1			
						«Производственно-складской комплекс №13 «Industrial City», расположенный по адресу: Московская область, Городской округ Подольск, деревня Новоселки, территория Технопарка, 13»			
Изм.	Кол.уч.	Лист	№ док	Подпись	Дата	Строение 1	Стадия	Лист	Листов
Разраб.		Якунина			04.18		Р	28	
Проверил		Черкасов			04.18				
						Узлы 1, 3	ООО «КУРСКРЕГИОНПРОЕКТ»		
ГИП		Абдулов			04.18				
Н. контр.		Абдулов			04.18				




Примечания:
1. Ведомость фасонных элементов см. лист 33.
2. Для крепления сэндвич-панелей использовать самосверлящий шуруп SFS intek SDT 14-A19-5.5x160:
- по 3 шурупа на панель и прогон для сэндвич-панелей средних пролетов;
- по 4 шурупа на панель и прогон для сэндвич-панелей крайних пролетов.
3. Для крепления фасонных элементов использовать:
- заклепку SFS intek ATC-D-3,2x8,0 к панелям;
- самосверлящий шуруп SFS intek SD14-T15-5.5x32 к стальным конструкциям;
4. Фасонные элементы внутри помещения не предусматриваются, отделку откосов выполнить при общей отделке помещений.
5. После монтажа панелей, перед заказом фасонных элементов, необходимо уточнить габариты всех фасонных элементов

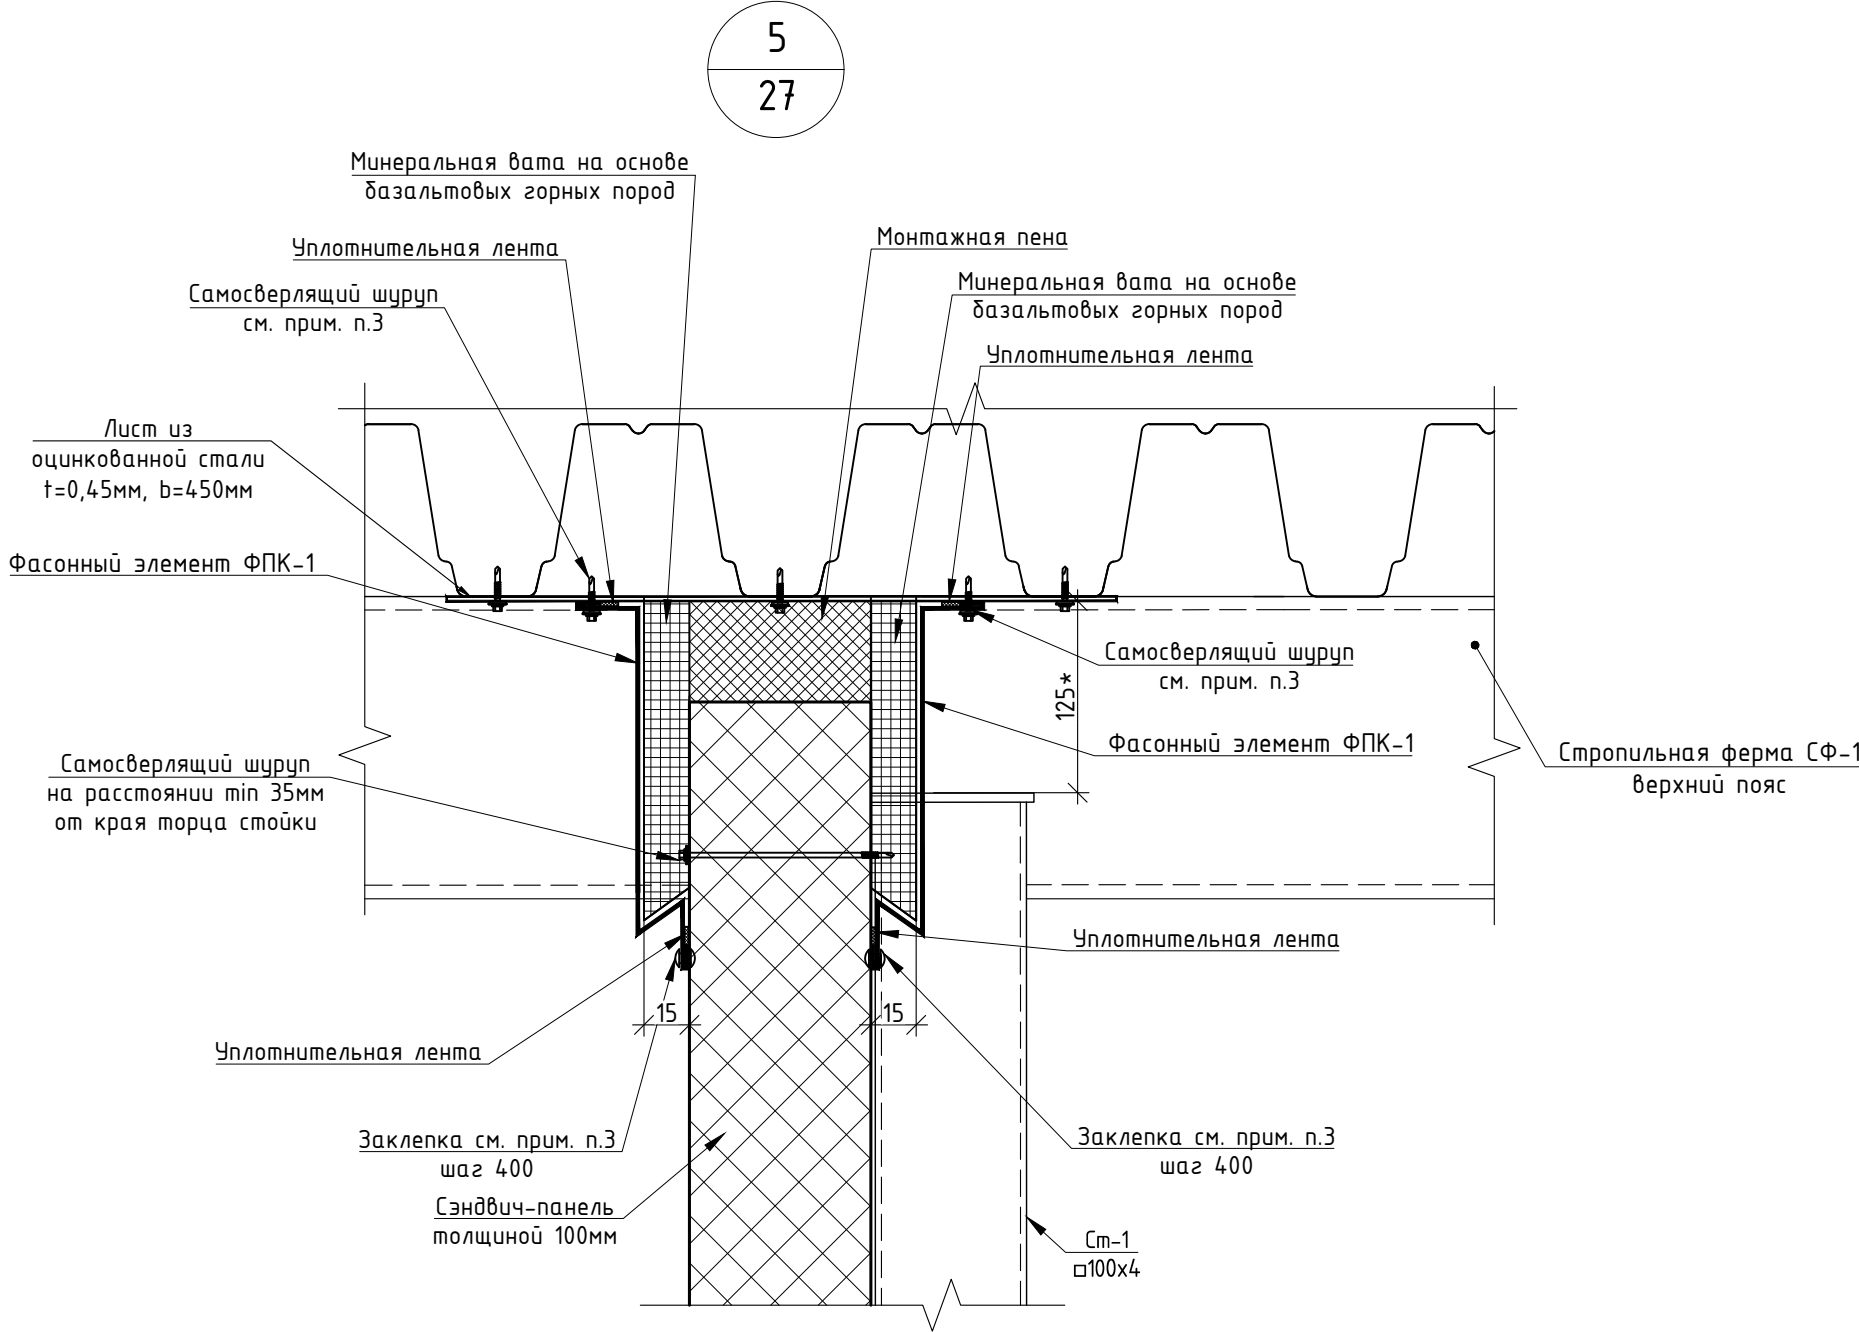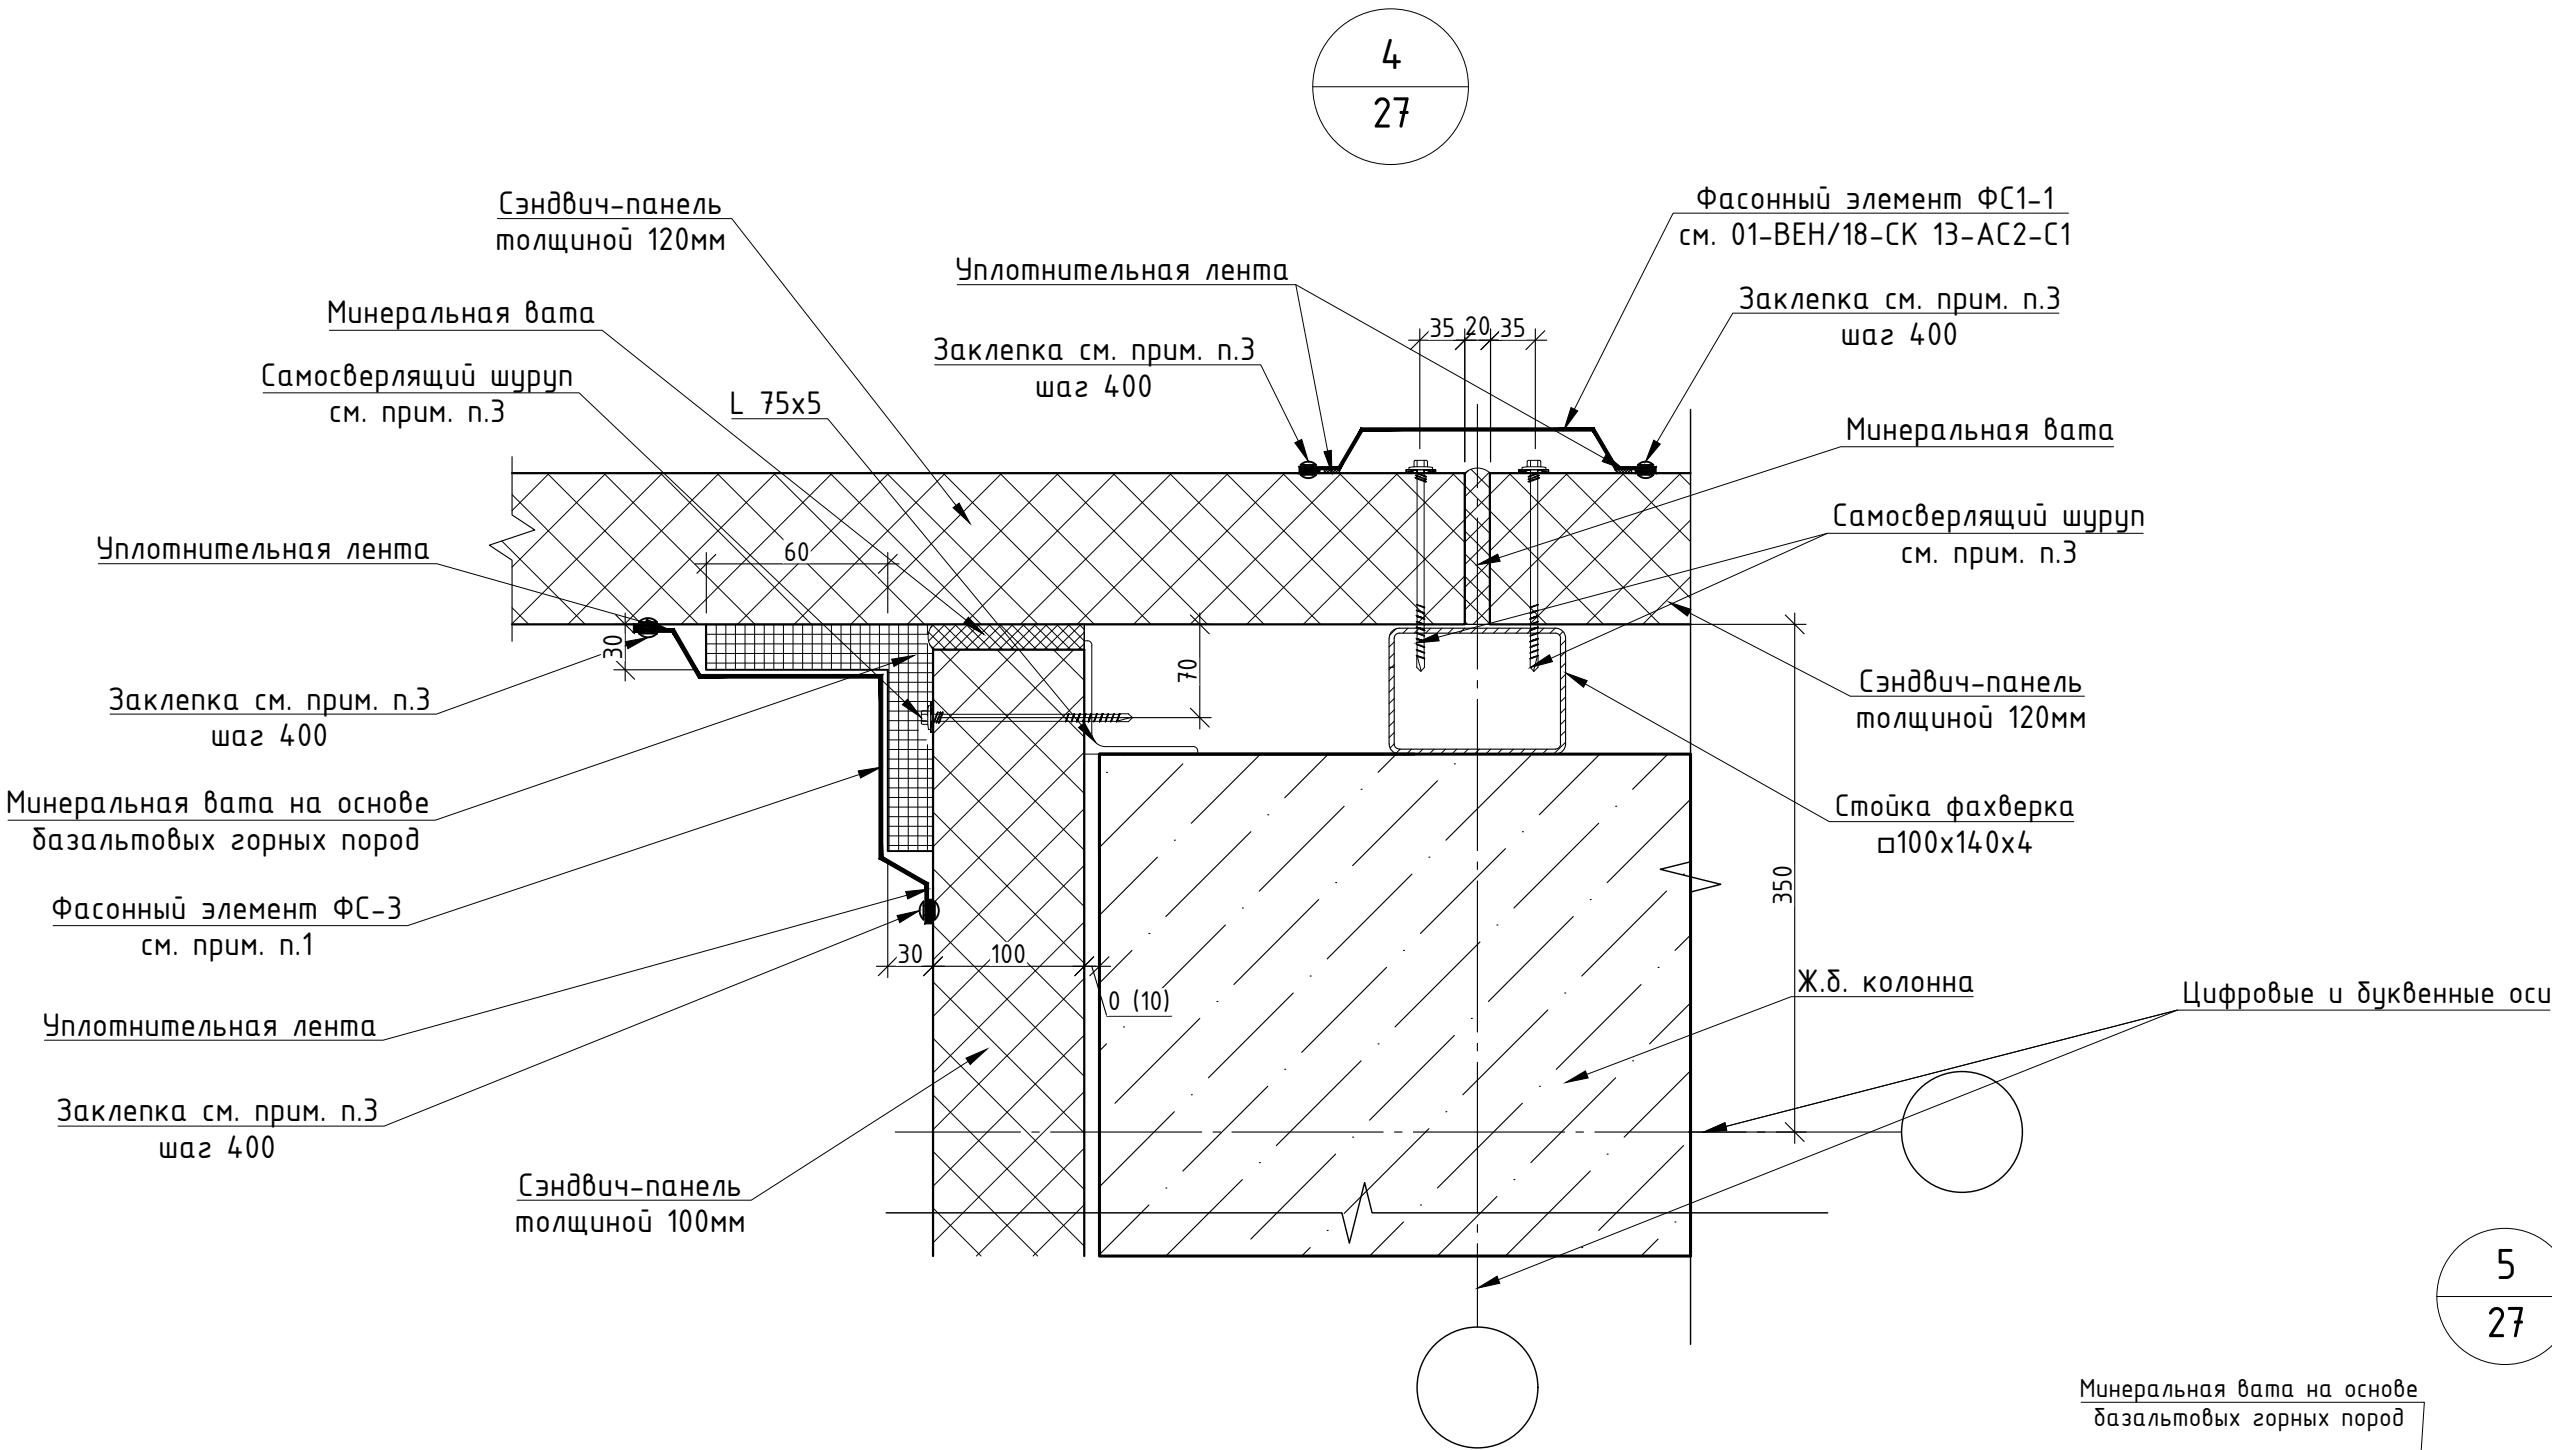



						01-ВЕН/18-СК13-АС1-С1			
						«Производственно-складской комплекс №13 «Industrial City», расположенный по адресу: Московская область, Городской округ Подольск, деревня Новоселки, территория Технопарка, 13»			
Изм.	Кол.уч.	Лист	№ док	Подпись	Дата	Строение 1	Стадия	Лист	Листов
Разраб.		Якунина			04.18		Р	29	
Проверил		Черкасов			04.18				
					04.18	Узлы 4, 5	ООО"КУРСКРЕГИОНПРОЕКТ"		
ГИП		Авдулов			04.18				
Н. контр.		Авдулов			04.18				

Инв. №	Взам. инв. №
подл.	инв.
Дата	Подпись

- Примечания:
1. Ведомость фасонных элементов см. лист 33.
 2. Для крепления сэндвич-панелей использовать самосверлящий шуруп SFS intek SDT 14-A19-5.5x160:
 - по 3 шурупа на панель и прогон для сэндвич-панелей средних пролетов;
 - по 4 шурупа на панель и прогон для сэндвич-панелей крайних пролетов.
 3. Для крепления фасонных элементов использовать:
 - заклепку SFS intek ATC-D-3,2x8,0 к панелям;
 - самосверлящий шуруп SFS intek SD14-T15-5.5x32 к стальным конструкциям;
 - самосверлящий шуруп SFS intek SD14-T15-5.5x32 к стальным конструкциям;
 - дюбель-гвоздь к бетонным конструкциям.
 4. Фасонные элементы внутри помещения не предусматриваются, отделку откосов выполнить при общей отделке помещений.
 5. После монтажа панелей, перед заказом фасонных элементов, необходимо уточнить габариты всех фасонных элементов

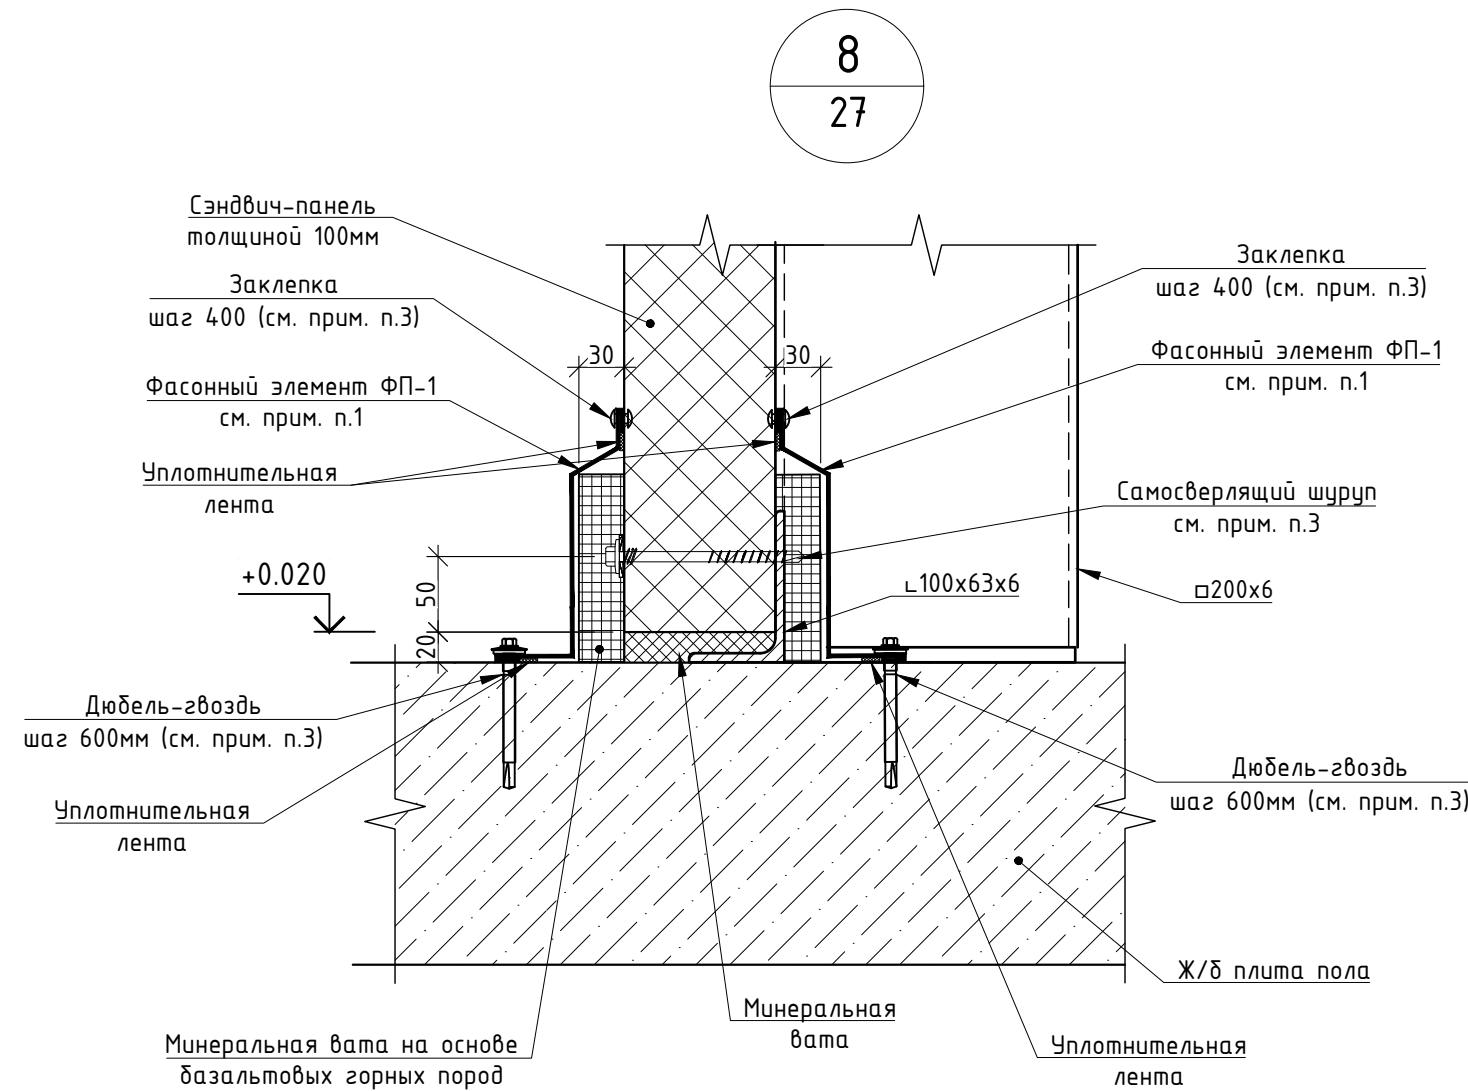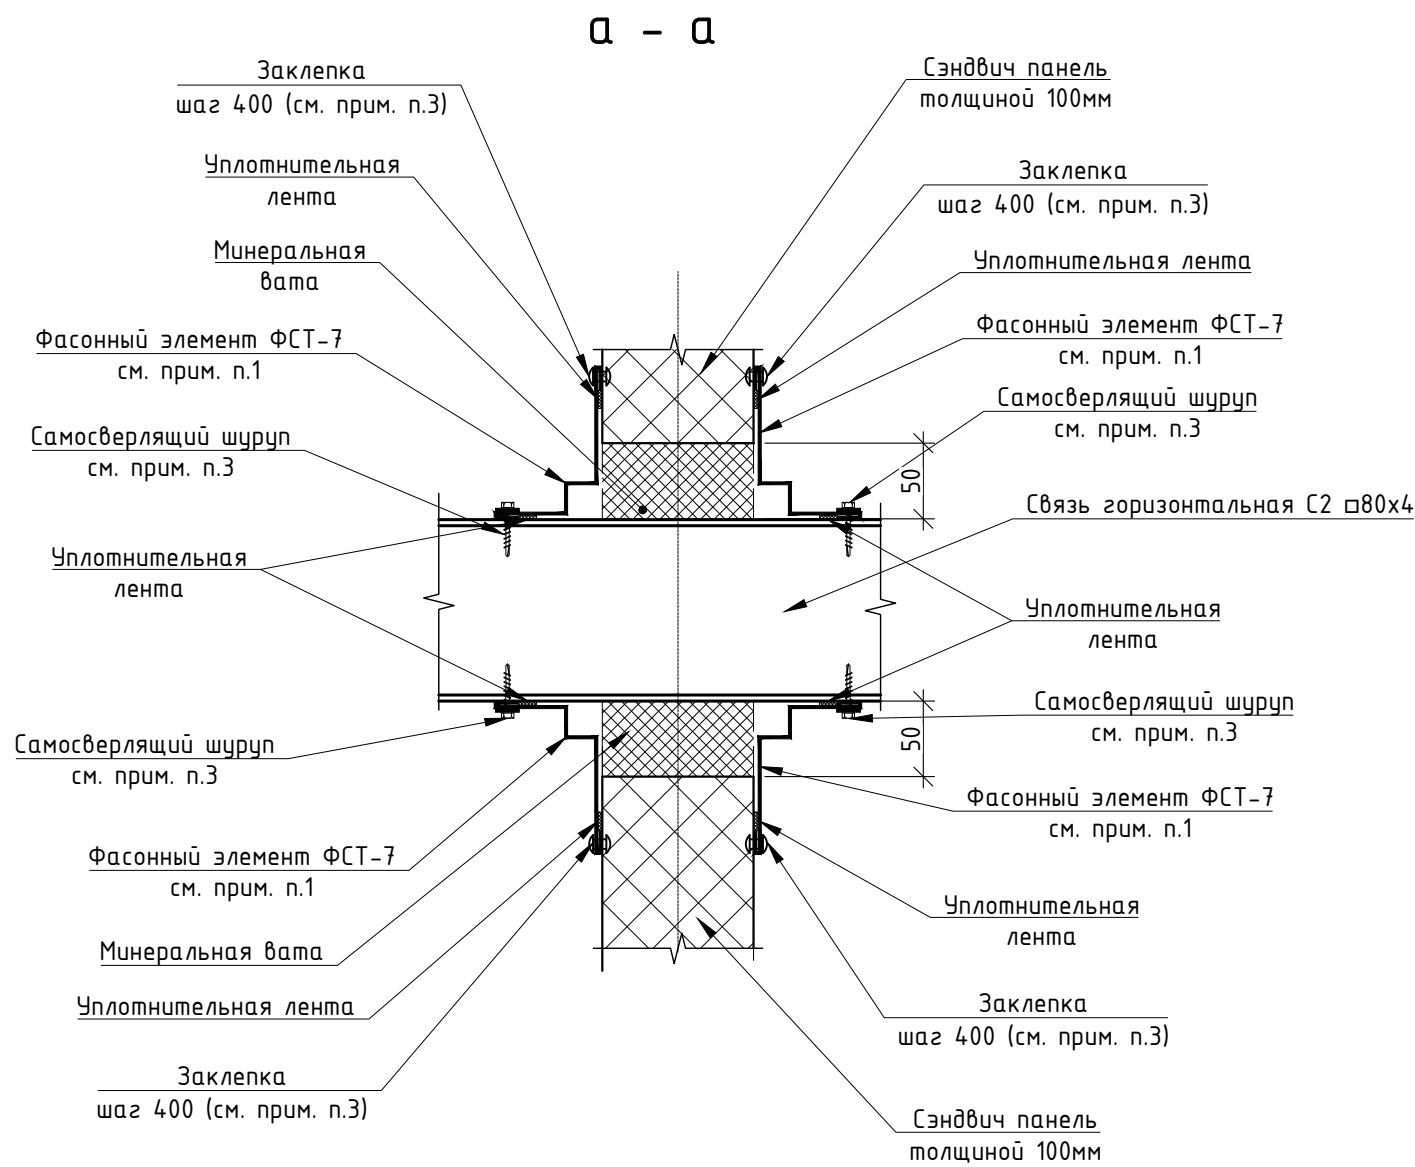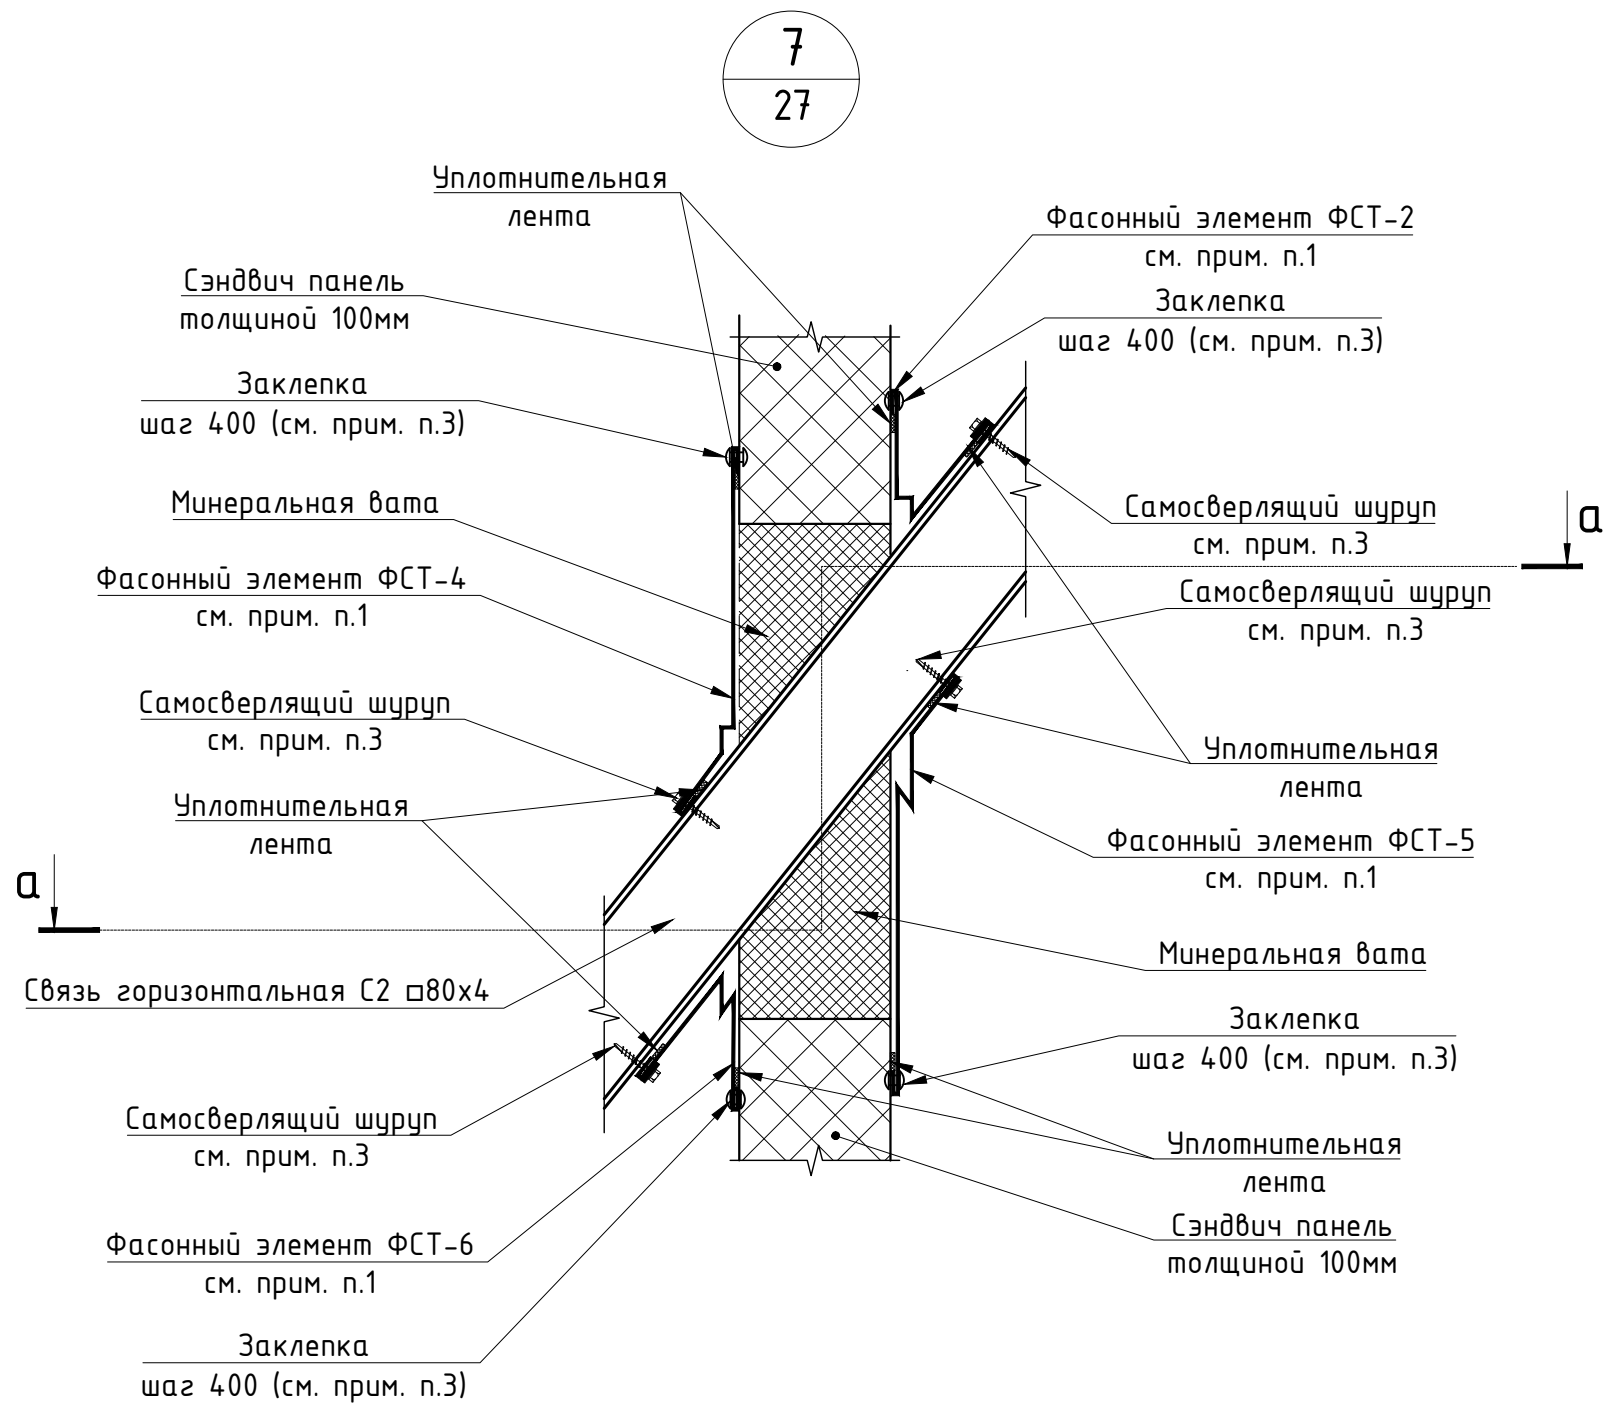

						01-ВЕН/18-СК13-АС1-С1			
						«Производственно-складской комплекс №13 «Industrial City», расположенный по адресу: Московская область, Городской округ Подольск, деревня Новоселки, территория Технопарка, 13»			
Изм.	Кол.уч.	Лист	№ док	Подпись	Дата	Строение 1	Стадия	Лист	Листов
Разраб.		Якунина			04.18		Р	30	
Проверил		Черкасов			04.18	Узлы 7, 8	ООО «КУРСКРЕГИОНПРОЕКТ»		
					04.18				
ГИП		Абдулов			04.18				
Н. контр.		Абдулов			04.18				

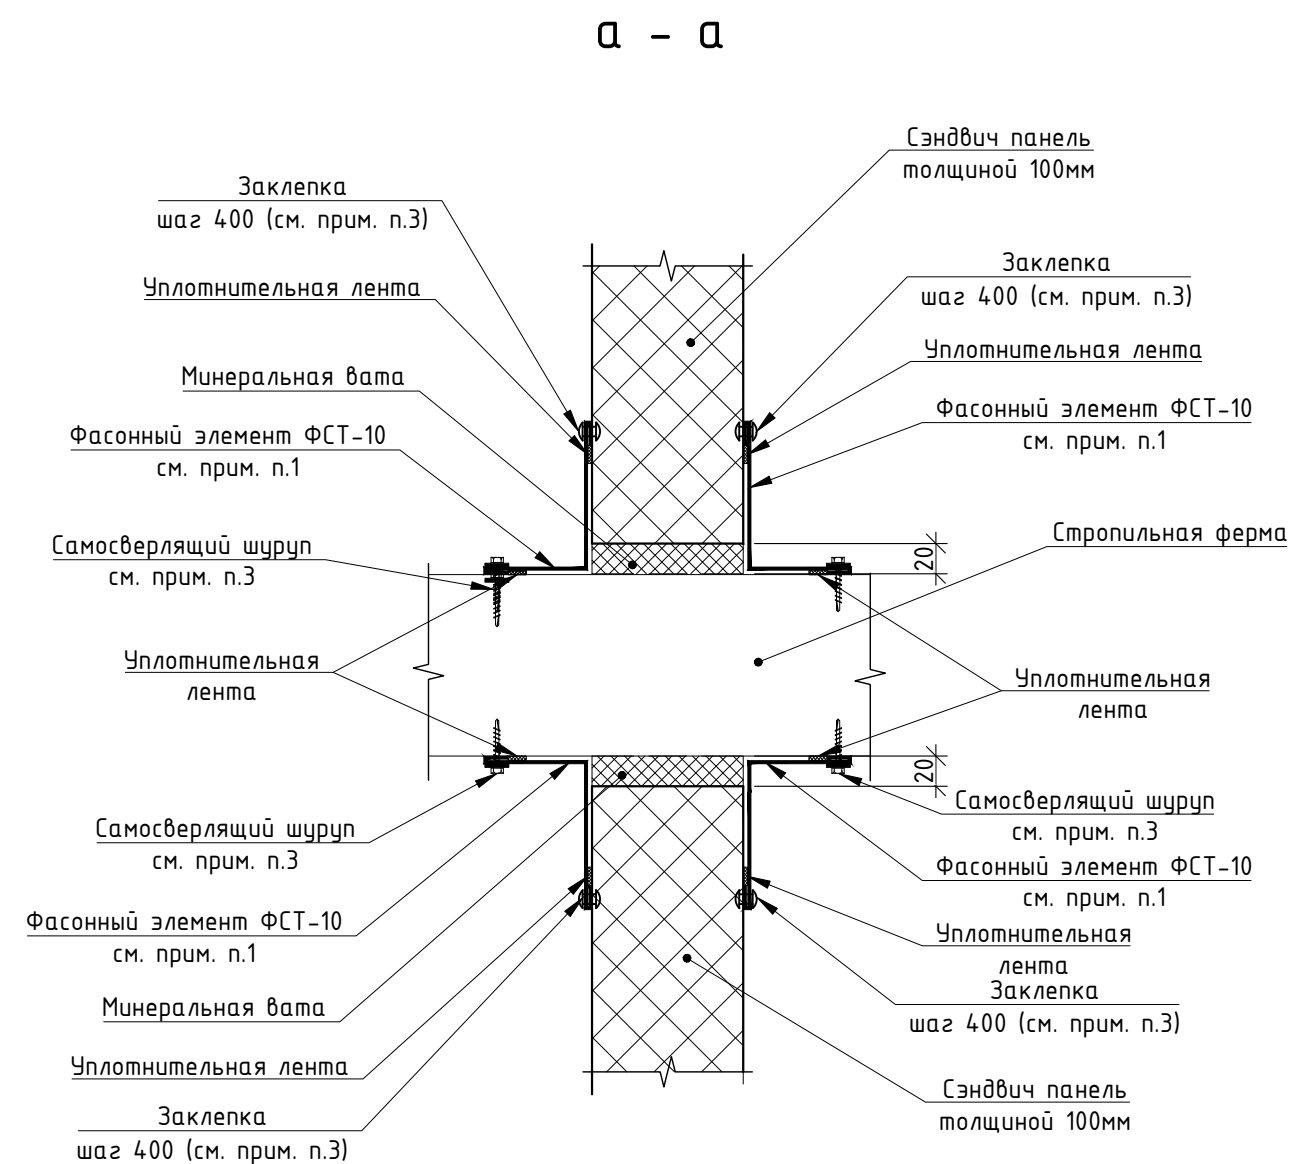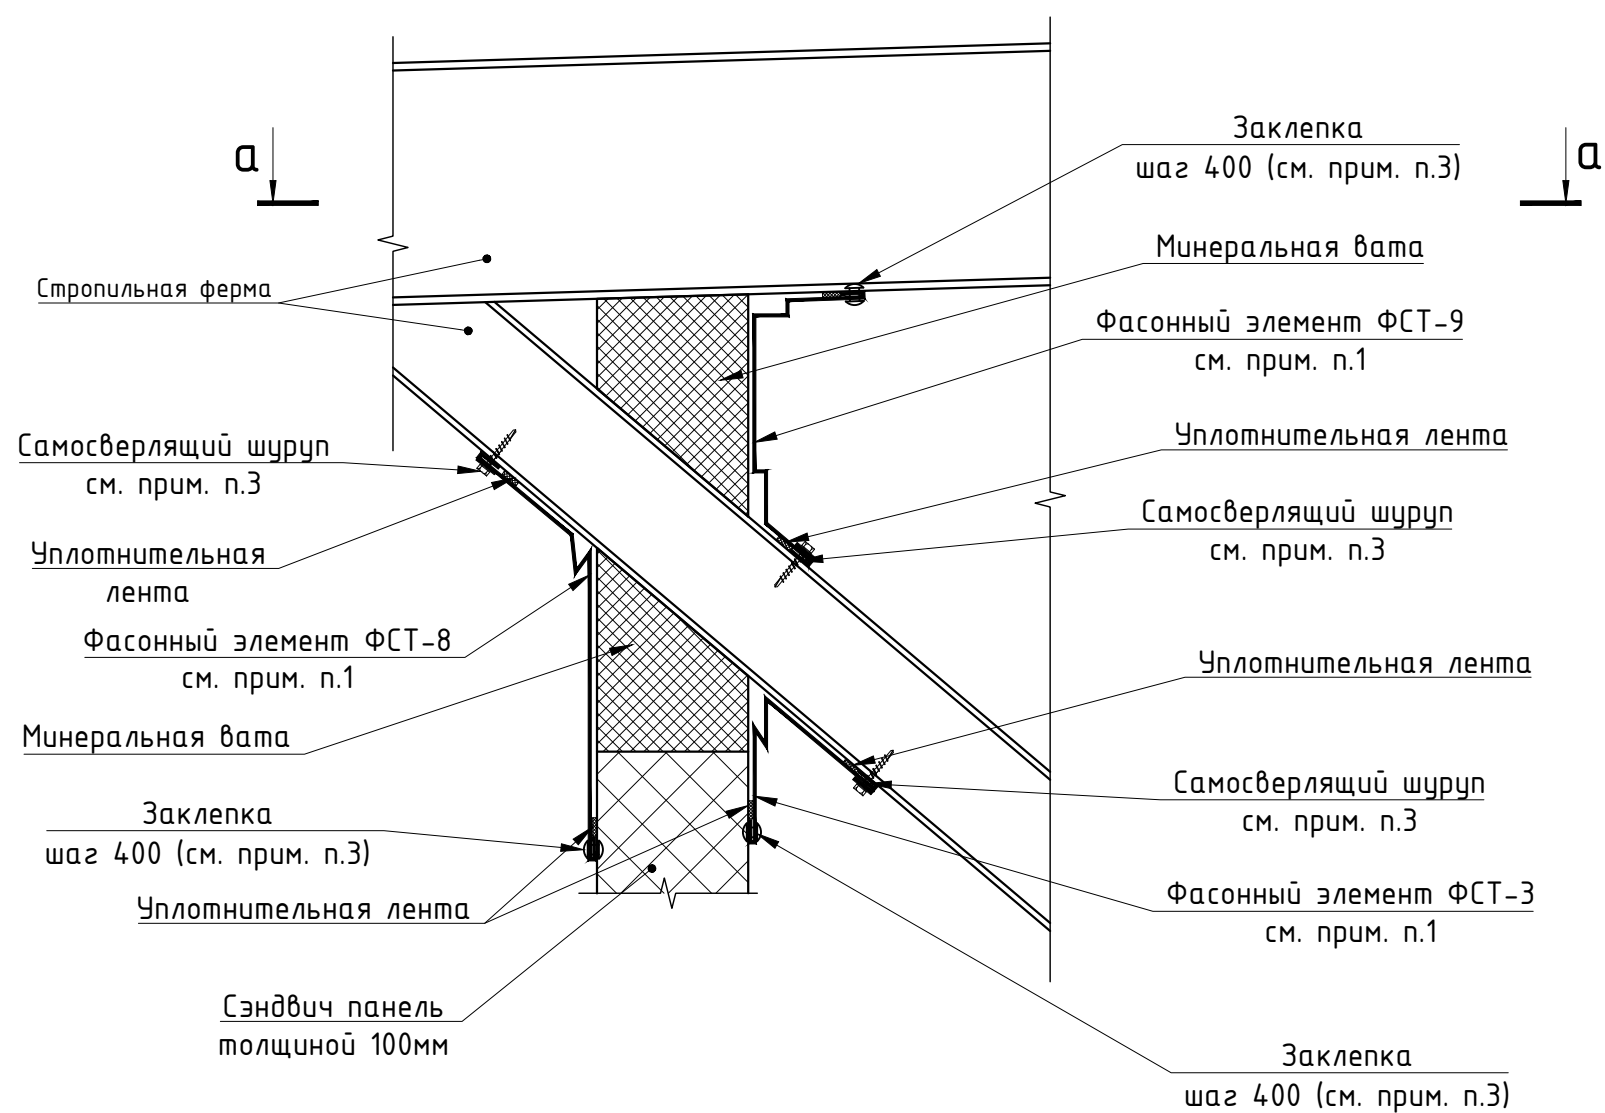


Примечания:
1. Ведомость фасонных элементов см. лист 33.
2. Для крепления сэндвич-панелей использовать самосверлящий шуруп SFS intek SDT 14-A19-5.5x160:
- по 3 шурупа на панель и прогон для сэндвич-панелей средних пролетов;
- по 4 шурупа на панель и прогон для сэндвич-панелей крайних пролетов.
3. Для крепления фасонных элементов использовать:
- заклепку SFS intek ATC-D-3,2x8,0 к панелям;
- самосверлящий шуруп SFS intek SD14-T15-5.5x32 к стальным конструкциям;
4. Фасонные элементы внутри помещения не предусматриваются, отделку откосов выполнить при общей отделке помещений.
5. После монтажа панелей, перед заказом фасонных элементов, необходимо уточнить габариты всех фасонных элементов


Инв. №	подл.
Подпись и дата	Взам. инв. №

01-ВЕН/18-СК13-АС1-С1						
«Производственно-складской комплекс №13 «Industrial City», расположенный по адресу: Московская область, Городской округ Подольск, деревня Новоселки, территория Технопарка, 13»						
Изм.	Кол.уч.	Лист	№ док.	Подпись	Дата	Строение 1
Разраб.	Якунина				04.18	
Проверил	Черкасов				04.18	Узел 10
ГИП	Абдулов				04.18	
Н. контр.	Абдулов				04.18	000"КУРСКРЕГИОНПРОЕКТ"


A
27

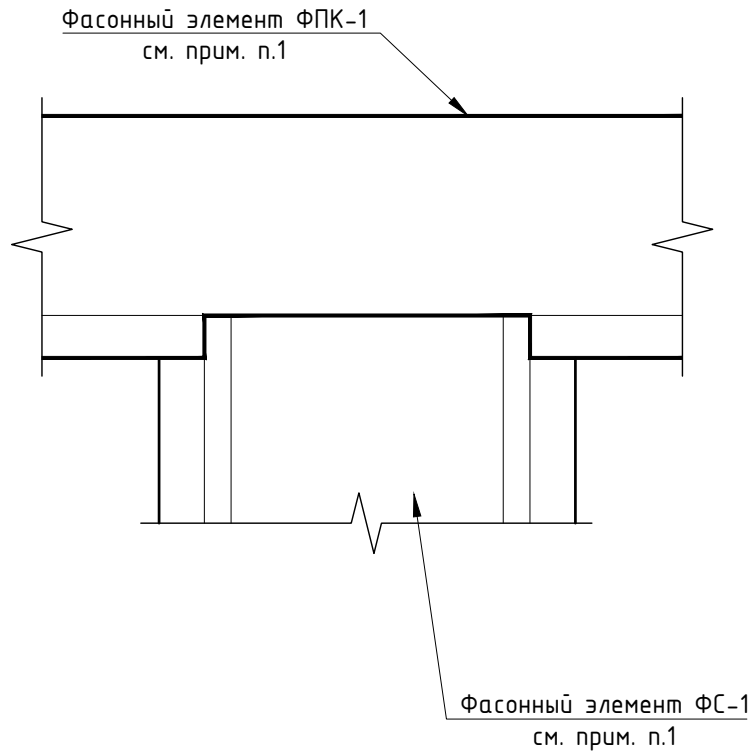


Б
27

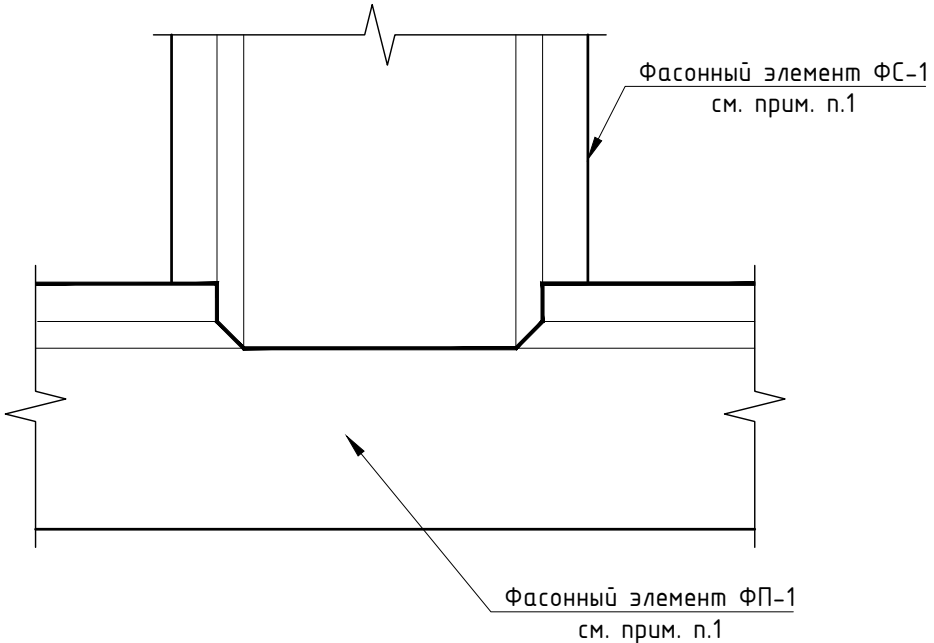

В
27

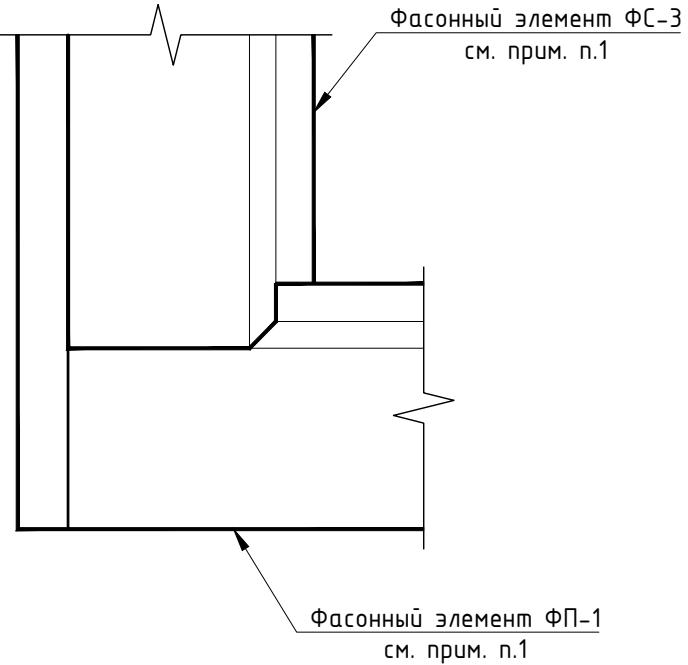

Г
27

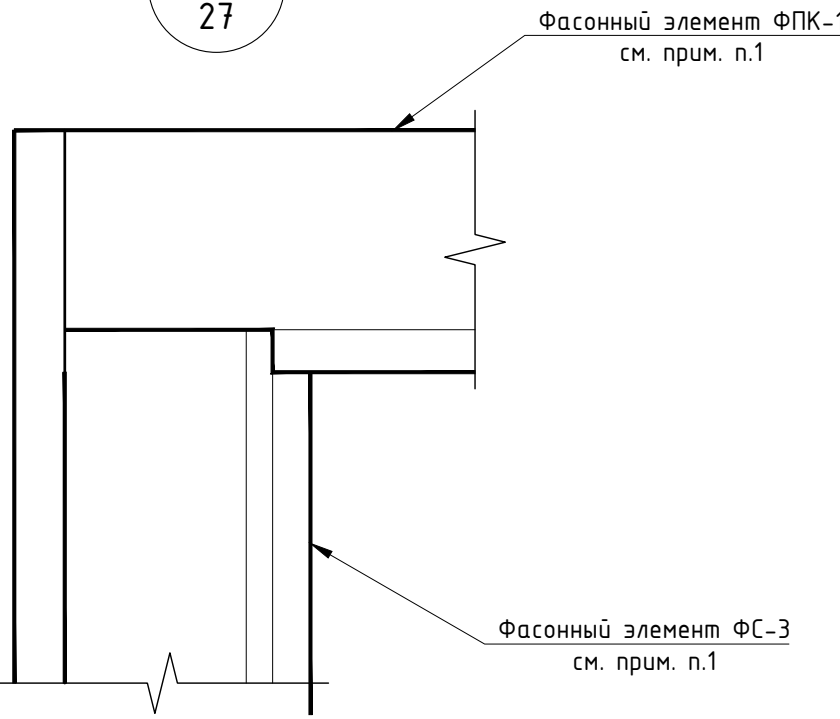

Примечания:
1. Ведомость фасонных элементов см. лист 33.
2. Все стыки фасонных элементов герметизировать герметиком в цвет фасонных элементов.

Инв. № подл.	Подпись и дата	Взам. инв. №

						01-ВЕН/18-СК13-АС1-С1			
						«Производственно-складской комплекс №13 «Industrial City», расположенный по адресу: Московская область, Городской округ Подольск, деревня Новоселки, территория Технопарка, 13»			
Изм.	Кол.уч.	Лист	№ док	Подпись	Дата	Строение 1	Стадия	Лист	Листов
Разраб.		Якунина			04.18		Р	32	
Проверил		Черкасов			04.18				
						Узлы А-Г	ООО "КУРСКРЕГИОНПРОЕКТ"		
ГИП		Авдулов			04.18				
Н. контр.		Авдулов			04.18				

Марка поз.	Эскиз	Ширина развертки, мм	Кол-во, п.м.	Площадь, м ²	Примечание
ФС-1		340	264.00	89.76	RAL 9003
ФС-3		390	316.80	123.55	RAL 9003
ФП-1		260	370.48	96.32	RAL 9003
ФПК-1		430	370.48	159.31	RAL 9003
ФСТ-2		205	4.62	0.95	RAL 9003
ФСТ-3		245	11.55	2.83	RAL 9003

Марка поз.	Эскиз	Ширина развертки, мм	Кол-во, п.м.	Площадь, м ²	Примечание
ФСТ-4		290	4.62	1.34	RAL 9003
ФСТ-5		350	4.62	1.62	RAL 9003
ФСТ-6		230	4.62	1.06	RAL 9003
ФСТ-7		190	30.80	5.85	RAL 9003
ФСТ-8		340	11.55	3.93	RAL 9003
ФСТ-9		300	11.55	3.47	RAL 9003
ФСТ-10		190	80.08	13.83	RAL 9003

						01-ВЕН/18-СК13-АС1-С1			
						«Производственно-складской комплекс №13 «Industrial City», расположенный по адресу: Московская область, Городской округ Подольск, деревня Новоселки, территория Технопарка, 13»			
Изм.	Кол.уч.	Лист	№ док	Подпись	Дата	Строение 1	Стадия	Лист	Листов
Разраб.		Якунина			04.18		Р	33	
Проверил		Черкасов			04.18	Ведомость фасонных элементов	ООО "КУРСРЕГИОНПРОЕКТ"		
ГИП		Авдулов			04.18				
Н. контр.		Авдулов			04.18				